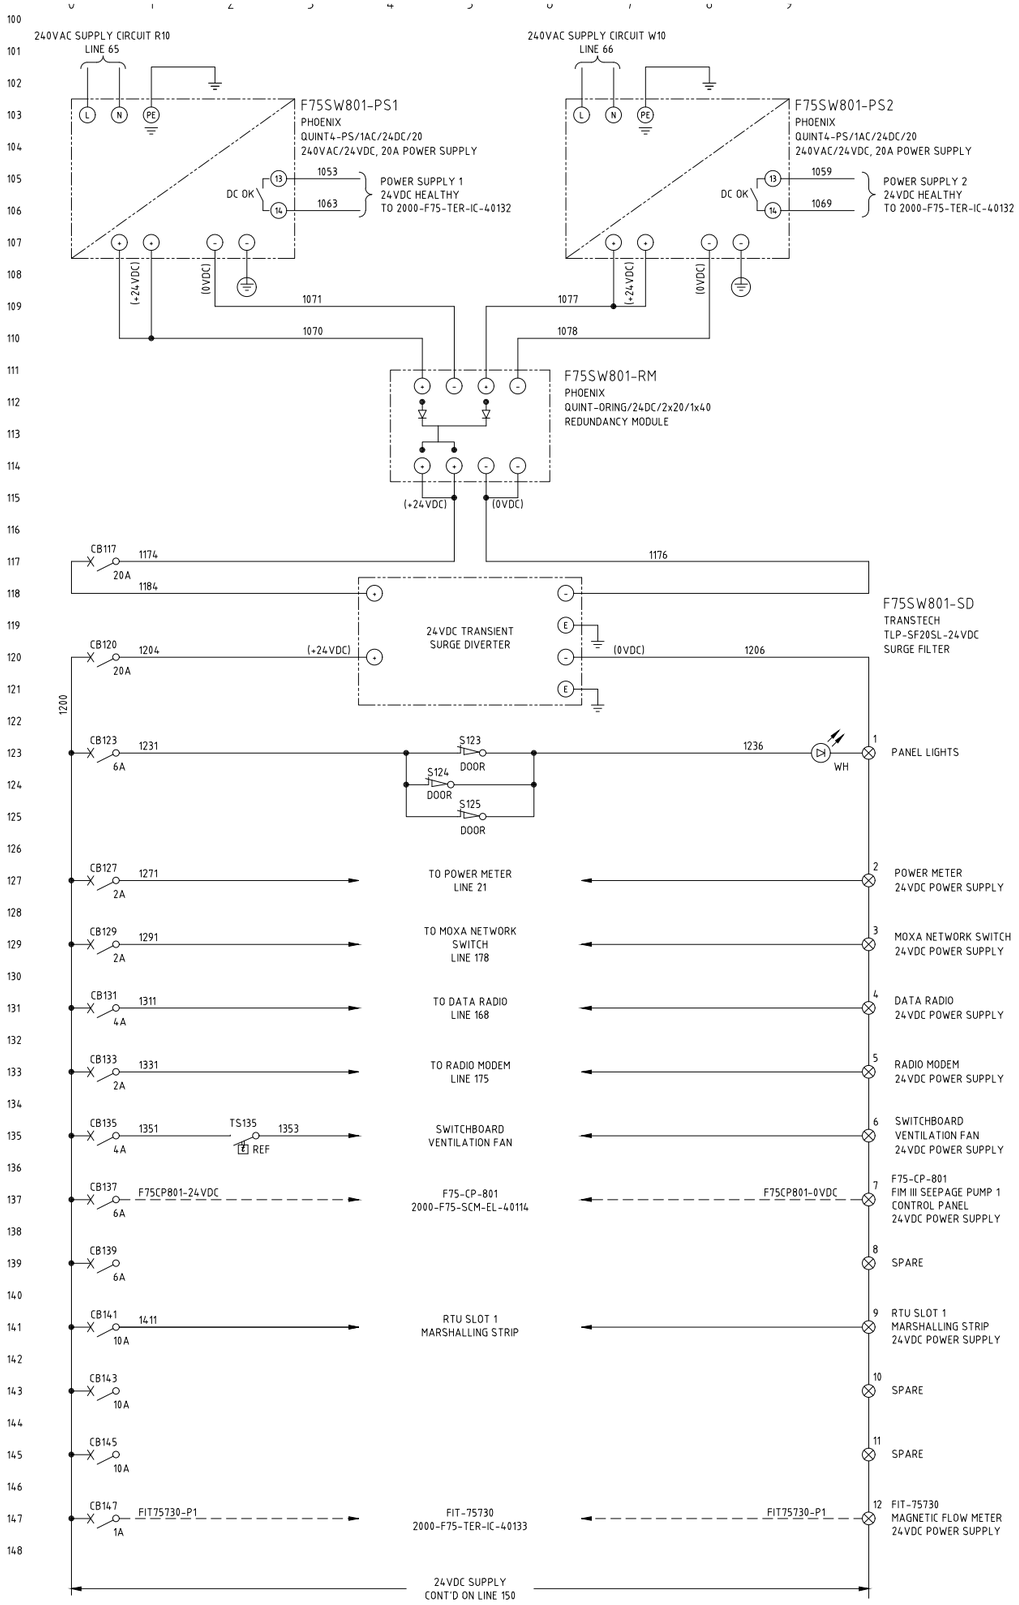
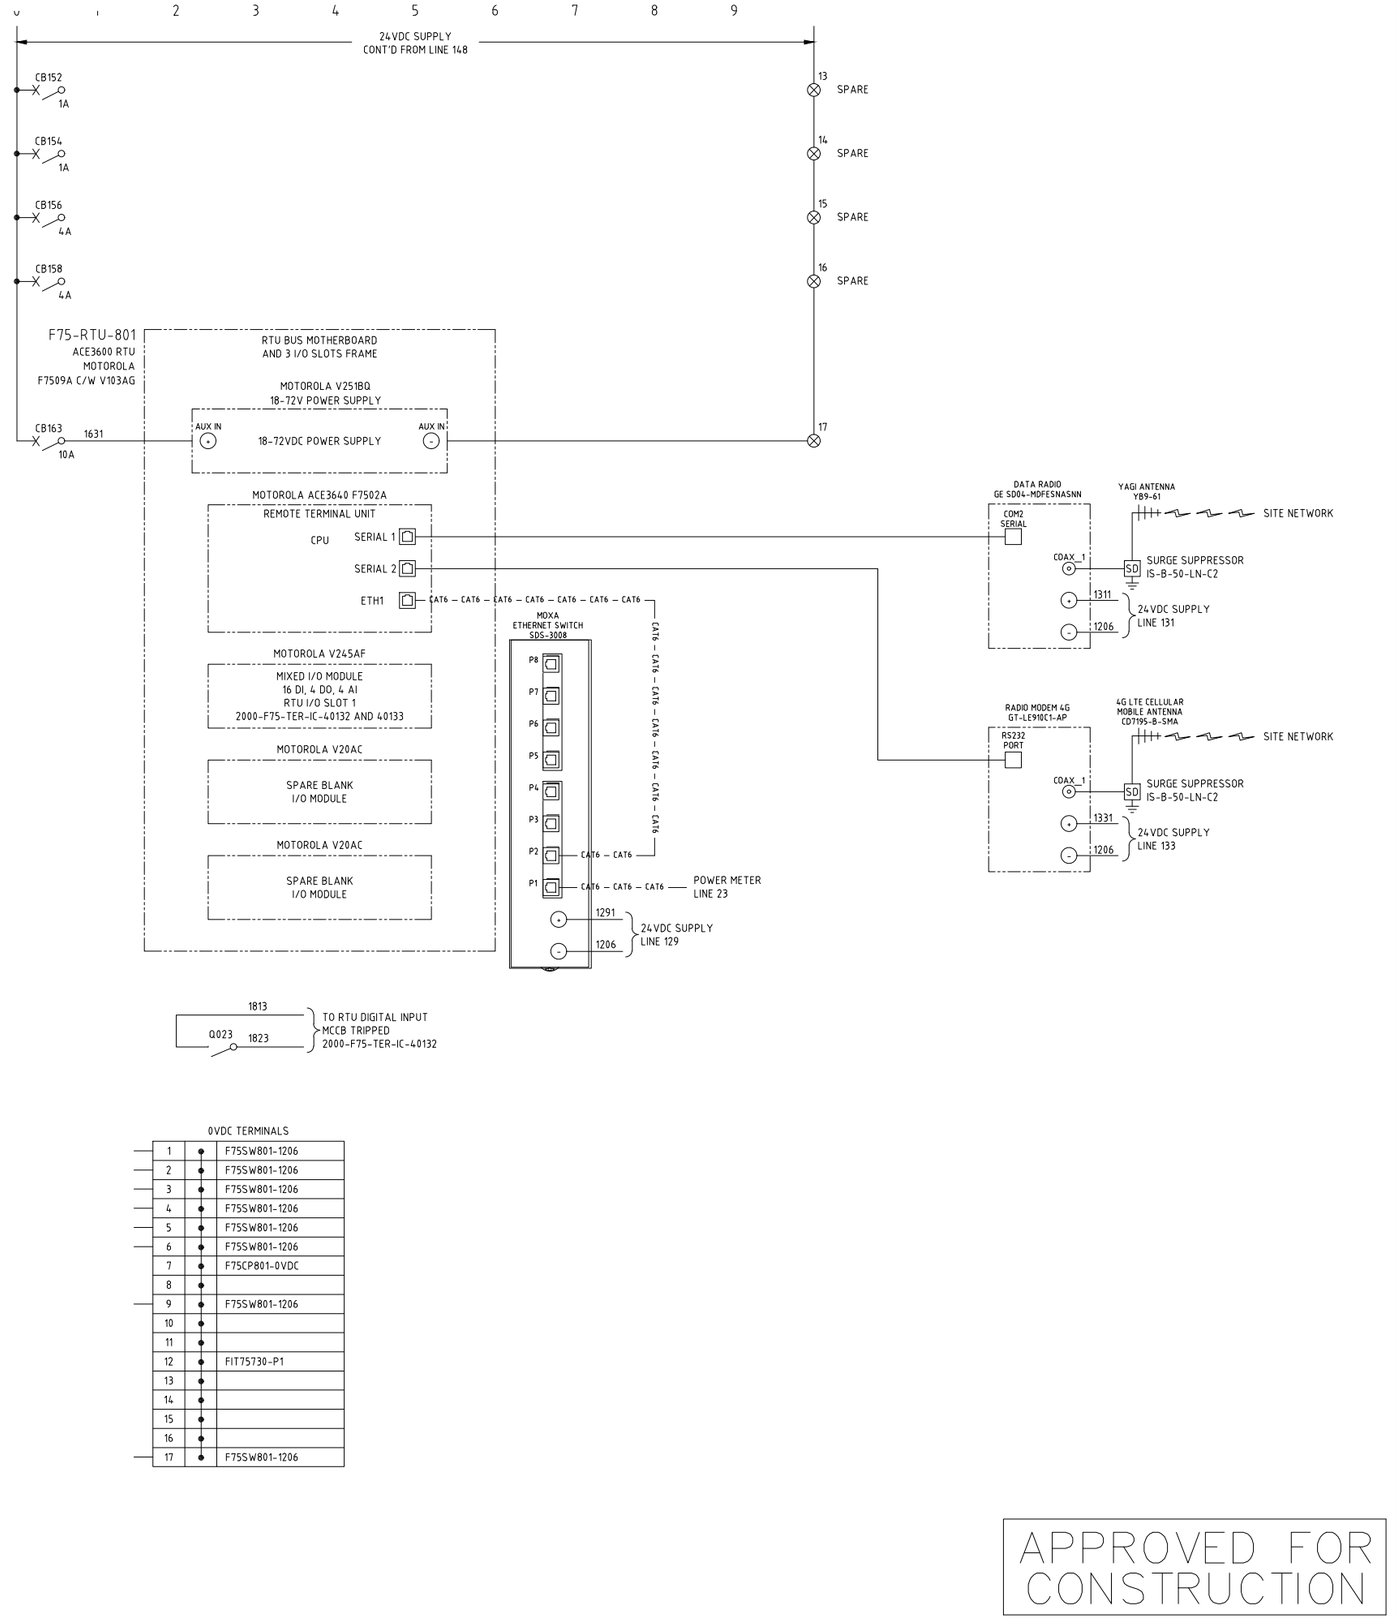



0VDC TERMINALS

| | | |
|---|---|---|
| 1 | • | F75SW801-1206 |
| 2 | • | F75SW801-1206 |
| 3 | • | F75SW801-1206 |
| 4 | • | F75SW801-1206 |
| 5 | • | F75SW801-1206 |
| 6 | • | F75SW801-1206 |
| 7 | • | F75CP801-0VDC |
| 8 | • | |
| 9 | • | F75SW801-1206 |
| 10 | • | |
| 11 | • | |
| 12 | • | FIT75730-P1 |
| 13 | • | |
| 14 | • | |
| 15 | • | |
| 16 | • | |
| 17 | • | F75SW801-1206 |

APPROVED FOR CONSTRUCTION

# 2000-F75-SCM-EL-40123_Rev0

FIM III tailings dam F75-SW-801 FIM III TSF switchboard 3 schematic diagram sheet 2