Docusign Envelope ID: 1C123F4F-48ED-425D-A3F4-754BD8FC0FD6

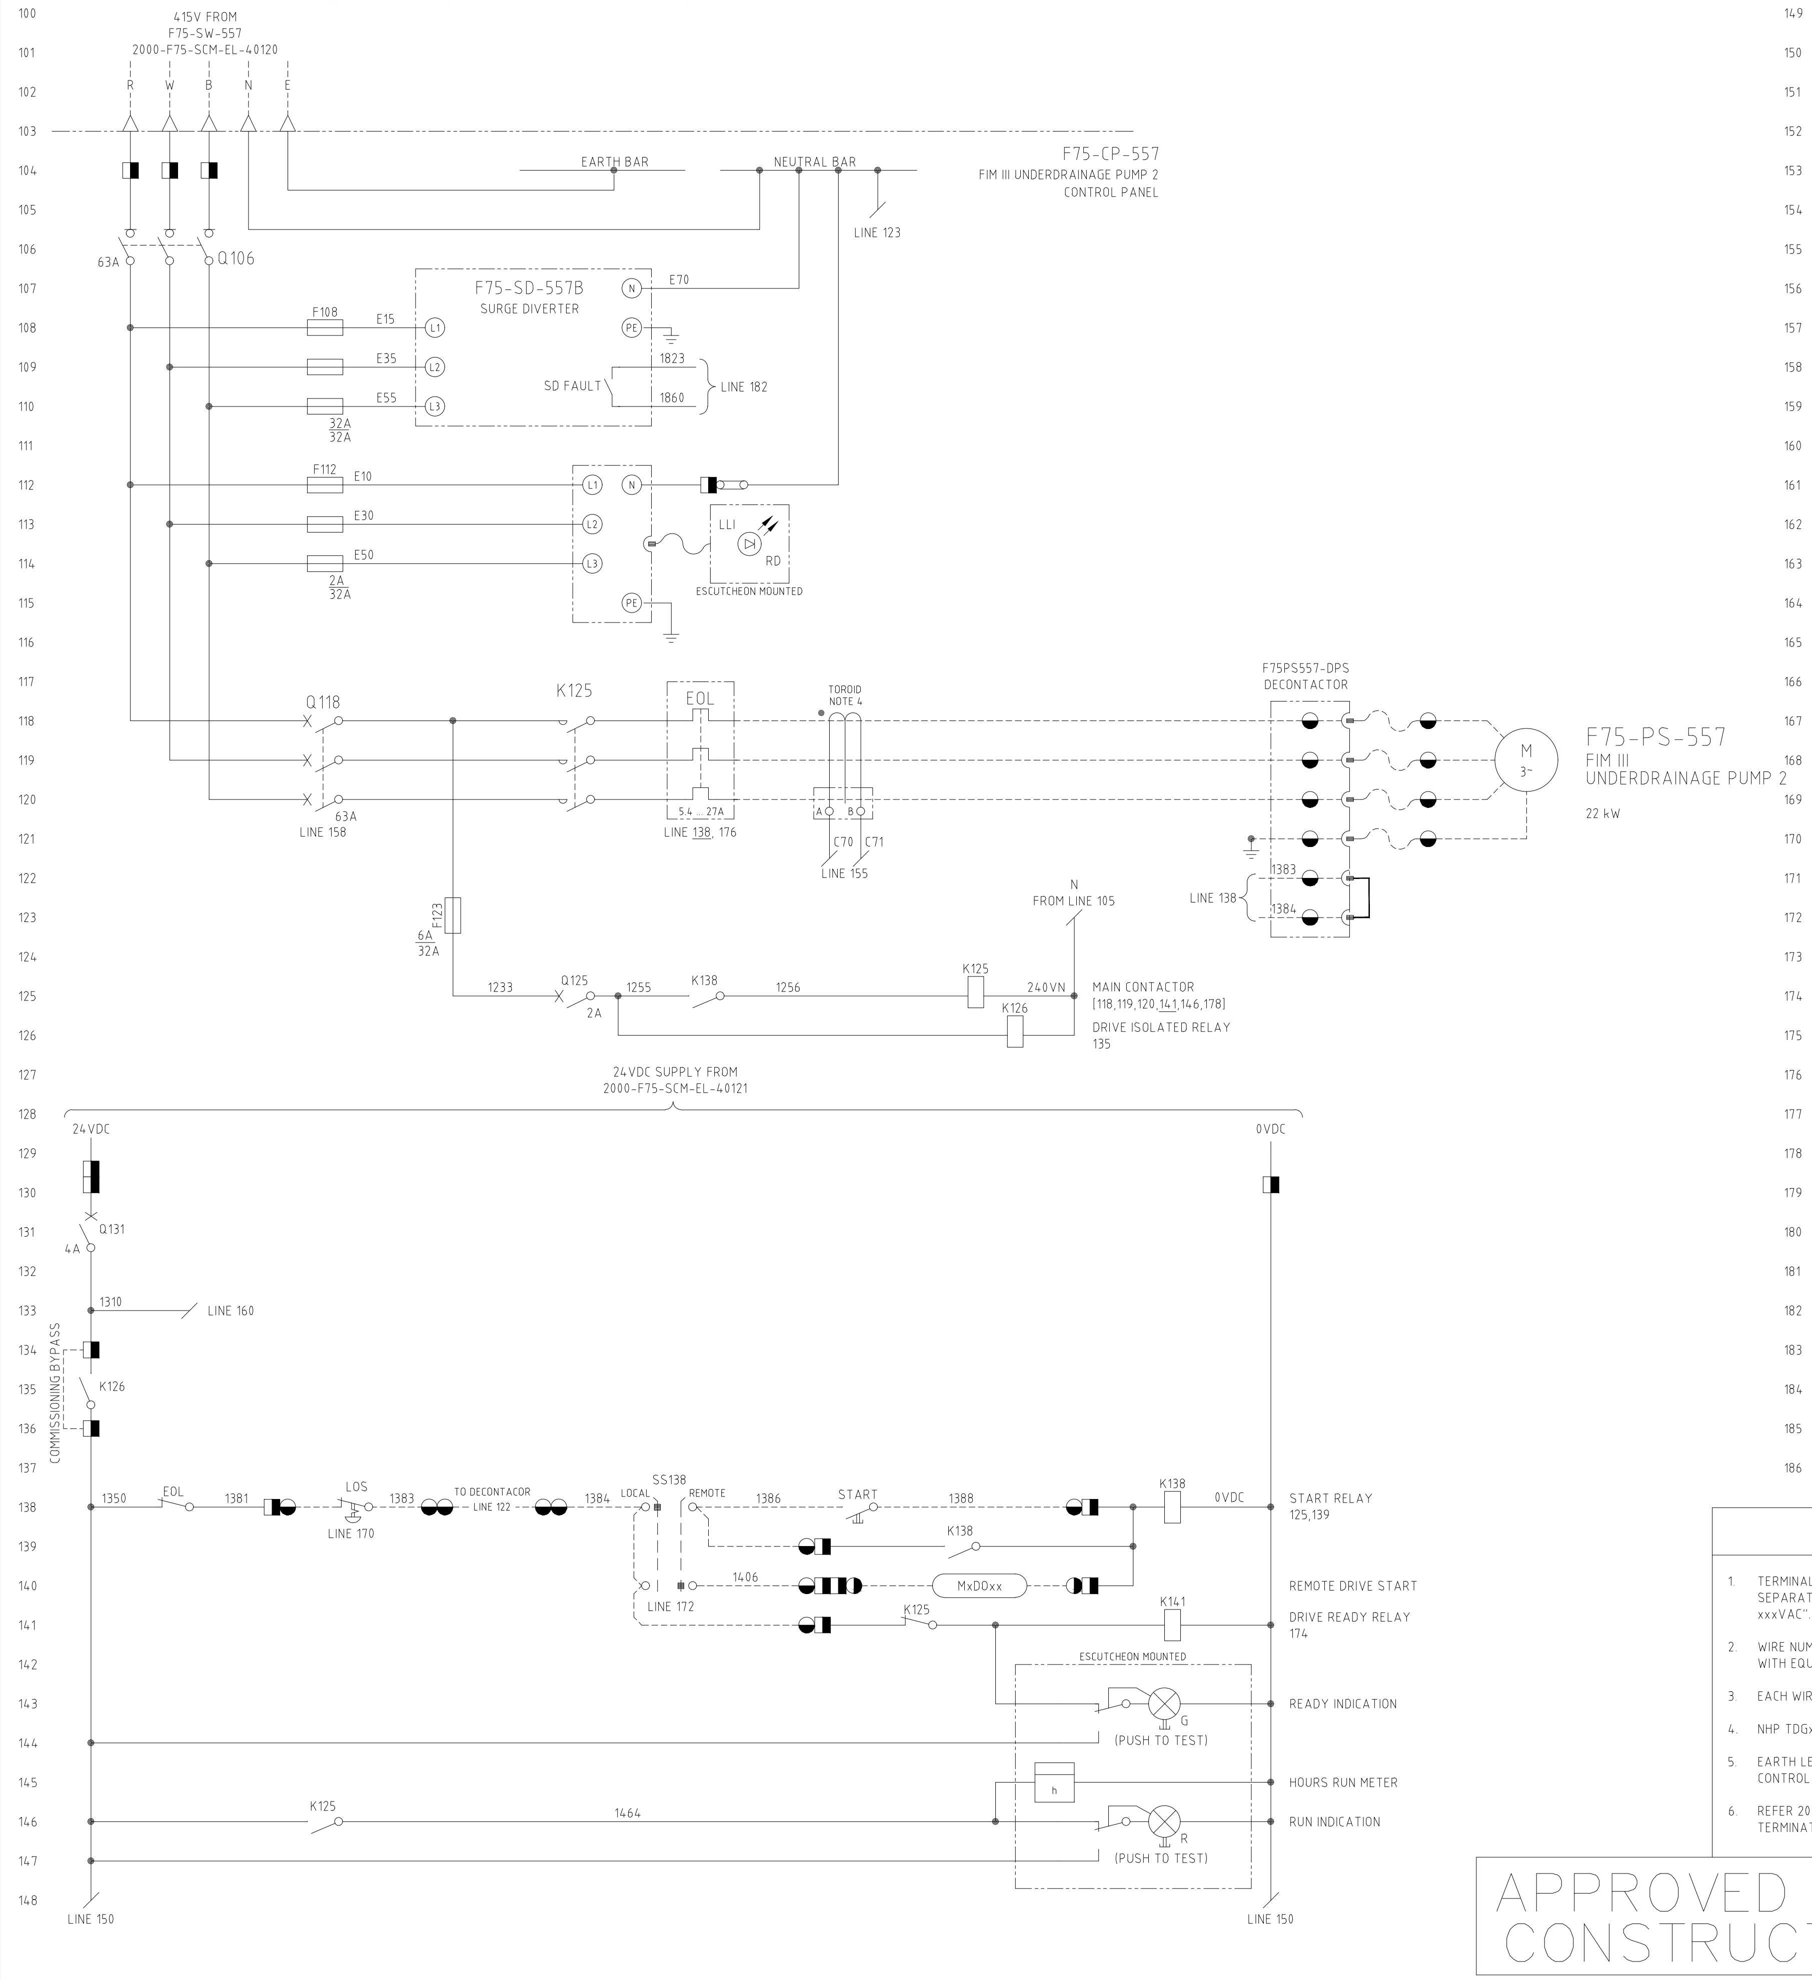

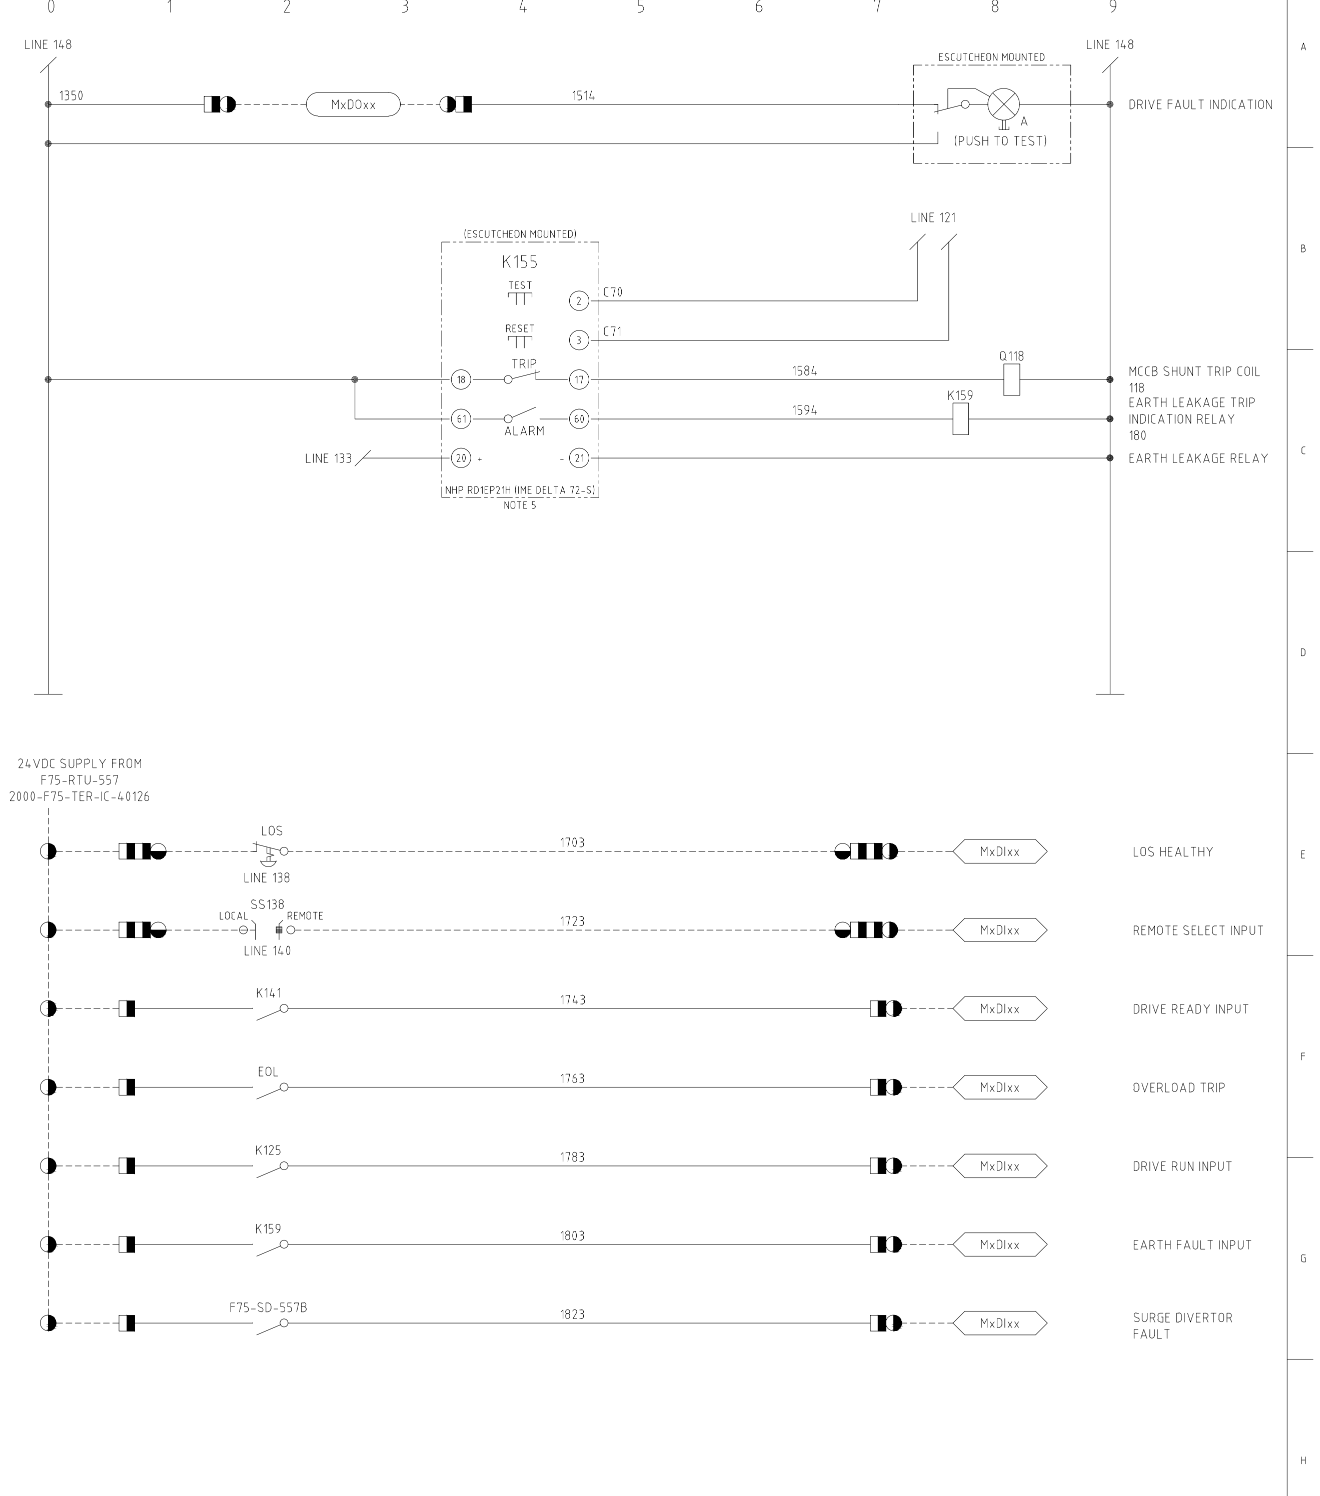

NOTES

1. TERMINALS ON TERMINAL STRIPS ABOVE 50VAC SHALL HAVE A SEPARATE PERSPEX SHROUD AND SHALL BE LABELLED "DANGER xxxVAC".
2. WIRE NUMBER FERRULES ON TERMINAL STRIP SHALL BE PREFIXED WITH EQUIPMENT NUMBER e.g. FxxPSxxx-1200.
3. EACH WIRE SHALL BE IDENTIFIED AT BOTH ENDS WITH FERRULES.
4. NHP TDGx2 TOROID TO SUIT CABLE DIAMETER.
5. EARTH LEAKAGE RELAY USER INTERFACE TO BE MOUNTED ON CONTROL PANEL ESCUTCHEON.
6. REFER 2000-F75-LST-IC-40004 FOR RTU I/O ADDRESSES AND TERMINATION DETAILS.

LEGEND

MxDIxx	RTU DIGITAL INPUT
MxDOxx	RTU DIGITAL OUTPUT
⊗	SWITCHBOARD TERMINAL
⧓	VSD TERMINAL
◒	FIELD TERMINAL
◑	RTU TERMINAL
◨	CONTROL PANEL TERMINAL
ⓧ	DEVICE TERMINAL
⊗ cc	INDICATION LAMP cc = COLOUR

TERMINATION LEGEND

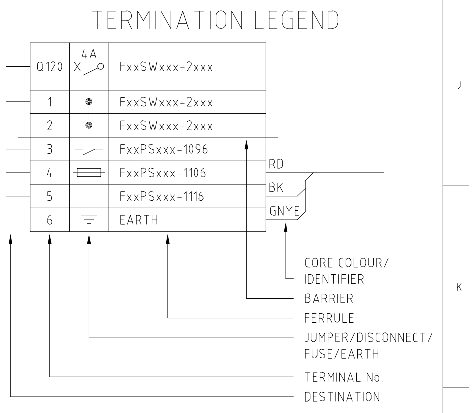

APPROVED FOR CONSTRUCTION

REFERENCES	DWG No	REV	DATE	REVISION	DRN	CHK	TECH APP	PROJ APP
F75-RTU-557 FIM III TSF SWITCHBOARD 2 RTU TERMINATION DIAGRAM SHEET 1	2000-F75-TER-IC-40126							
F75-CP-557 FIM III UNDERDRAINAGE PUMP 2 CONTROL PANEL GENERAL ARRANGEMENT SHEET 1	2000-F75-DRG-EL-40125							
F75-CP-557 FIM III UNDERDRAINAGE PUMP 2 CONTROL PANEL TERMINATION DIAGRAM	2000-F75-TER-EL-40112							
F75-SW-557 FIM III TSF SWITCHBOARD 2 SCHEMATIC DIAGRAM SHEET 2	2000-F75-SCM-EL-40121							
F75-SW-557 FIM III TSF SWITCHBOARD 2 SCHEMATIC DIAGRAM SHEET 1	2000-F75-SCM-EL-40120							
GENERAL NOTES AND STANDARD DRAWINGS INDEX	2000-F00-STD-EL-10001	0	29.MAY.25	APPROVED FOR CONSTRUCTION	Initial TG	Initial KVN	Initial KVN	DS TH

NORTHERN STAR
RESOURCES LIMITED

DRA PACIFIC (PTY) LIMITED

DRAWN	Signed by: J.TORRALBA John Torralba B614B6499345438...	03.APR.25
CHECKED	Signed by: J.Y.WEE Jia Yang Wee 7432A8E609F94A1...	03.APR.25
DESIGNED	Signed by: J.TORRALBA John Torralba B614B6499345438...	03.APR.25
TECH APP	Signed by: K.VAN NAMEN Kate van Namen F5496A0ED06E479...	29.APR.25
PROJ APP	DocuSigned by: T.HAMDORF Tom Hamdorf E8201606A17B4A9...	29.MAY.25
CLIENT APP		

PROJECT: KCGM
FIM TSF PROJECT

TITLE: FIM III TAILINGS DAM
F75-CP-557 FIM III UNDERDRAINAGE PUMP 2 CP
SCHEMATIC DIAGRAM

A1 | SCALE NTS | DRG No. 2000-F75-SCM-EL-40112 | REV 0