


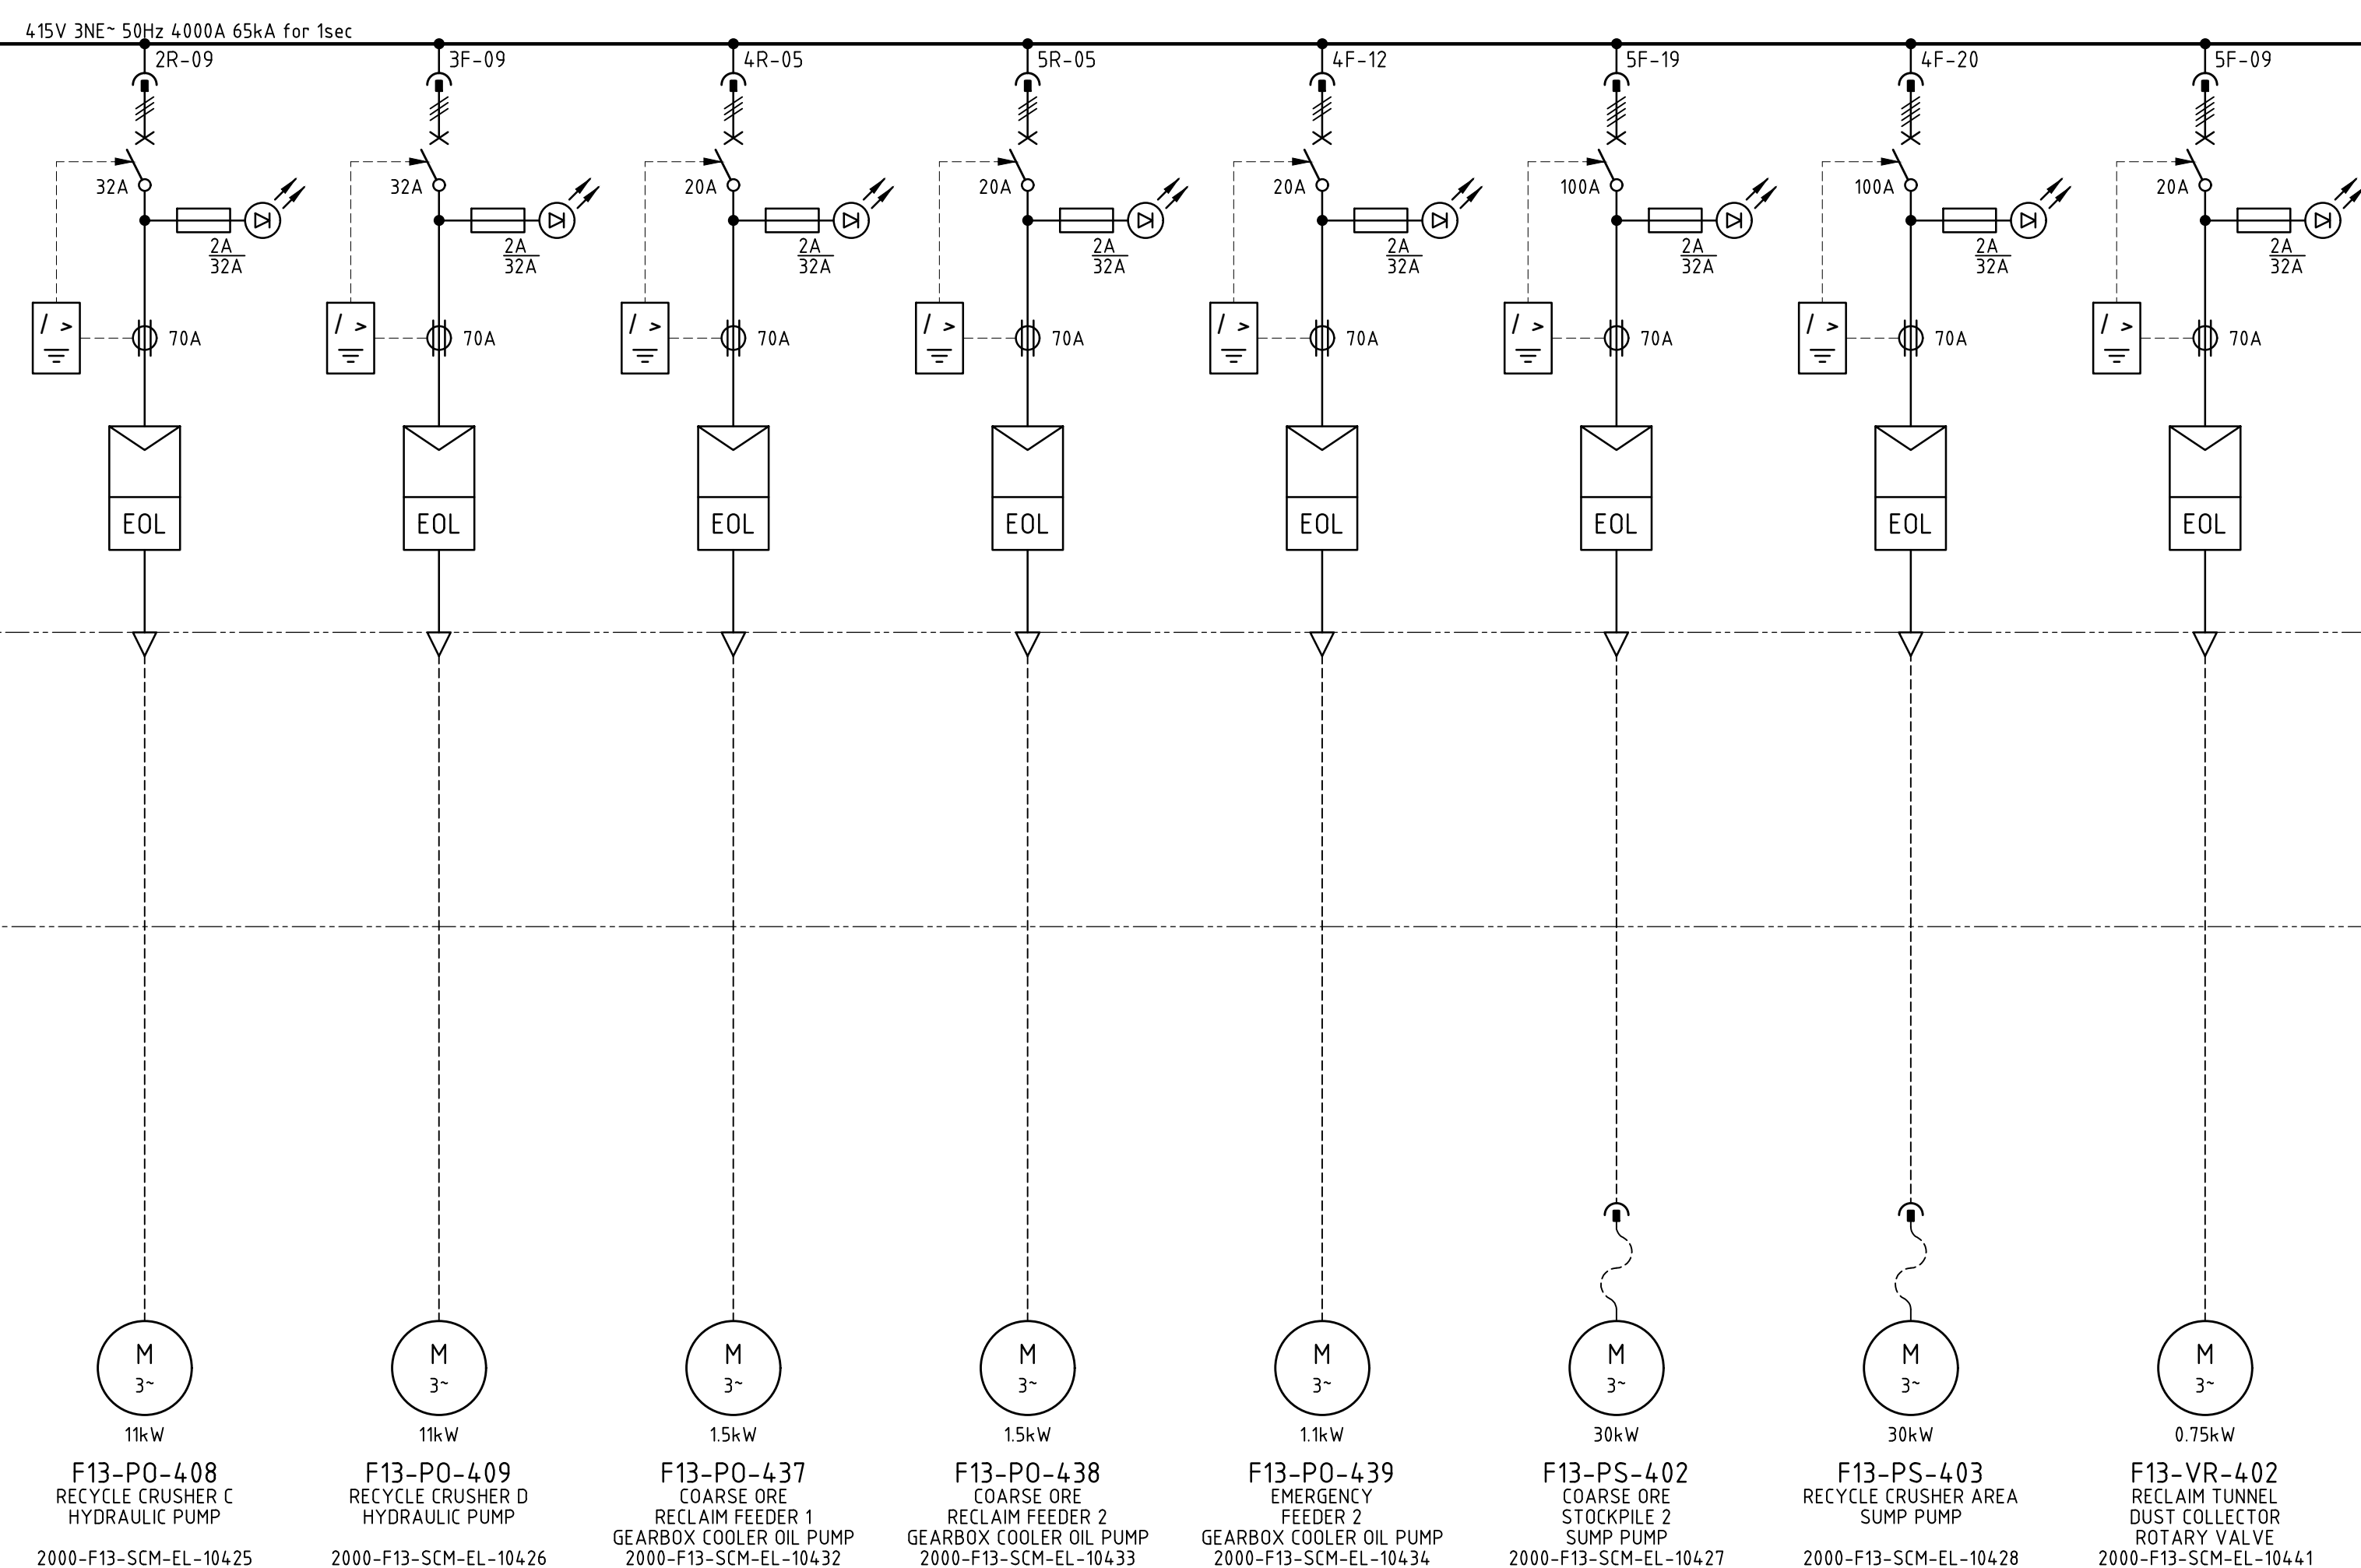

CONTINUED ON SHT 3
2000-F13-SLD-EL-104.03

[illegible]

PRIMERO
primero.com.au | DESIGN | CONSTRUCT | OPERATE

PRIMERO PROJECT NUMBER: **23517**

PROJECT:	NORTHERN STAR RESOURCES LTD KCGM GROWTH PROJECT
TITLE:	MILLING & CLASSIFICATION - RECYCLE CRUSHING F13-SW-014 415V MCC SINGLE LINE DIAGRAM SHEET 4

INFORMATION AND REPRESENTATIONS ON THIS DRAWING ARE THE INTELLECTUAL PROPERTY OF
PRIMERO UNLESS SPECIFICALLY IDENTIFIED OTHERWISE. ALL RIGHTS INCLUDING USE RESERVED

SHEET	SCALE	DRG No.	REVISION
A1	NONE	2000-F13-SLD-EL-10404	2

LEGEND

1. REFER TO SHEET 1.

NOTES

1. REFER TO SHEET 1.