


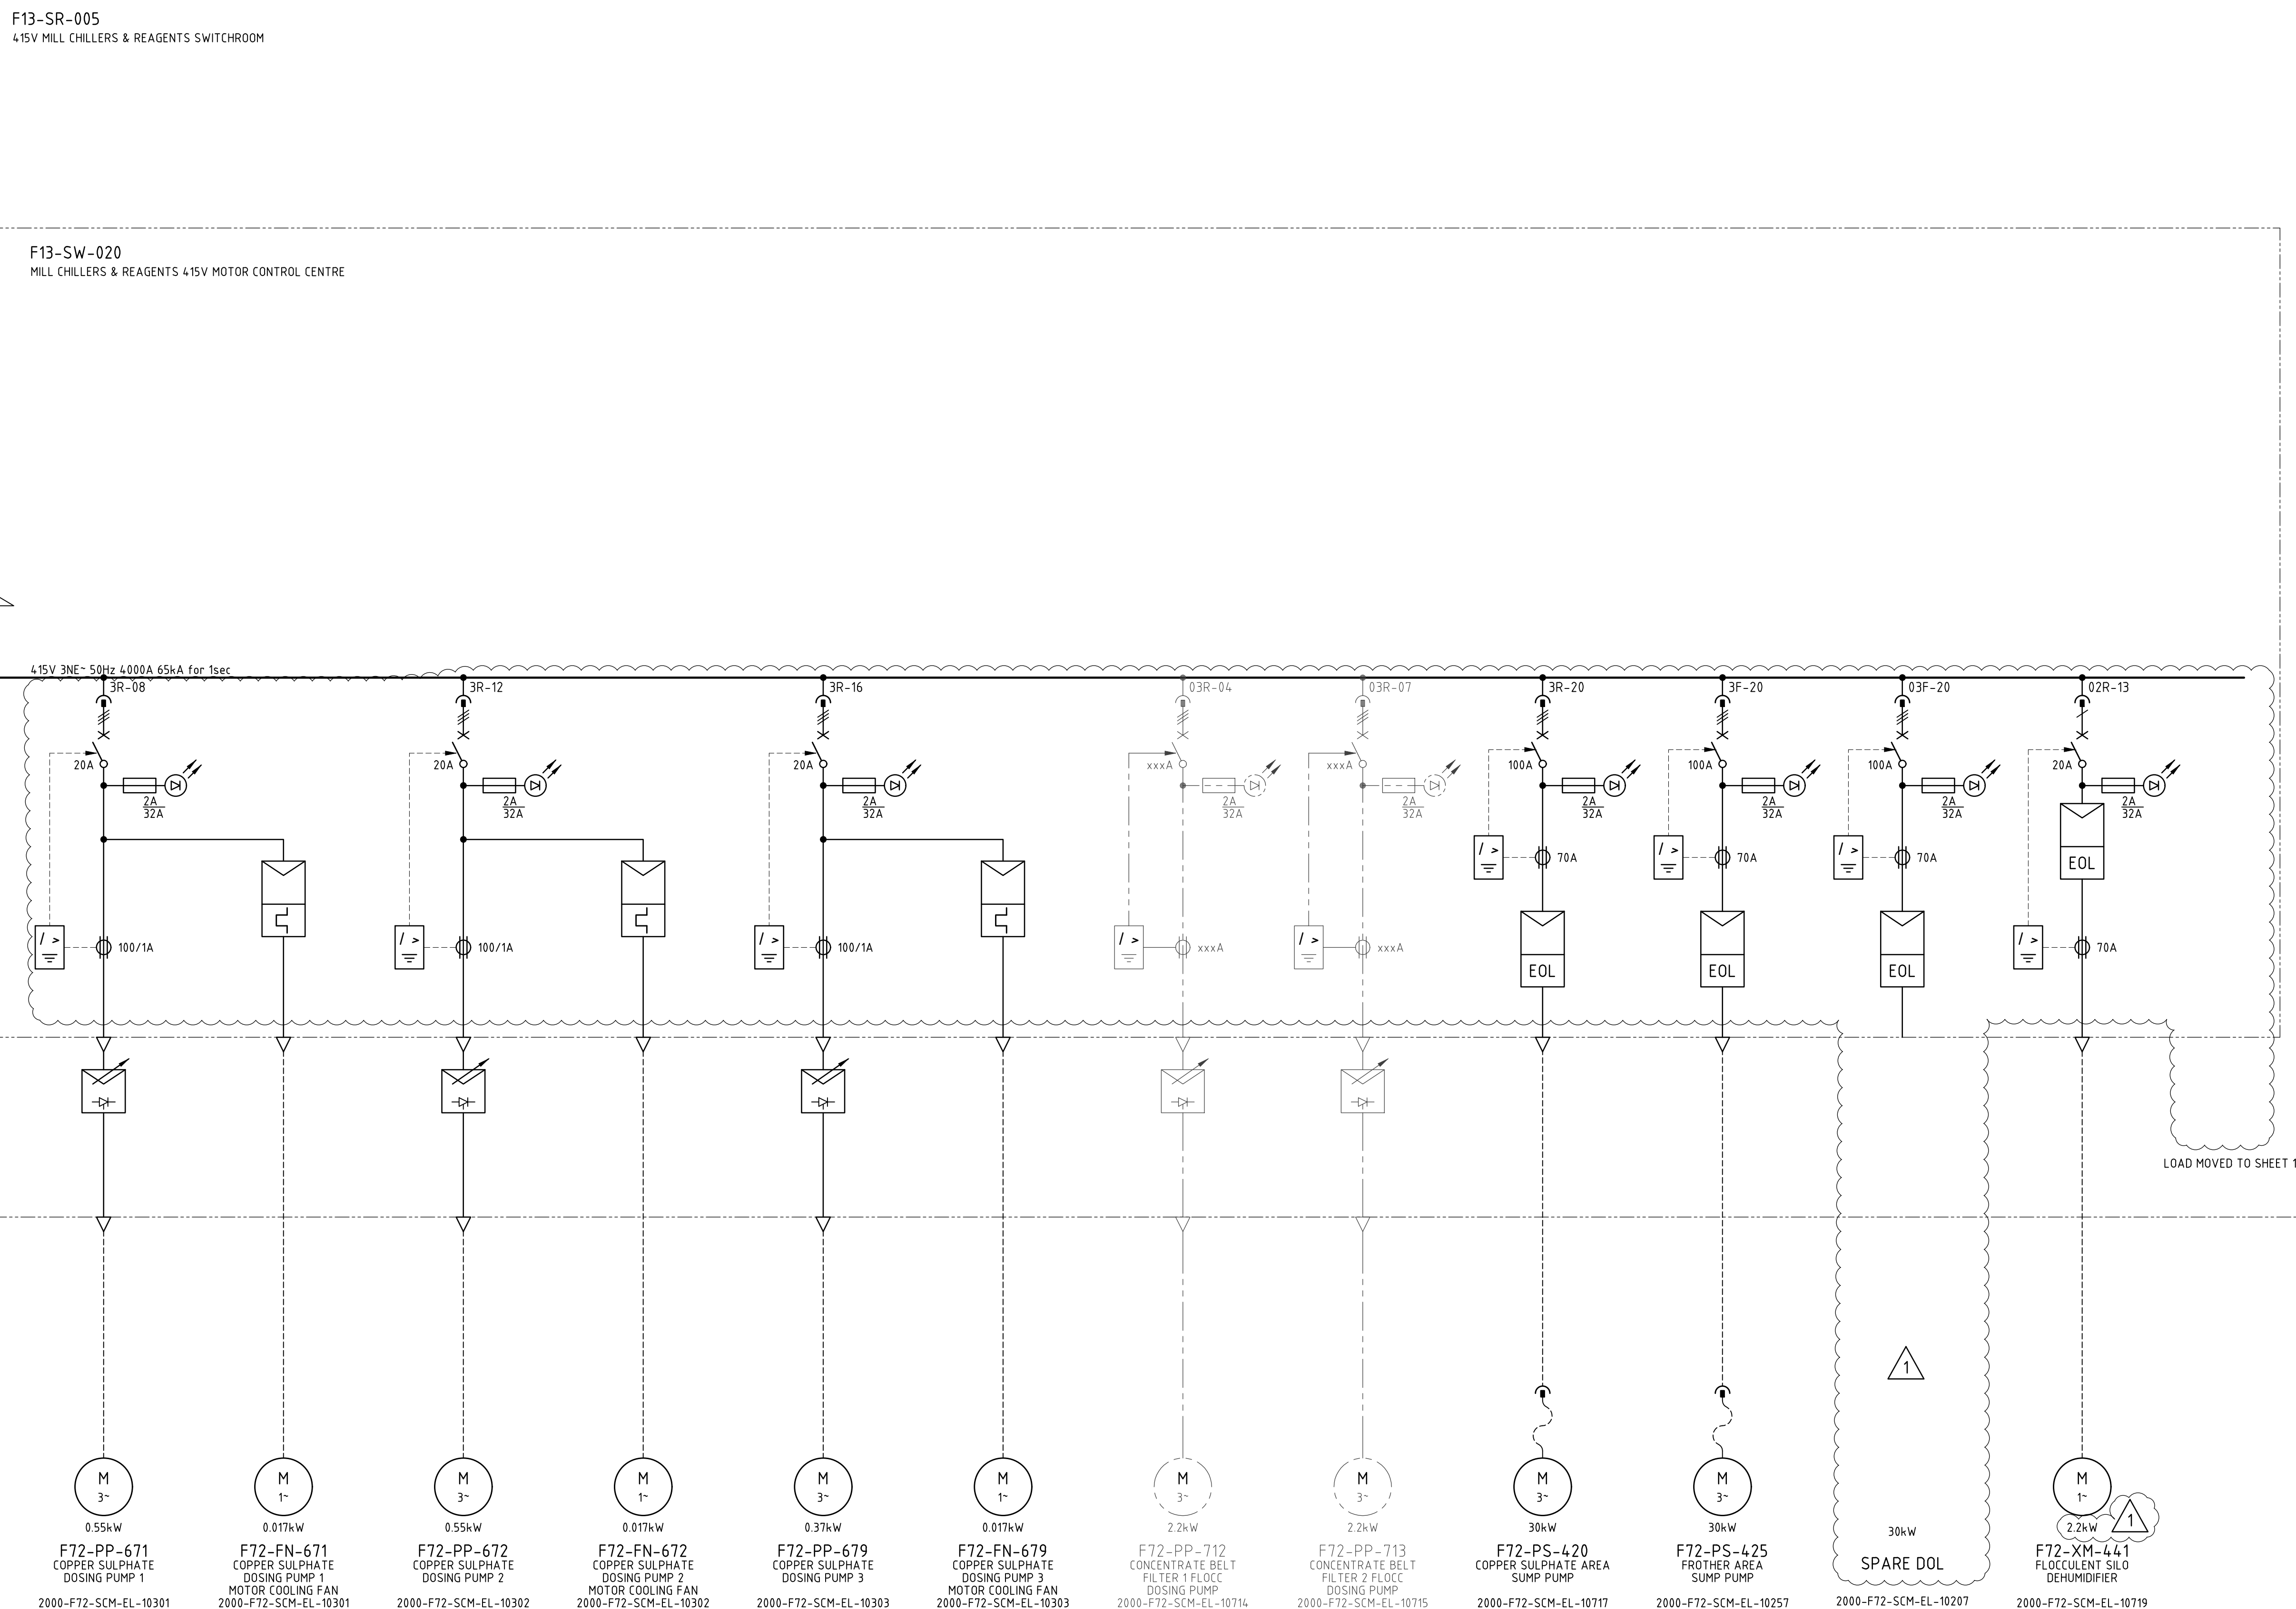

CONTINUED ON SHT 3
0000-F13-SLD-EL-10703

F13-SR-005
415V MILL CHILLERS & REAGENTS SWITCHROOM

F13-SW-020
MILL CHILLERS & REAGENTS 415V MOTOR CONTROL CENTRE

NOTES

1. REFER TO SHEET 1.

LEGEND

1. REFER TO SHEET 1

 NORTHERN STAR LOGISTICS	
Approved	☒
Approved as Noted	☐
Not Approved	☐
For Information Only	☐
Signed	Date 24.06.2025
ACCEPTANCE DOES NOT RELIEVE THE SUPPLIER / CONTRACTOR OF ITS RESPONSIBILITY OR LIABILITIES UNDER THE PURCHASE ORDER / CONTRACT	

[illegible]