
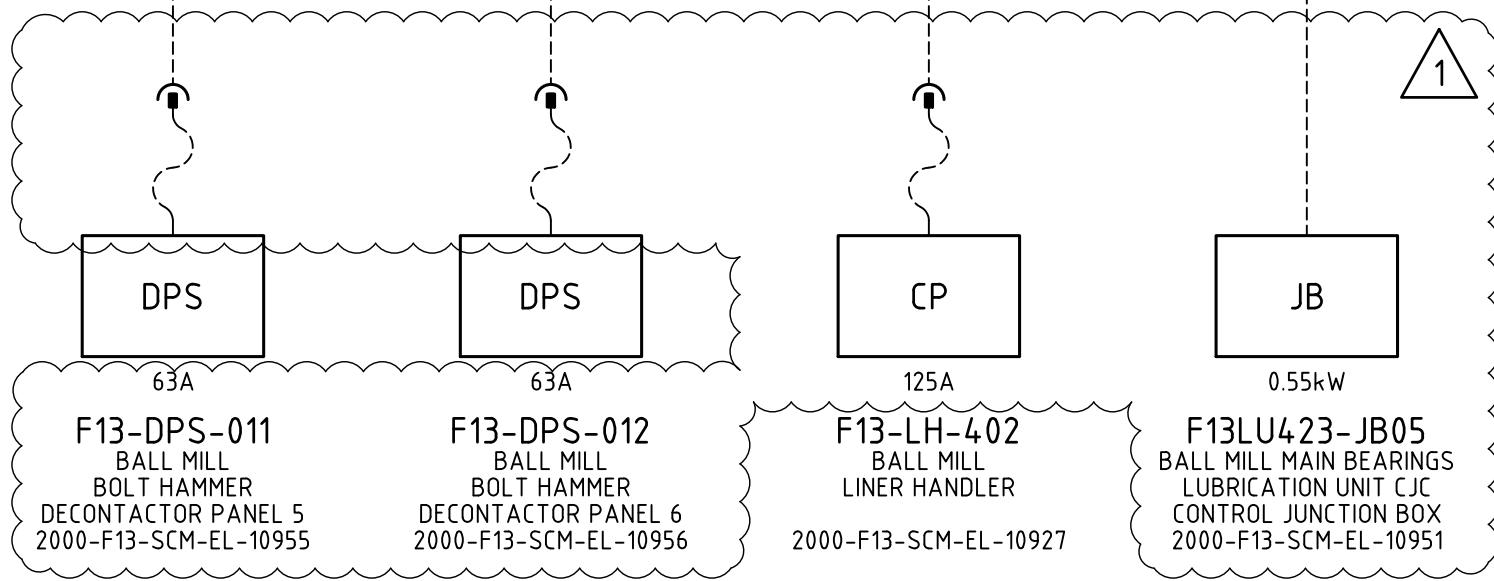


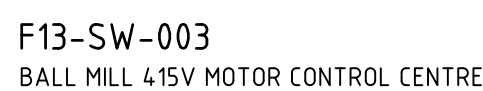

PRIMERO
primero.com.au | DESIGN | CONSTRUCT | OPERATE
PRIMERO PROJECT NUMBER: 23517

INFORMATION AND REPRESENTATIONS ON THIS DRAWING ARE THE INTELLECTUAL PROPERTY OF PRIMERO UNLESS SPECIFICALLY IDENTIFIED OTHERWISE. ALL RIGHTS INCLUDING USE RESERVED.

PROJECT: NORTHERN STAR RESOURCES LTD KCGM GROWTH PROJECT			
TITLE: MILLING & CLASSIFICATION - BALL MILL F13-SW-003 415V MCC SINGLE LINE DIAGRAM SHEET 3			
SHEET A1	SCALE NONE	DRG No. 2000-F13-SLD-EL-10903	REVISION 1

1. REFER TO SHEET 1.

1. REFER TO SHEET 1.