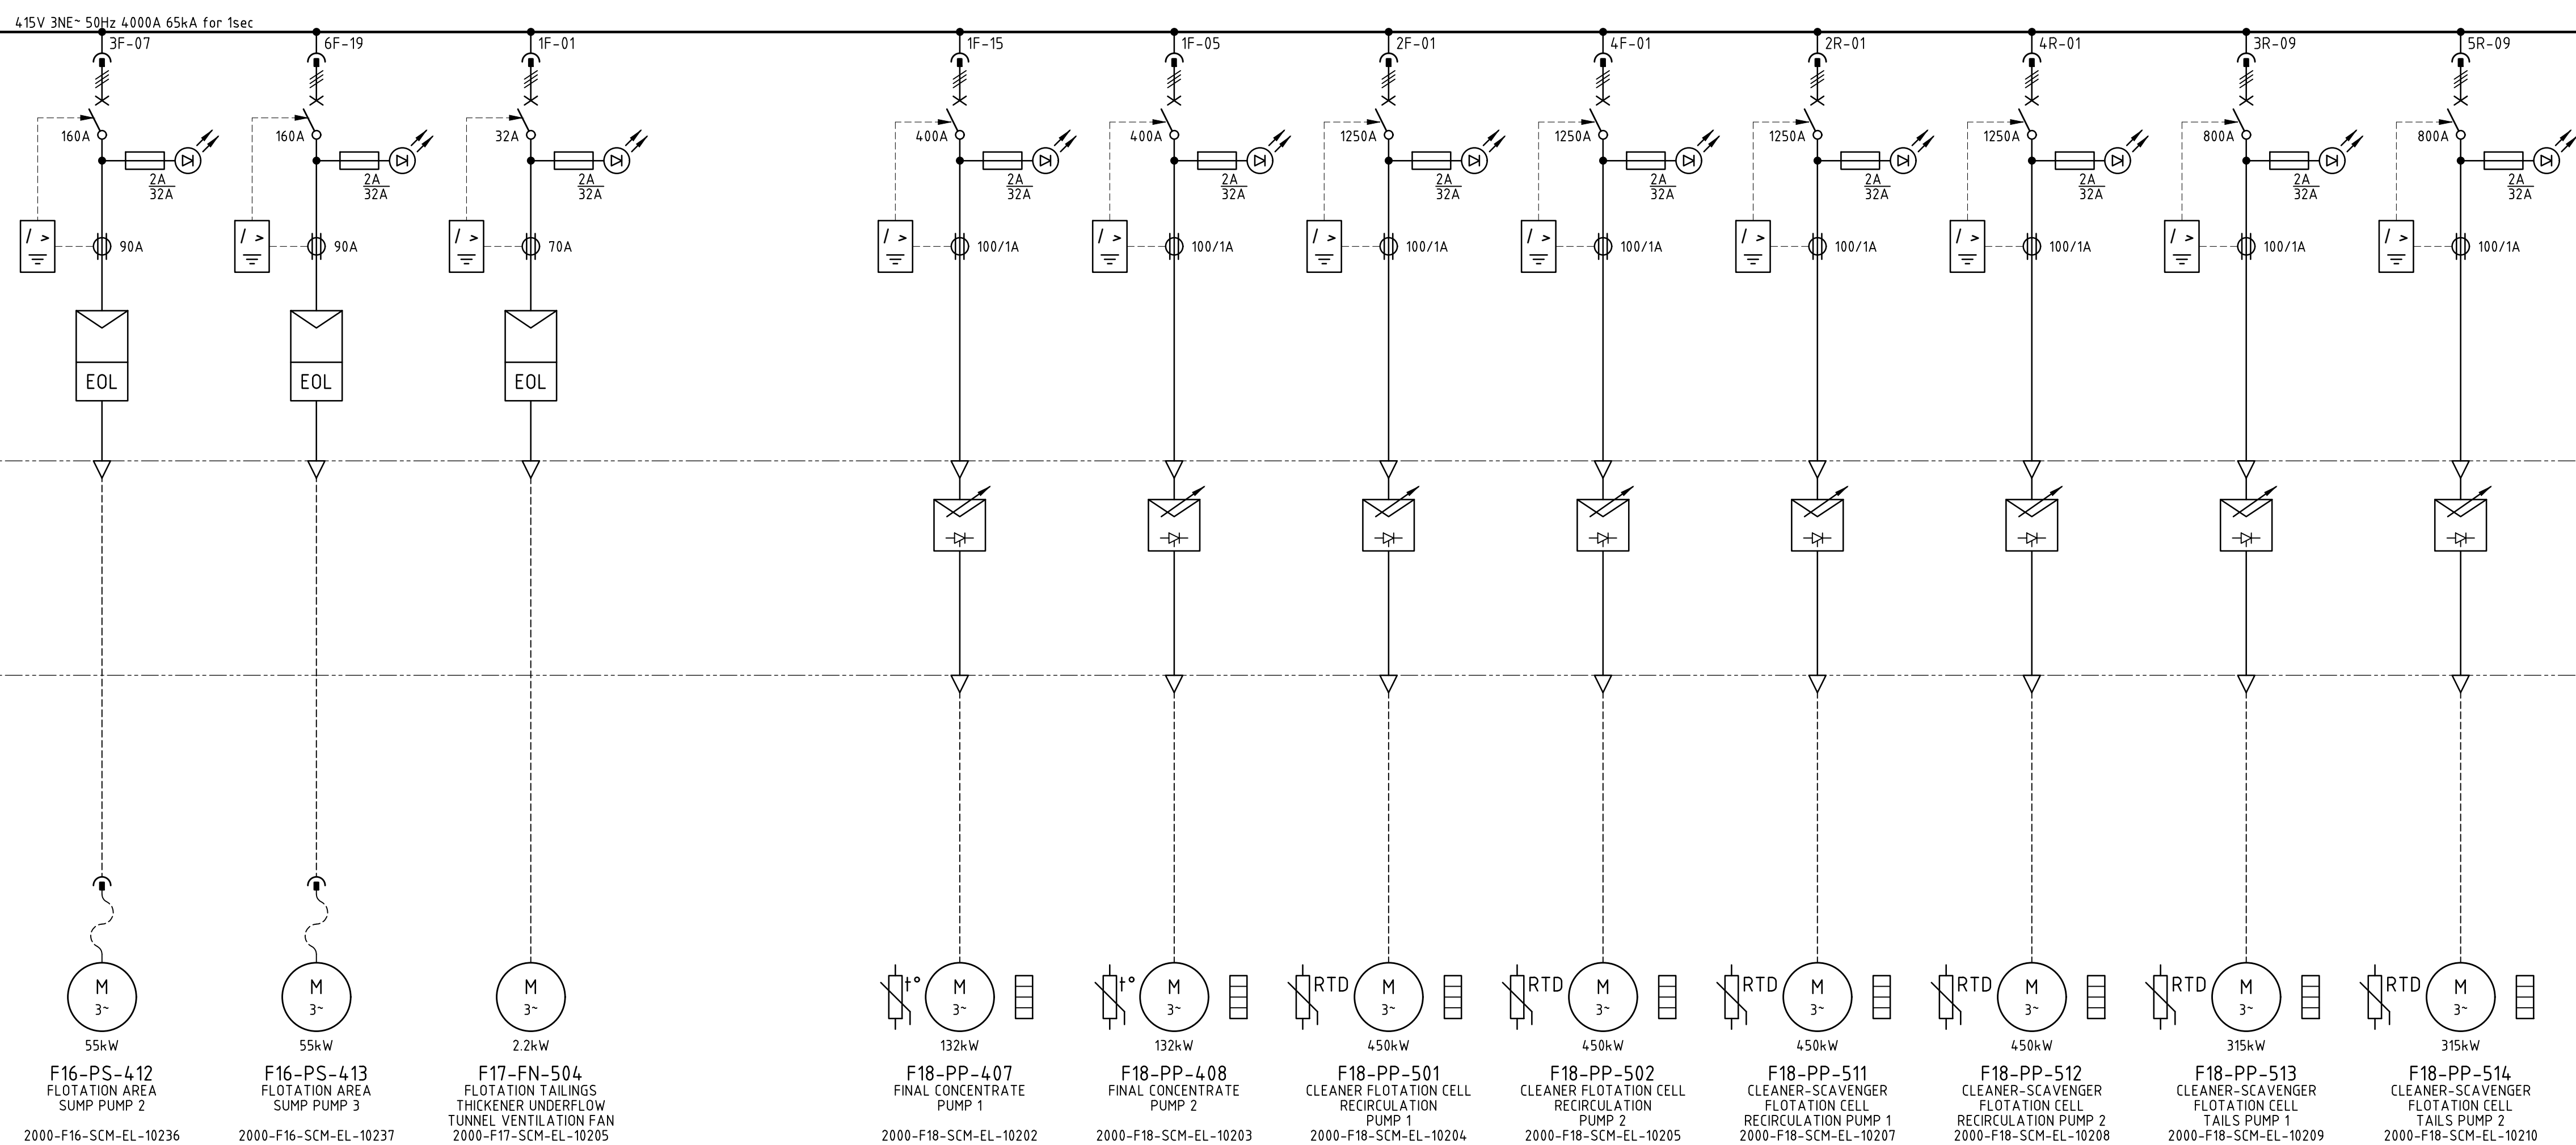


CONTINUED ON SHT 5
2000-F16-SLD-EL-10205

[illegible]

PRIMERO
primero.com.au | DESIGN | CONSTRUCT | OPERATE
PRIMERO PROJECT NUMBER: 23517

INFORMATION AND REPRESENTATIONS ON THIS DRAWING ARE THE INTELLECTUAL PROPERTY OF
PRIMERO UNLESS SPECIFICALLY IDENTIFIED OTHERWISE. ALL RIGHTS INCLUDING USE RESERVED

PROJECT: NORTHERN STAR RESOURCES LTD KCGM GROWTH PROJECT			
TITLE: ROUGHER AND SCAVENGER FLOTATION F16-SW-004 4.15V MCC SINGLE LINE DIAGRAM SHEET 4			
SHEET A1	SCALE NONE	DRG No. 2000-F16-SLD-EL-10204	REVISION 2

NOTES

1. REFER TO SHEET 1.

LEGEND

1. REFER TO SHEET 1.