


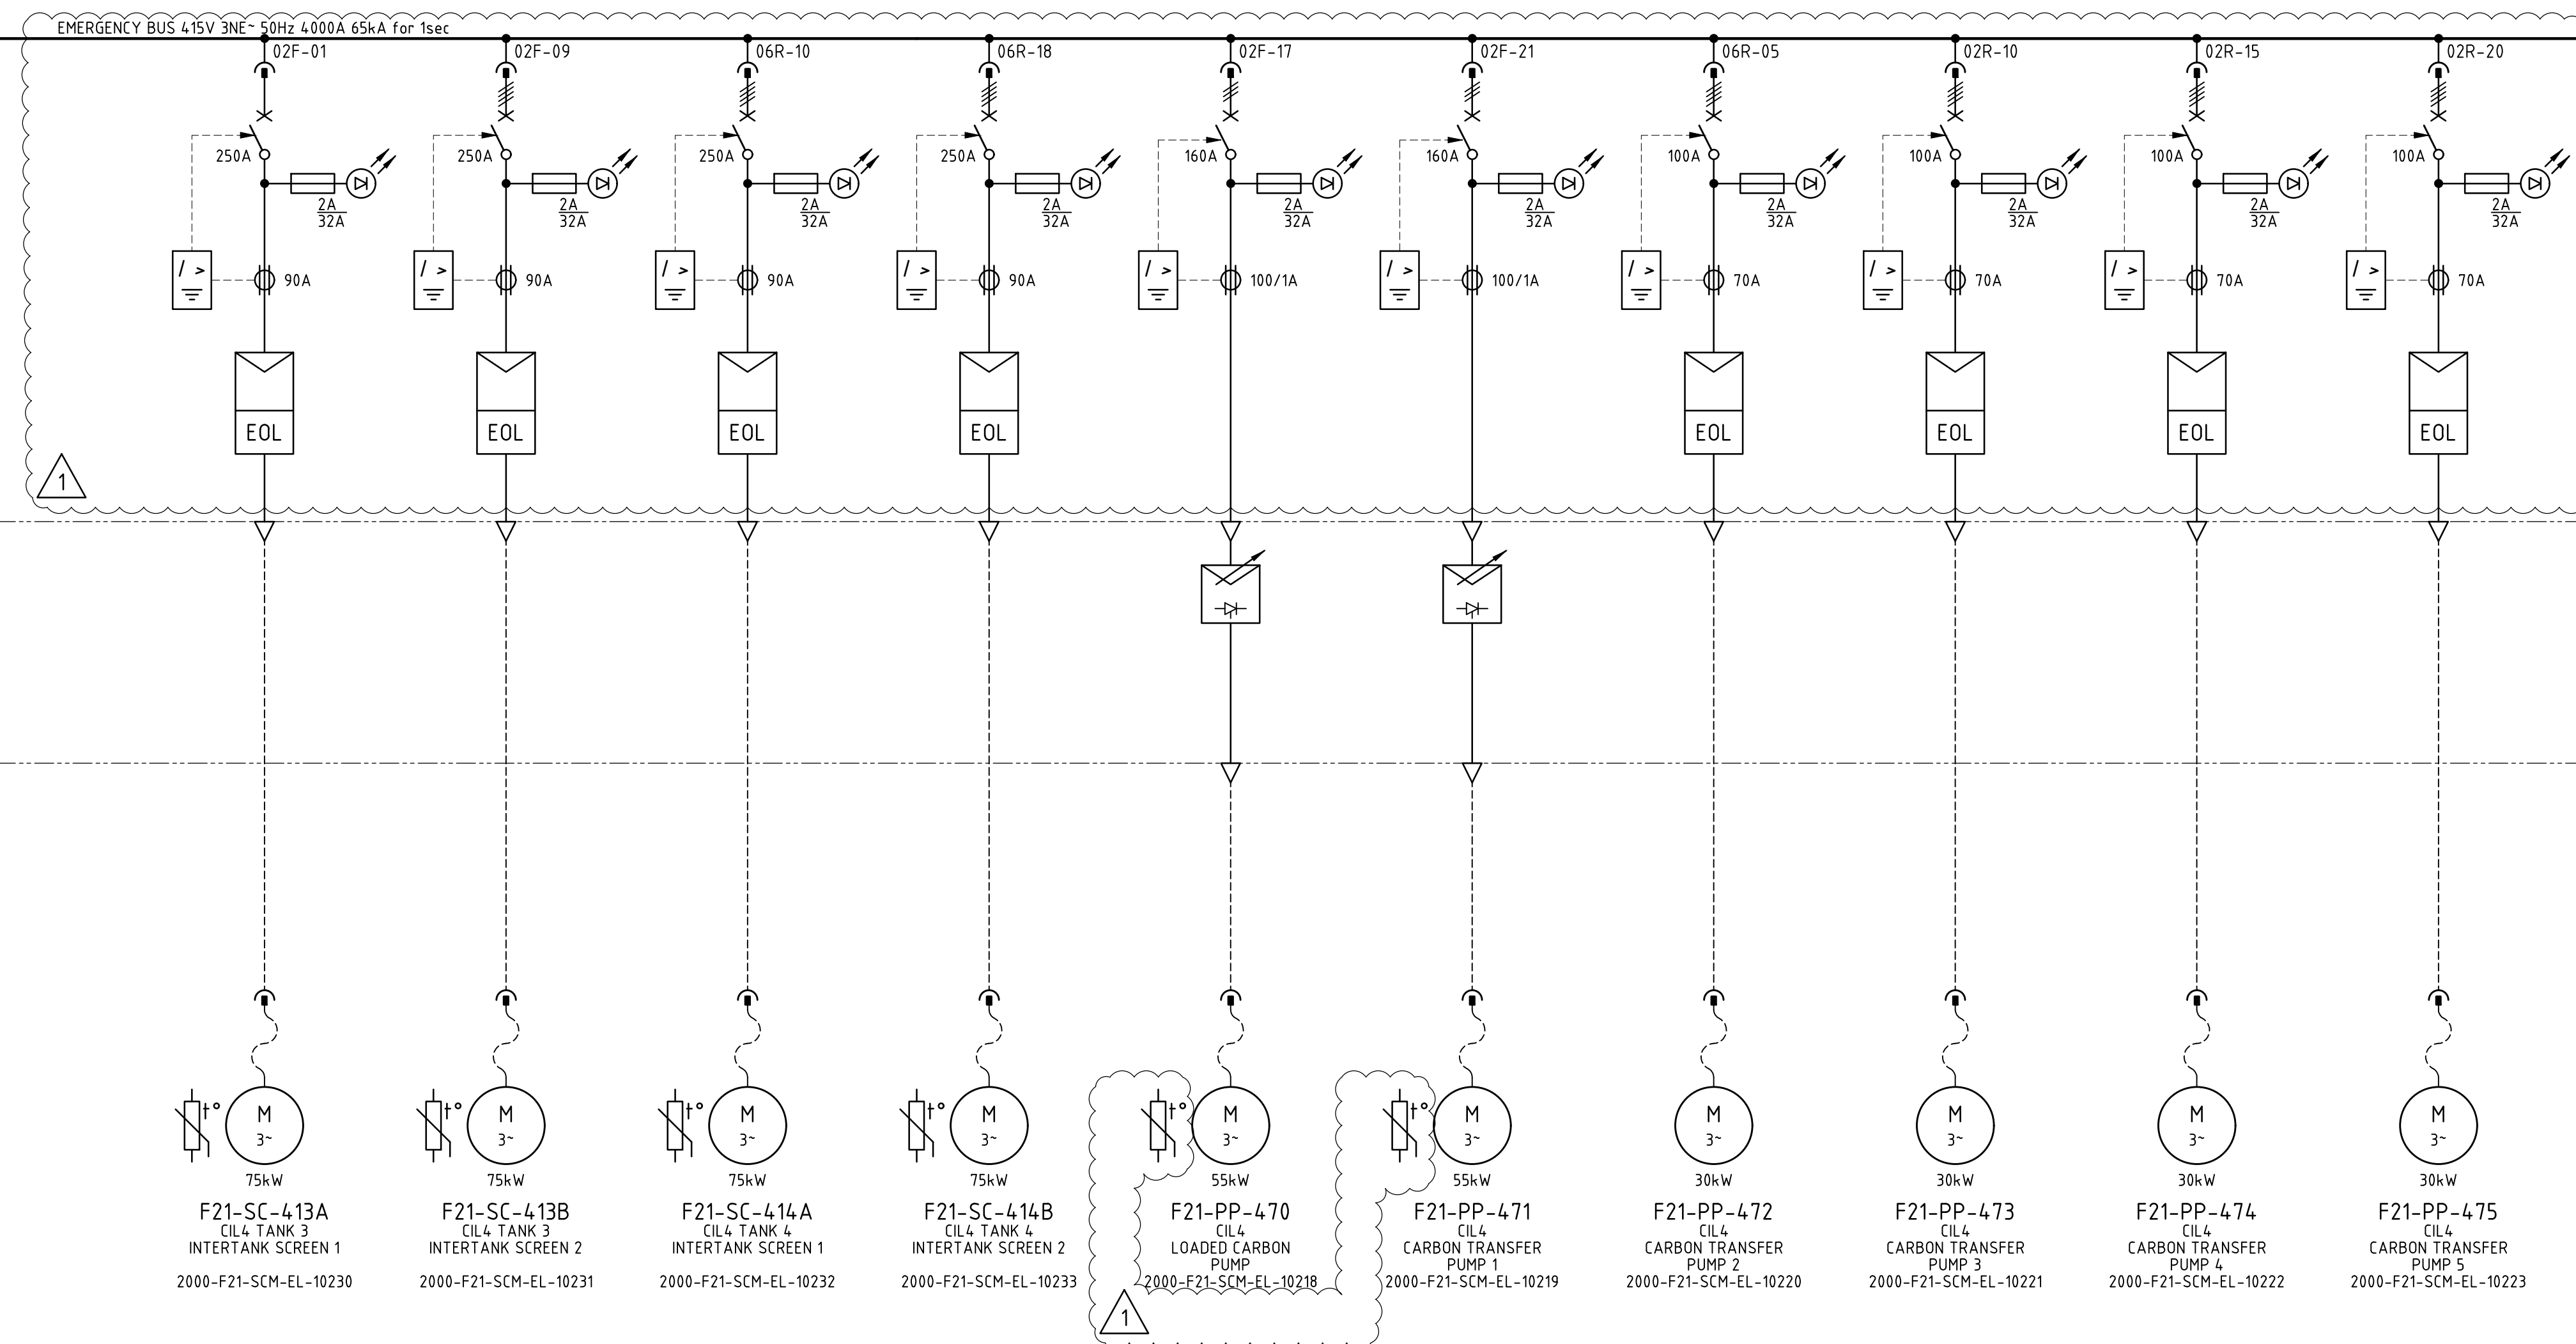

CONTINUED ON SHT 1
2000-F21-SLD-EL-10201

CONTINUED ON SHT 3
000-F21-SLD-EL-10203

[illegible]

PRIMERO
primero.com.au | DESIGN | CONSTRUCT | OPERATE
PRIMERO PROJECT NUMBER: 23517

INFORMATION AND REPRESENTATIONS ON THIS DRAWING ARE THE INTELLECTUAL PROPERTY OF PRIMERO UNLESS SPECIFICALLY IDENTIFIED OTHERWISE. ALL RIGHTS INCLUDING USE RESERVED

TITLE:	FLOTATION TAILINGS CIL4 F21-SW-006 415V MCC SINGLE LINE DIAGRAM SHEET 2
--------	---


REVISION
1

NOTES

1. REFER TO SHEET 1.

LEGEND

1. REFER TO SHEET 1.

  NORTHERN STAR	
Approved	☒
Approved as Noted	☐
Not Approved	☐
For Information Only	☐
Signed	Date
	19/11/2025
*ACCEPTANCE DOES NOT RELIEVE THE SUPPLIER / CONTRACTOR OF ITS RESPONSIBILITY OR LIABILITIES UNDER THE PURCHASE ORDER / CONTRACT	