


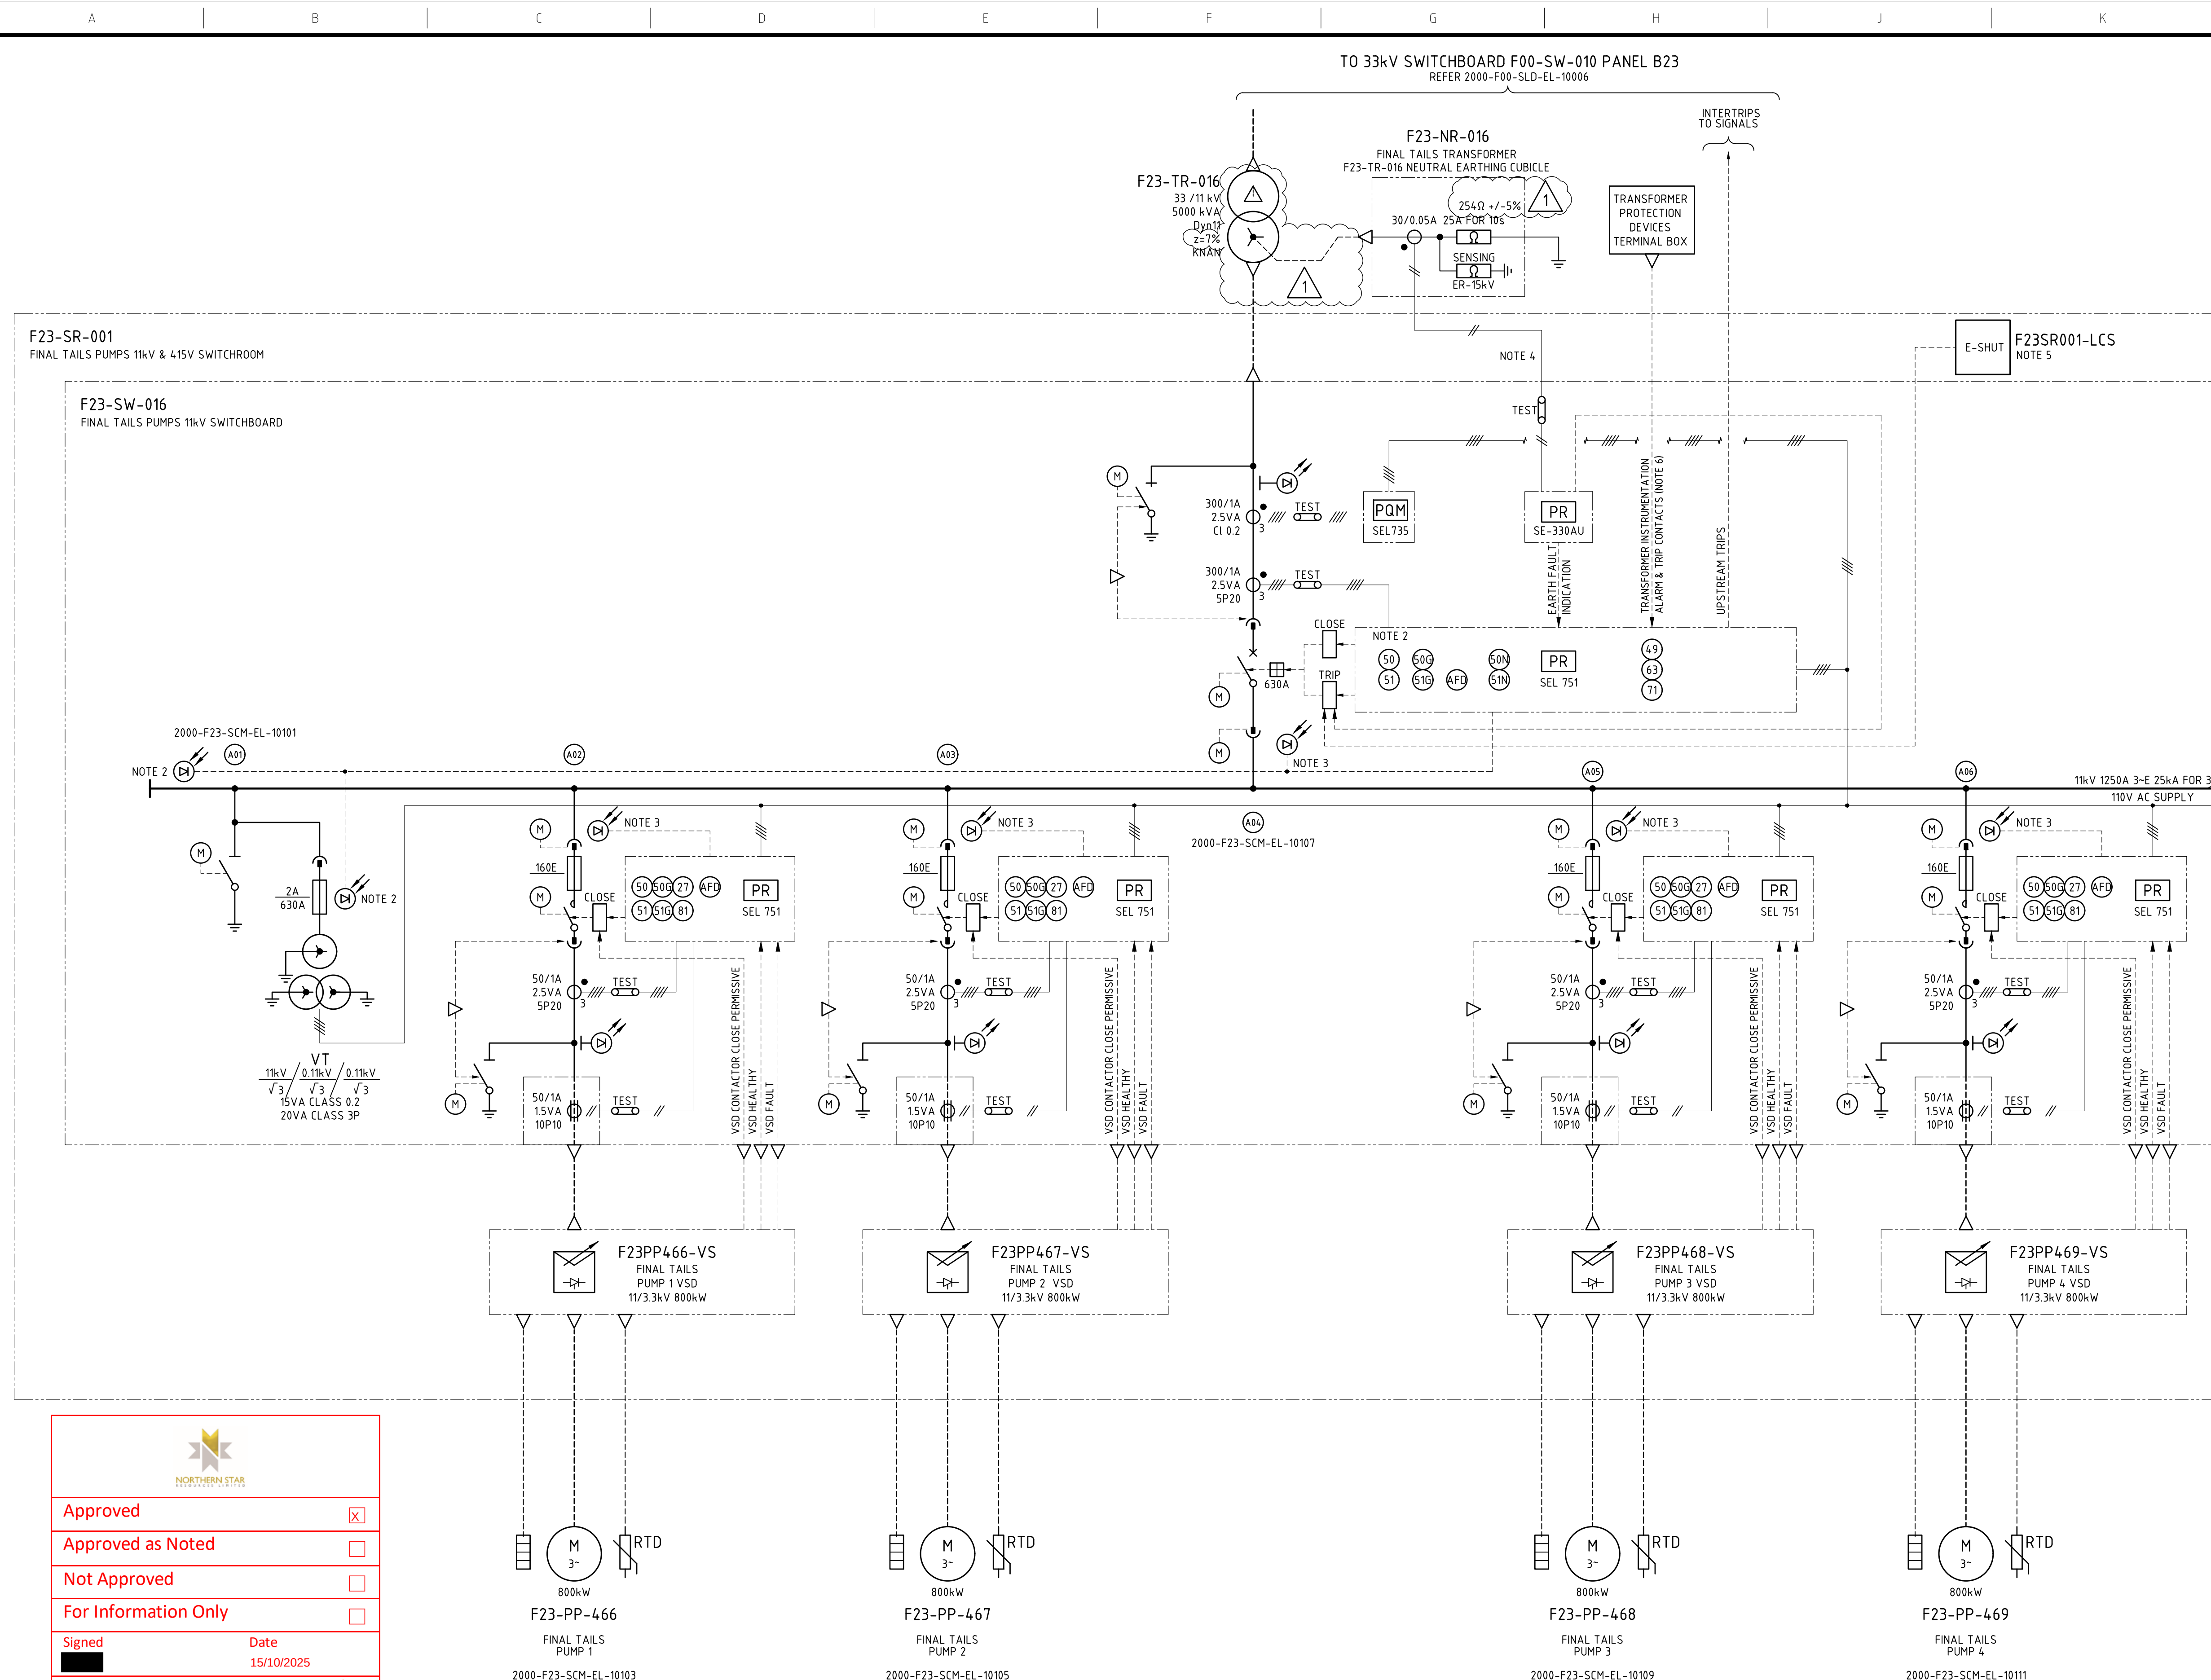

- ## NOTES
- | | |
|----|---|
| 1. | THE SWITCHBOARD SHALL BE EXTENSIBLE ONE END FOR FUTURE EXPANSION AND SUPPLIED WITH ONE SPARE TIE AS SHOWN. |
| 2. | ARC FLASH IN INCOMER CIRCUIT BREAKER COMPARTMENT IS NOT CURRENT SUPERVISED.
TRIPPING OF BUS AND DOWNSTREAM CB/FC COMPARTMENTS IS CURRENT SUPERVISED. |
| 3. | ARC FLASH POINT DETECTORS SHALL BE PLACED IN THE CABLE JUNE, CIRCUIT BREAKER CHAMBER OR FUSE CONTACTOR CHAMBER AND THE BUSBAR CHAMBER. THE DETECTORS SHALL BE CONNECTED DIRECTLY TO THE PROTECTION RELAY IN EACH PANEL. |
| 4. | ONE OFF 30/0.05A PROTECTION CT SHALL BE INSTALLED IN THE NEAR CUBICLE AND CONNECTED TO THE INCOMER PROTECTION RELAY TO MONITOR FOR EARTH FAULT DETECTION . |
| 5. | SWITCHROOM EMERGENCY SHUTDOWN (E-SHUT) PUSHBUTTON IS HARDWIRED DIRECT TO THE SHUNT TRIP OF THE INCOMER CIRCUIT BREAKER AND UPSTREAM 33kV FEEDER. |
| 6. | 33/11kV TRANSFORMER INSTRUMENTATION TRIP CONTACTS SHALL BE HARDWIRED TO THE 11kV SWITCHBOARD INCOMER PROTECTION RELAY WHICH SHALL INTERTRIP THE UPSTREAM 33kV FEEDER. |
| 7. | UPSTREAM 11kV FEEDER SHALL BE TRIPPED ON THE EARTH & ARC FAULT DETECTION OF THE DOWNSTREAM INCOMER ACB. |

LEGEND

- | | |
|--|--|
| | INCOMER / FEEDER PROTECTION RELAY |
| | POWER QUALITY METER |
| | ARC FLASH SENSOR (POINT TYPE)
NOTES 2 & 3 |
| | CAPACITIVE RESONANCE INDICATION |
| | MECHANICAL INTERLOCK DEVICE |
| | SWITCHROOM EMERGENCY SHUTDOWN |
| | MOTOR OPERATOR |
| | UNDER VOLTAGE |
| | INSTANTANEOUS OVER-CURRENT |
| | INSTANTANEOUS EARTH/NEUTRAL OVERCURRENT |
| | TIMED OVER-CURRENT |
| | TIMED EARTH/NEUTRAL OVERCURRENT |
| | OVER VOLTAGE |
| | EARTH FAULT |
| | TRANSFORMER TEMPERATURE |
| | TRANSFORMER PRESSURE / BUCCHOLZ |
| | TRANSFORMER LIQUID / GAS LEVEL |
| | FREQUENCY |
| | ARC FLASH DETECTION |

 NORTHERN STAR SERVICES LTD	
Approved	☒
Approved as Noted	☐
Not Approved	☐
For Information Only	☐
Signed 	Date 15/10/2025
ACCEPTANCE DOES NOT RELIEVE THE SUPPLIER / CONTRACTOR OF ITS RESPONSIBILITY OR LIABILITIES UNDER THE PURCHASE ORDER / CONTRACT	

--	--	