


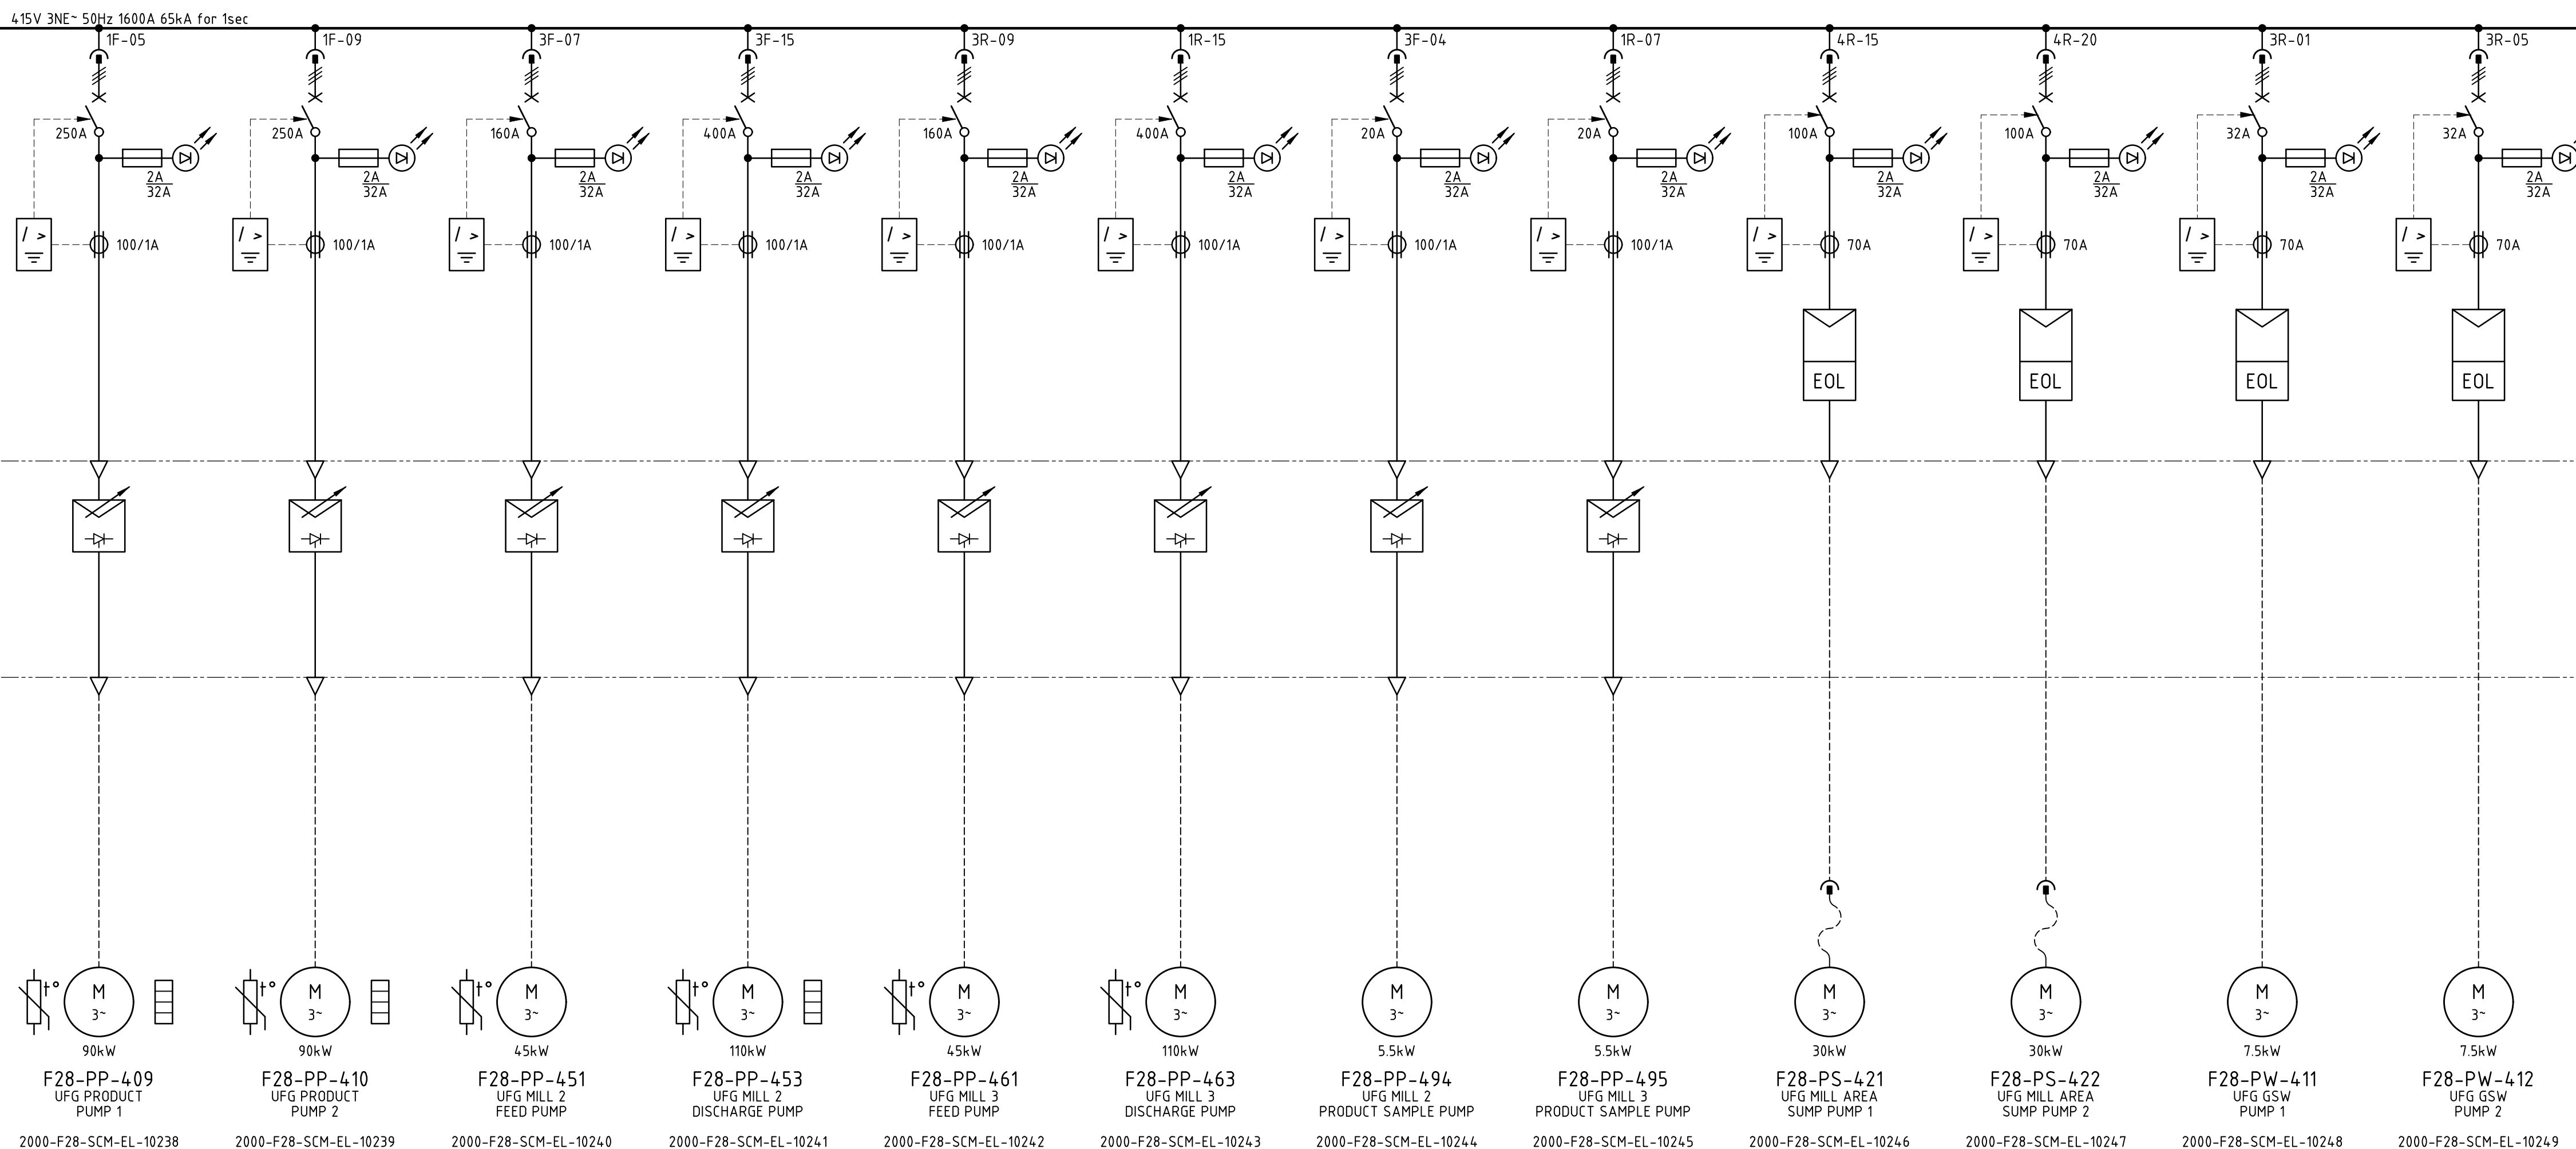

CONTINUED ON SHT 2
2000-F28-SLD-EL-10202

CONTINUED ON SHT 4

[illegible]

PRIMERO
primero.com.au | DESIGN | CONSTRUCT | OPERATE

PRIMERO PROJECT NUMBER: 23517

INFORMATION AND REPRESENTATIONS ON THIS DRAWING ARE THE INTELLECTUAL PROPERTY OF
PRIMERO UNLESS SPECIFICALLY IDENTIFIED OTHERWISE. ALL RIGHTS INCLUDING USE RESERVED

PROJECT:	NORTHERN STAR RESOURCES LTD KCGM GROWTH PROJECT
TITLE:	ULTRA FINE GRINDING 2/3 F28-SW-009 415V MCC SINGLE LINE DIAGRAM SHEET 3

SHEET	SCALE	DRG No.	REVISION
A1	NONE	2000-F28-SLD-EL-10203	2

NOTES

1. REFER TO SHEET 1

LEGEND

1. REFER TO SHEET 1