


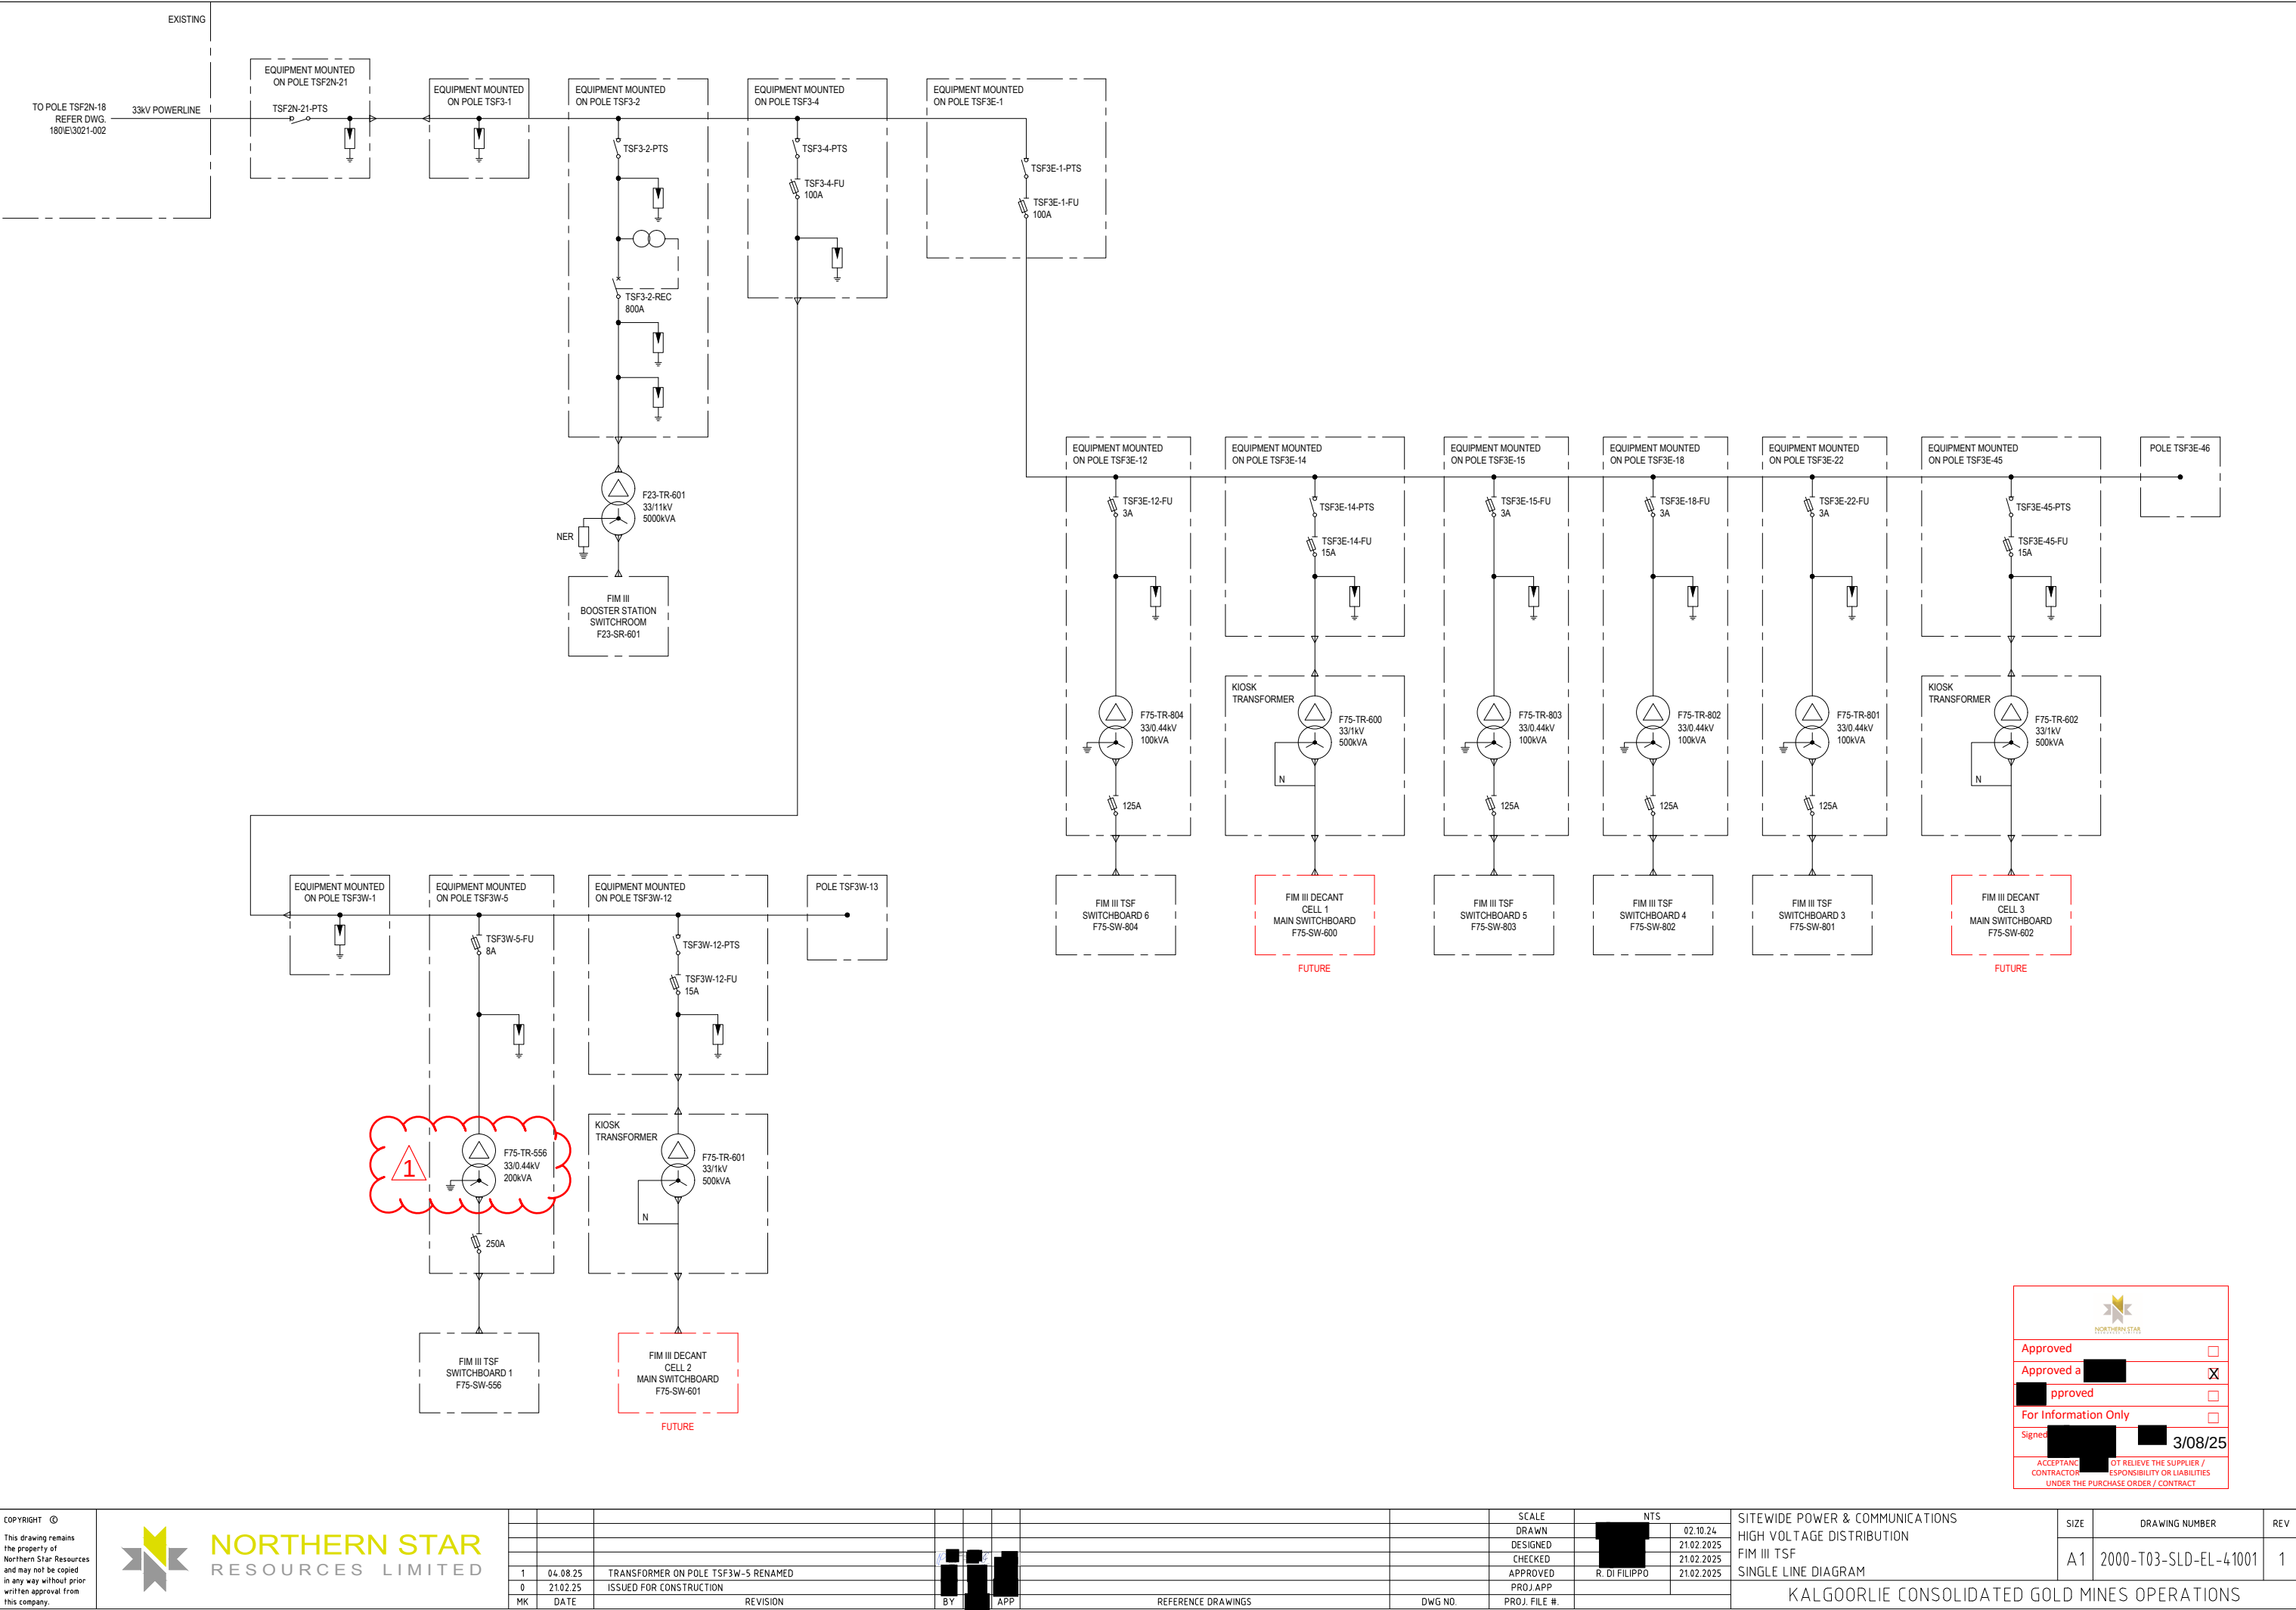

	
Approved	☐
Approved a	☒
pproved	☐
For Information Only	☐
Signed	3/08/25
ACCEPTANCE OF THE CONTRACTOR DOES NOT RELIEVE THE SUPPLIER / CONTRACTOR OF RESPONSIBILITY OR LIABILITIES UNDER THE PURCHASE ORDER / CONTRACT	

COPYRIGHT © This drawing remains the property of Northern Star Resources and may not be copied in any way without prior written approval from this company.			 NORTHERN STAR RESOURCES LIMITED			<table><tr><td>1</td><td>04.08.25</td><td>TRANSFORMER ON POLE TSF3W-5 RENAMED</td></tr><tr><td>0</td><td>21.02.25</td><td>ISSUED FOR CONSTRUCTION</td></tr><tr><td>MK</td><td>DATE</td><td>REVISION</td></tr></table>			1	04.08.25	TRANSFORMER ON POLE TSF3W-5 RENAMED	0	21.02.25	ISSUED FOR CONSTRUCTION	MK	DATE	REVISION	BY 	APP 	REFERENCE DRAWINGS	DWG NO.	SCALE DRAWN DESIGNED CHECKED APPROVED PROJ APP PROJ. FILE #	NTS  R. DI FILIPPO	SITEWIDE POWER & COMMUNICATIONS HIGH VOLTAGE DISTRIBUTION FIM III TSF SINGLE LINE DIAGRAM KALGOORLIE CONSOLIDATED GOLD MINES OPERATIONS	SIZE A1	DRAWING NUMBER 2000-T03-SLD-EL-41001	REV 1
1	04.08.25	TRANSFORMER ON POLE TSF3W-5 RENAMED																									
0	21.02.25	ISSUED FOR CONSTRUCTION																									
MK	DATE	REVISION																									