

D:\CAD PROJECTS\235 NORTHERN STAR RESOURCES LTD\23517 KCGM GROWTH PROJECT\03 DELIVERABLES\PR\PID\2000-F16-PID-PR-10001.DWG 03/10/25 8:45AM ANNE HOYNE

REVISION IN PROGRESS

REVISION IN PROGRESS

REVISION IN PROGRESS

REVISION IN PROGRESS

REVISION IN PROGRESS

REVISION IN PROGRESS

REVISION IN PROGRESS

REVISION IN PROGRESS

REVISION IN PROGRESS

REVISION IN PROGRESS

REVISION IN PROGRESS


REVISION IN PROGRESS

REVISION IN PROGRESS

REVISION IN PROGRESS

REVISION IN PROGRESS

REVISION IN PROGRESS

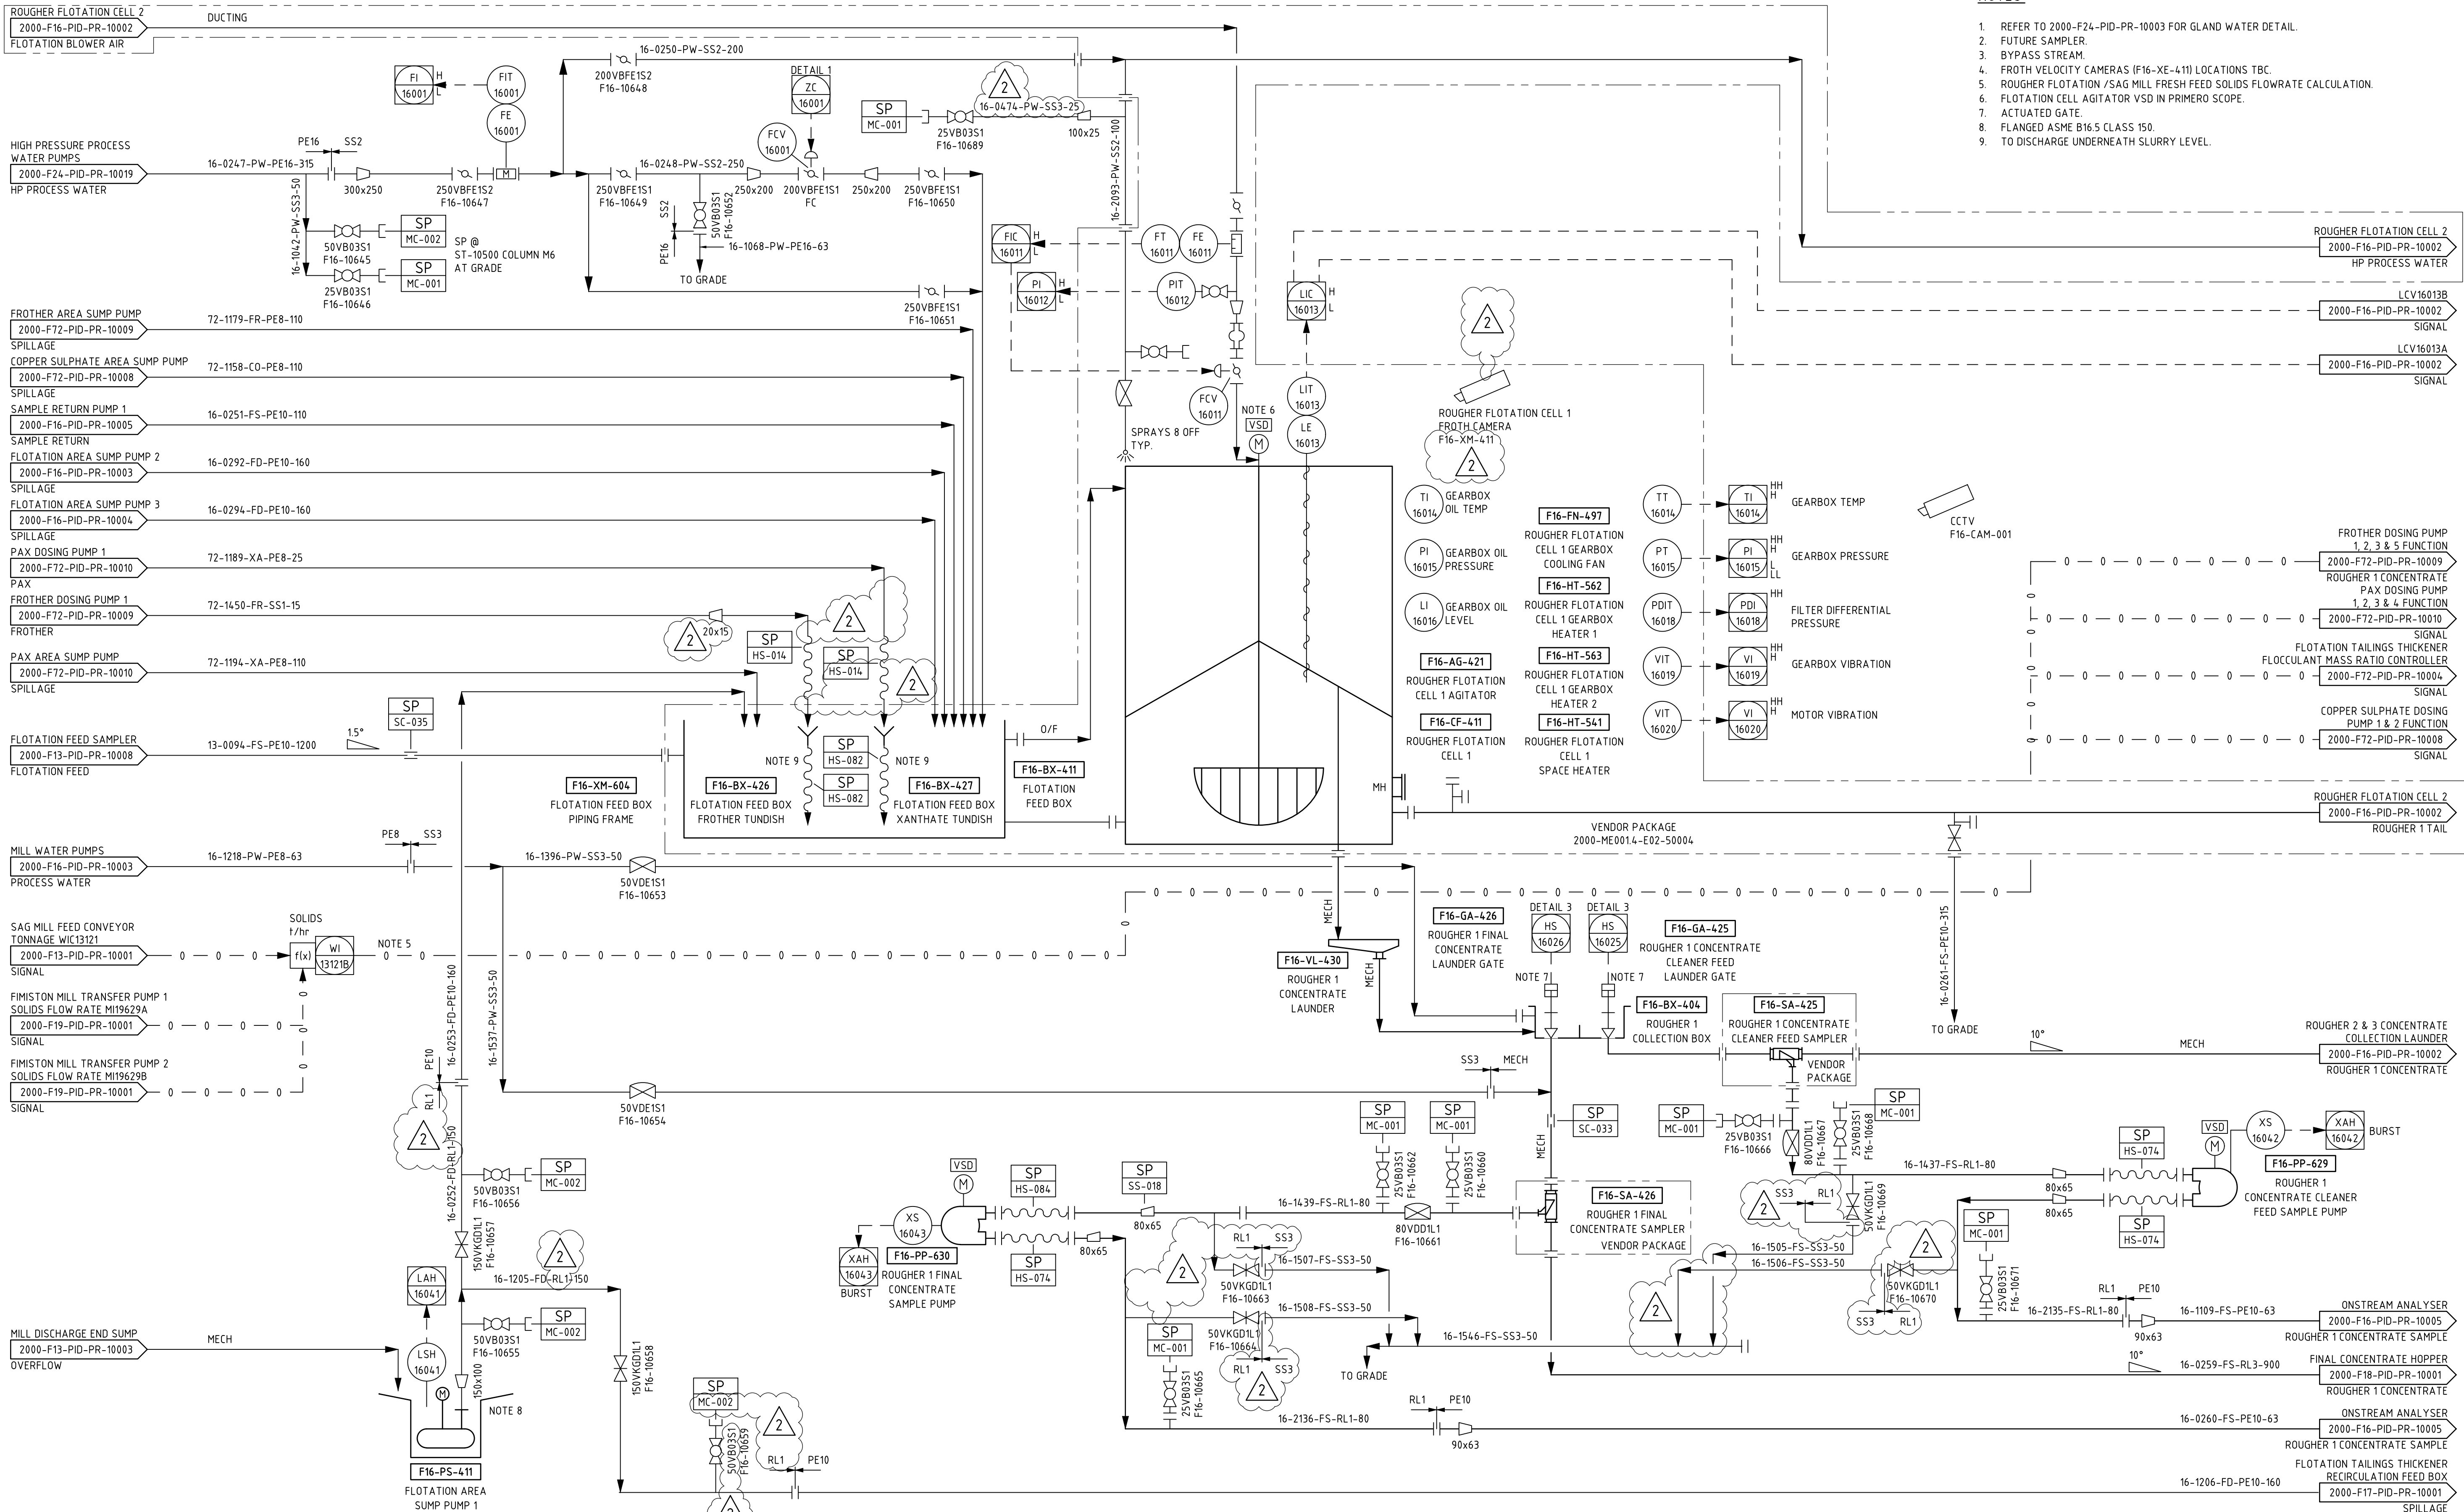

2000-F00-PID-PR-10007	LEGEND SHEET 7 - PIPING AND INSTRUMENTATION DIAGRAM				
2000-F00-PID-PR-10006	LEGEND SHEET 6 - PIPING AND INSTRUMENTATION DIAGRAM				
2000-F00-PID-PR-10005	LEGEND SHEET 5 - PIPING AND INSTRUMENTATION DIAGRAM				
2000-F00-PID-PR-10004	LEGEND SHEET 4 - PIPING AND INSTRUMENTATION DIAGRAM				
2000-F00-PID-PR-10003	LEGEND SHEET 3 - PIPING AND INSTRUMENTATION DIAGRAM				
2000-F00-PID-PR-10002	LEGEND SHEET 2 - PIPING AND INSTRUMENTATION DIAGRAM				
2000-F00-PID-PR-10001	LEGEND SHEET 1 - PIPING AND INSTRUMENTATION DIAGRAM				
DRG No.	REFERENCES	REV	DATE	DESCRIPTION	APPROVED
		2		GENERAL REVISIONS ADDED	
		1	19NOV24	RE-ISSUED FOR CONSTRUCTION	
		0	10SEP24	APPROVED FOR CONSTRUCTION	



INFORMATION AND REPRESENTATIONS ON THIS DRAWING ARE THE INTELLECTUAL PROPERTY OF PRIMERO UNLESS SPECIFICALLY IDENTIFIED OTHERWISE. ALL RIGHTS INCLUDING USE RESERVED



PRIMERO PROJECT NUMBER: 23517

PROJECT:	NORTHERN STAR RESOURCES LTD KCGM GROWTH PROJECT			
TITLE:	ROUGHER & SCAVENGER FLOTATION ROUGHER FLOTATION - SHEET 1 - STAGE 1 PIPING AND INSTRUMENTATION DIAGRAM			
SHEET	A1	SCALE	NTS	DRG No.
				2000-F16-PID-PR-10001
				REVISION
				2

REVISION IN PROGRESS

REVISION IN PROGRESS

REVISION IN PROGRESS

REVISION IN PROGRESS

REVISION IN PROGRESS

REVISION IN PROGRESS