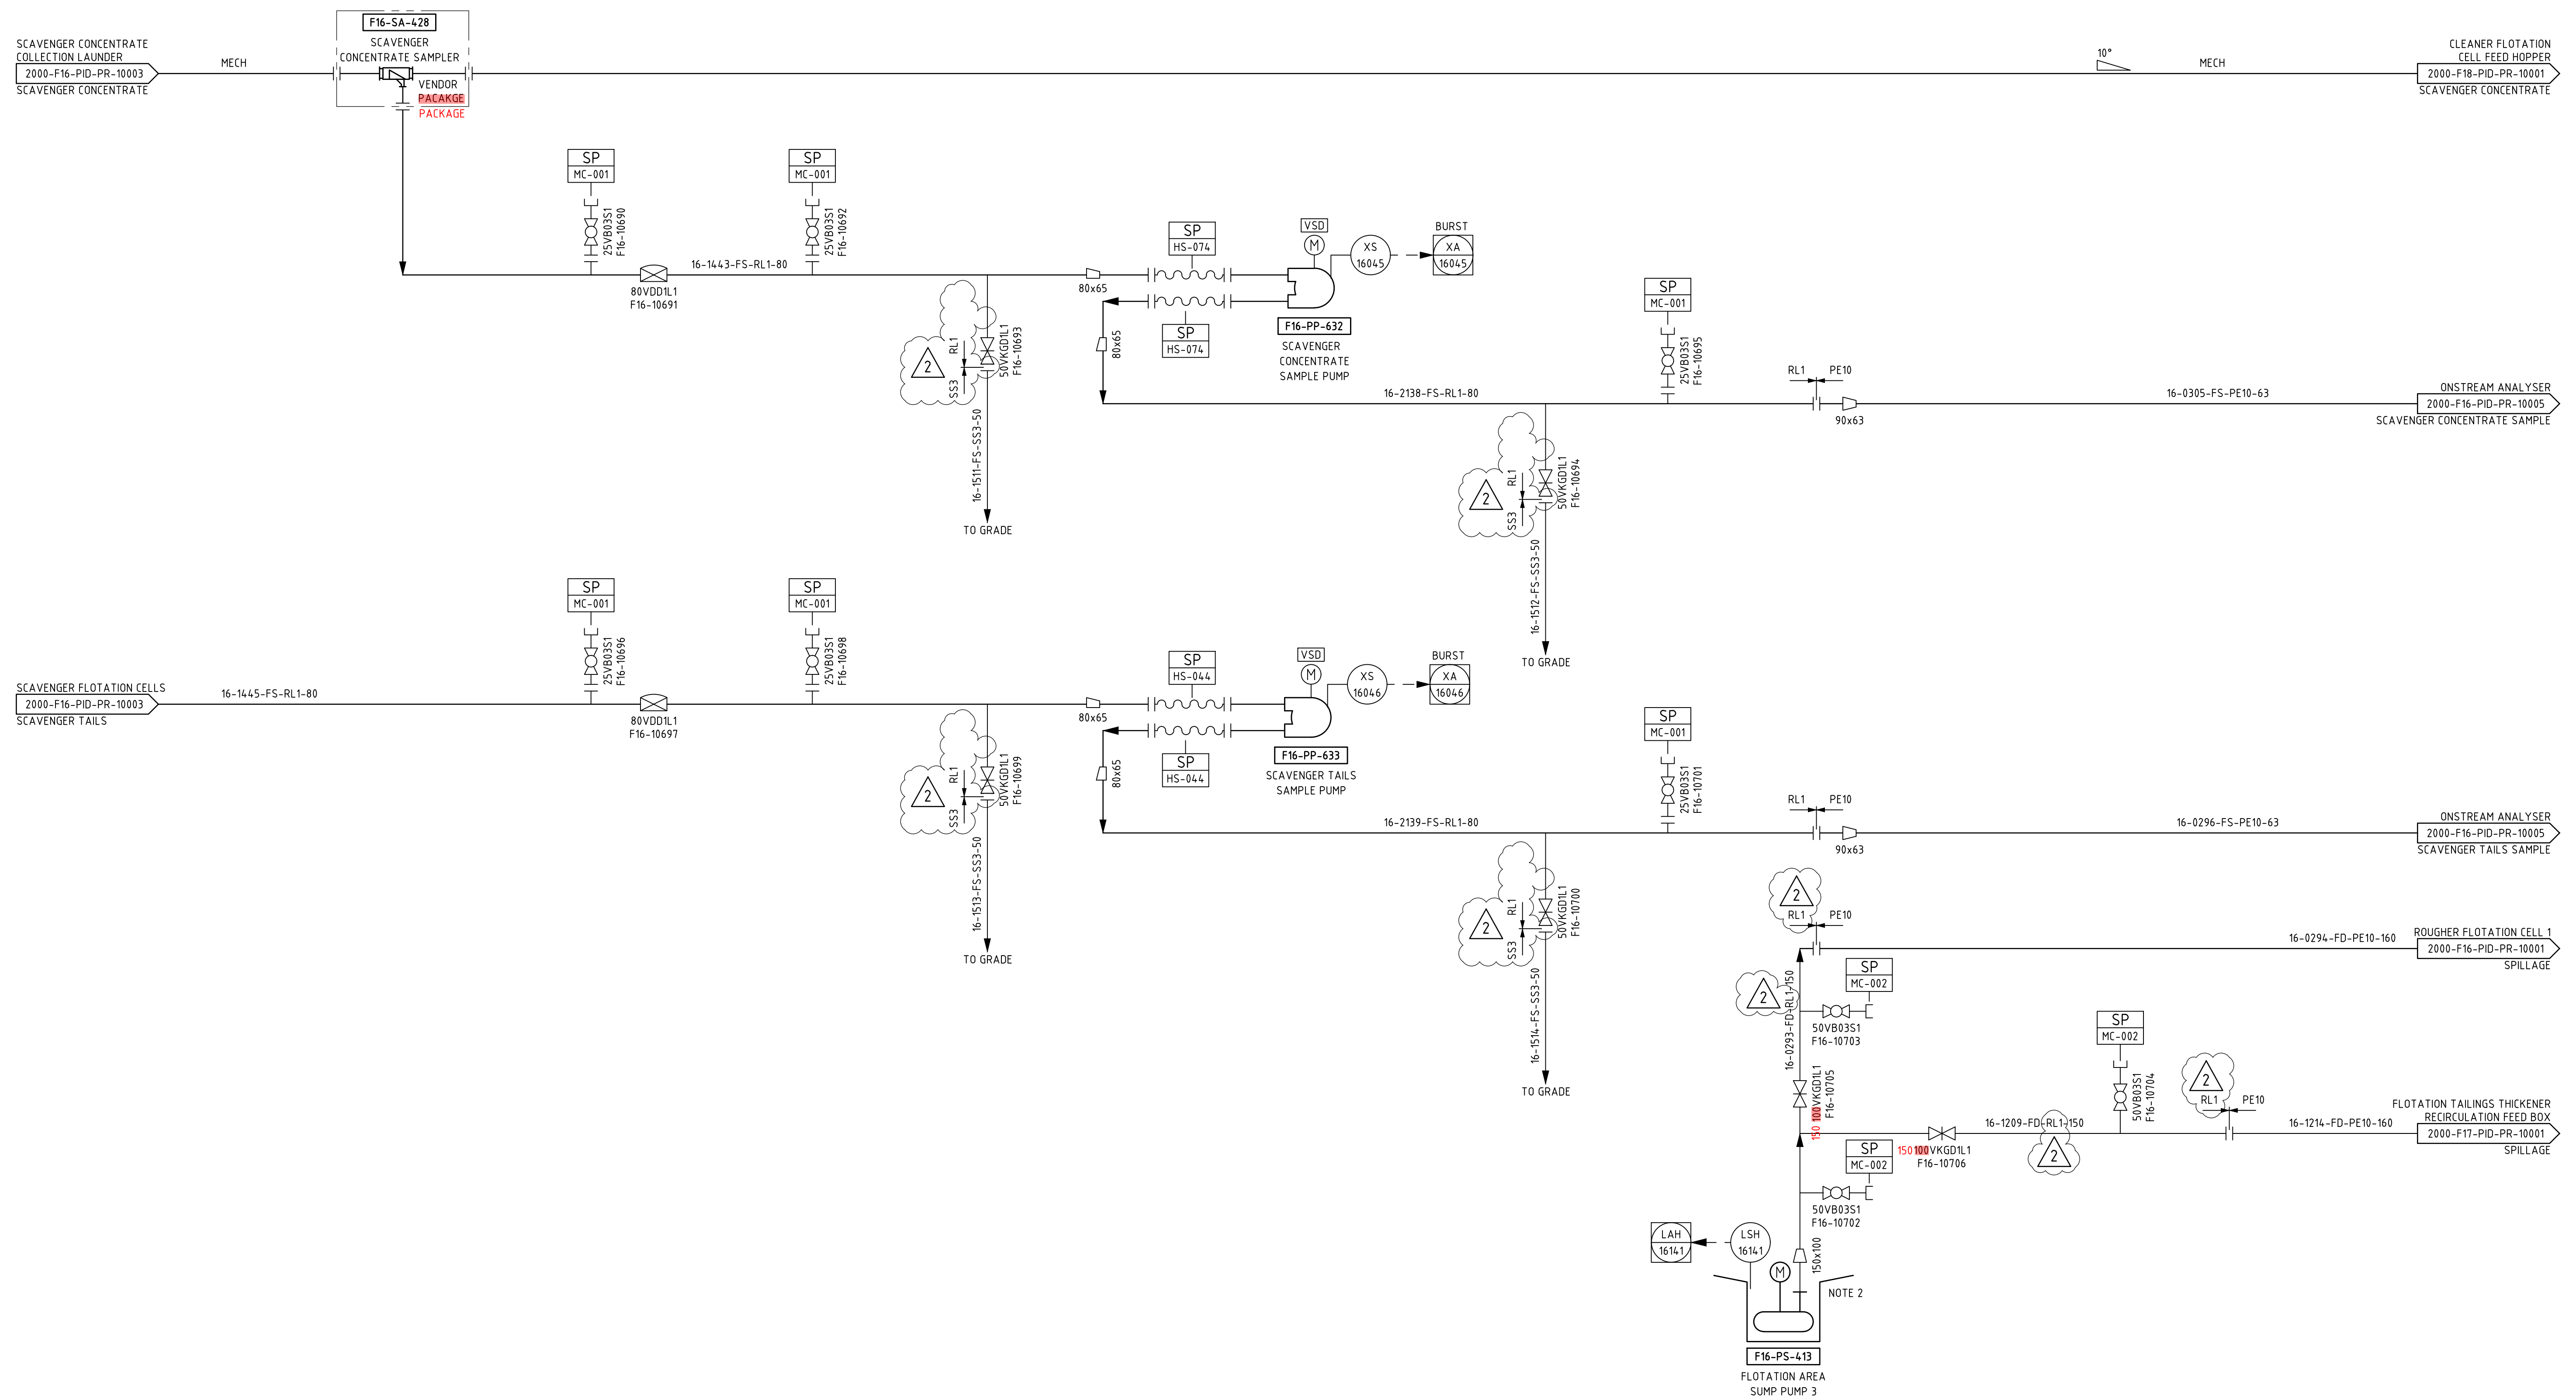


[illegible]

INFORMATION AND REPRESENTATIONS ON THIS DRAWING ARE THE INTELLECTUAL PROPERTY OF PRIMERO UNLESS SPECIFICALLY IDENTIFIED OTHERWISE. ALL RIGHTS INCLUDING USE RESERVED

PRIMERO
primero.com.au | DESIGN | CONSTRUCT | OPERATE

PRIMERO PROJECT NUMBER: 23517

PROJECT:	NORTHERN STAR RESOURCES LTD KCGM GROWTH PROJECT		
TITLE:	ROUGHER & SCAVENGER FLOTATION SCAVENGER FLOTATION - SHEET 2 - STAGE 1 PIPING AND INSTRUMENTATION DIAGRAM		
SHEET A1	SCALE NTS	DRG No. 2000-F16-PID-PR-10004	REVISION 2