


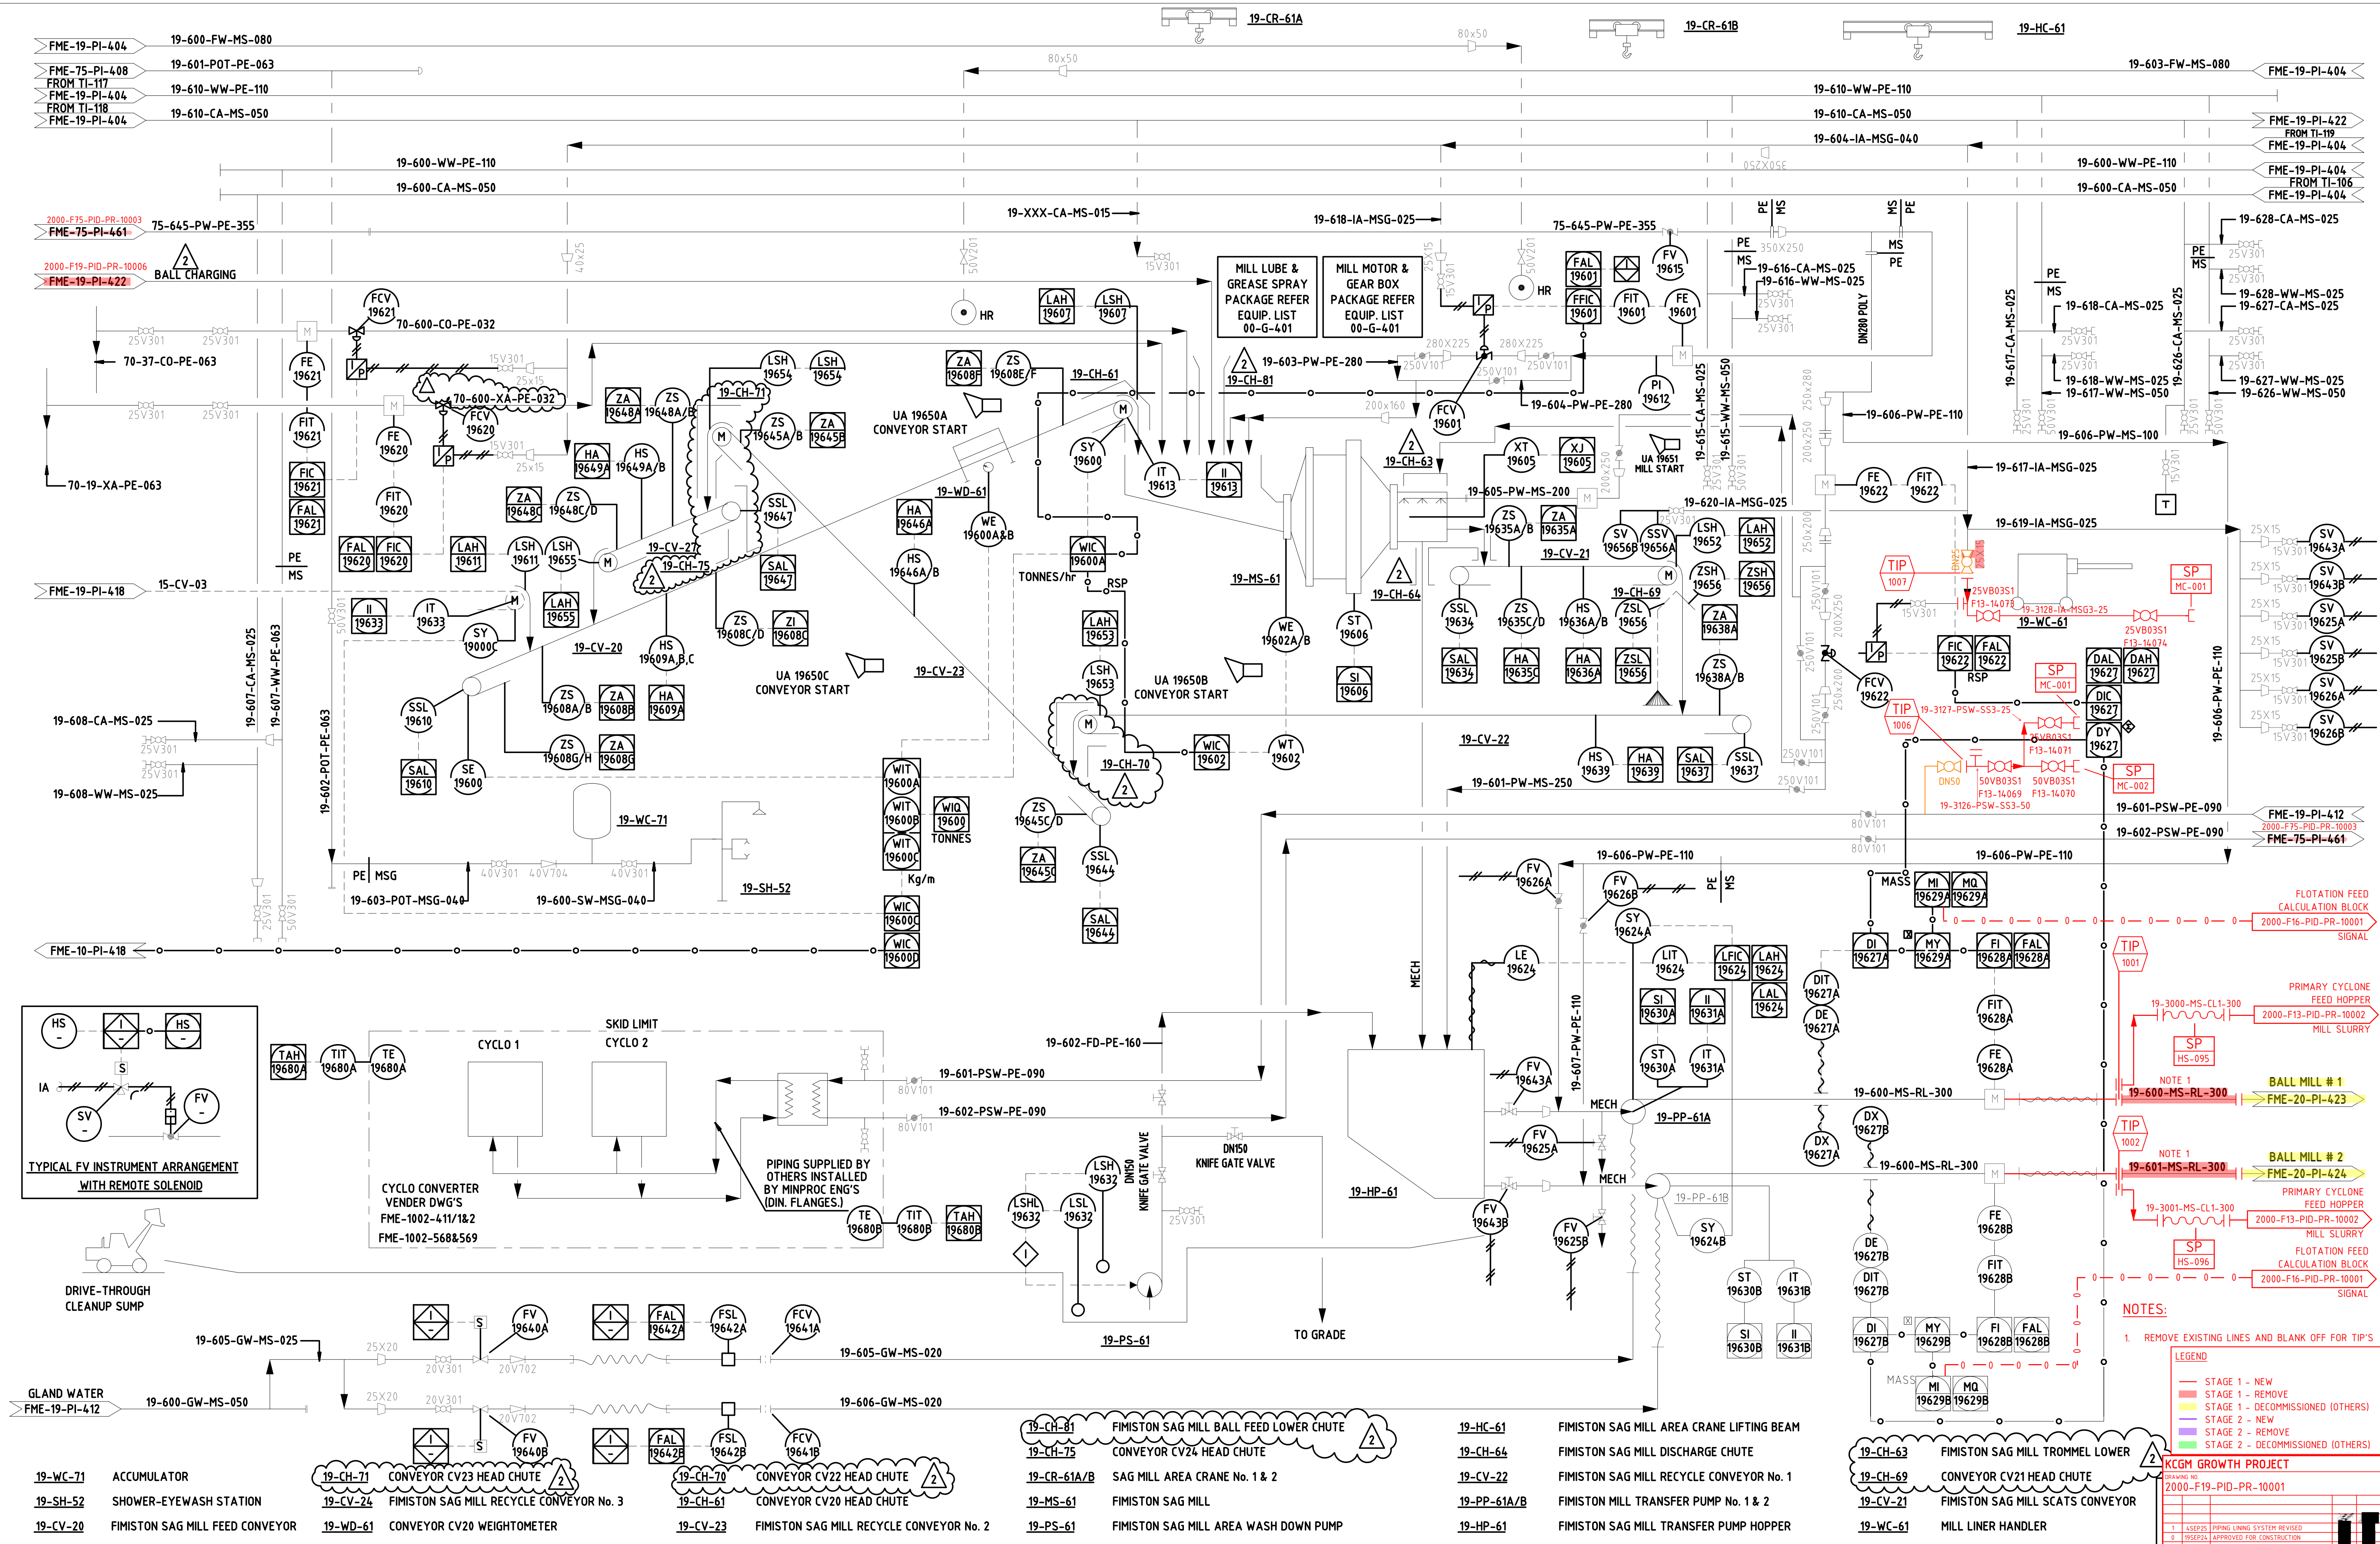

DRAWING No.		REFERENCE DRAWINGS		00-G-401		EQUIPMENT LIST	
No.		BY		DATE		REVISION	
		3		31/12/19		UPDATED	
		2		3/05/95		REVISED AS NOTED	
		1		21/04/95		APPROVED FOR CONSTRUCTION	
		0		17/03/95		APPROVED FOR TENDER F035	
PROJECT APPR.		BY		DATE		DESIGNED	
DESIGN APPR.		BY		DATE		CHECKED	
DRAWN		BY		DATE		PLANT GRID NORTH	
CLIENT		KALGOORLIE CONSOLIDATED GOLD MINES		TITLE		FIMISTON EXPANSION 1994/95 PIPING & INSTRUMENT DIAGRAM SAG MILLING - FIMISTON	
SIZE		B1		N.T.S.		REV.	
No.		1		2		3	
DRAWING No.		FME-19-PI-419		PROJECT		KCGM GROWTH PROJECT	
No.		2000-F19-PID-PR-10001		REVISION		1	
DATE		12-04-95		DESCRIPTION		LSEPS2 PIPING LINES SYSTEM REVISED	
						19SEP24 APPROVED FOR CONSTRUCTION	