


D:\CAD PROJECTS\235 NORTHERN STAR RESOURCES LTD\23517 KCGM GROWTH PROJECT\03 DELIVERABLES\PR\PID\ISSUED\12.09.25 - SIGNING\NATIVES\2000-F22-PID-PR-10001_1.DWG 09SEP25 8:06AM ANNE.HOYNE

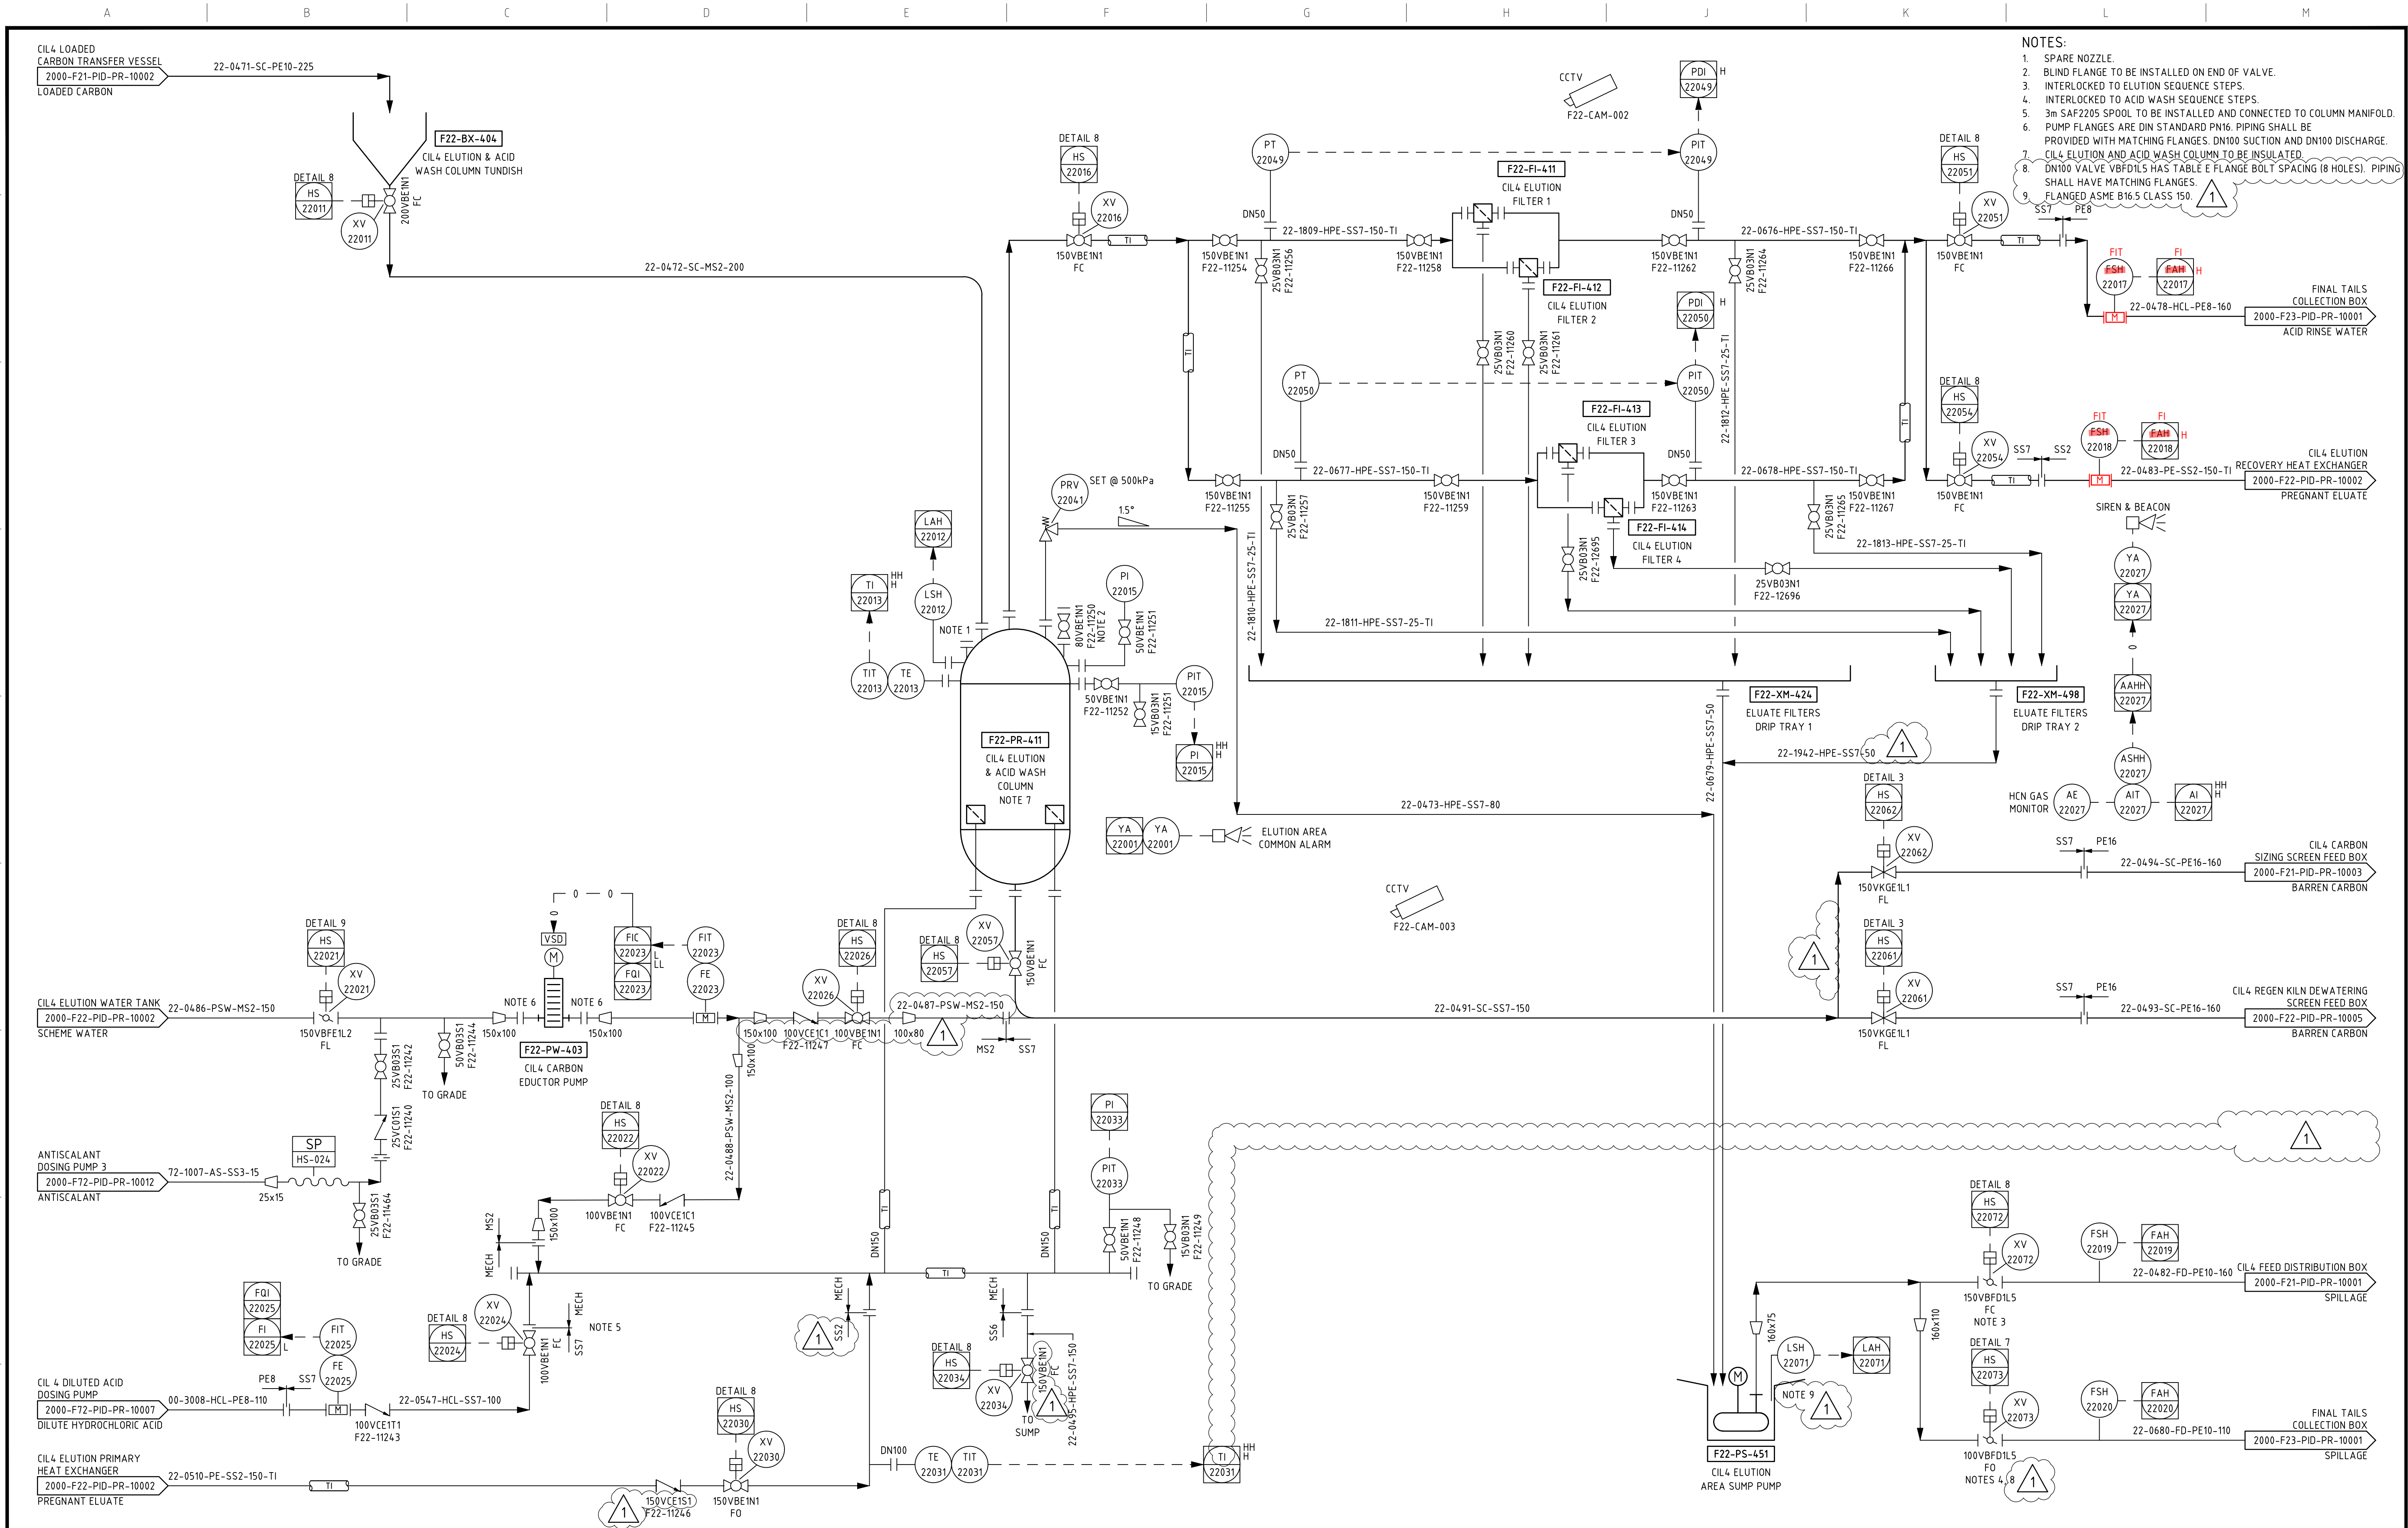

- NOTES:
1. SPARE NOZZLE.
 2. BLIND FLANGE TO BE INSTALLED ON END OF VALVE.
 3. INTERLOCKED TO ELUTION SEQUENCE STEPS.
 4. INTERLOCKED TO ACID WASH SEQUENCE STEPS.
 5. 3m SAFZ05 SPOOL TO BE INSTALLED AND CONNECTED TO COLUMN MANIFOLD.
 6. PUMP FLANGES ARE DIN STANDARD PN16. PIPING SHALL BE PROVIDED WITH MATCHING FLANGES. DN100 SUCTION AND DN100 DISCHARGE.
 7. CIL4 ELUTION AND ACID WASH COLUMN TO BE INSULATED.
 8. DN100 VALVE VBF015 HAS TABLE E FLANGE BOLT SPACING (8 HOLES). PIPING SHALL HAVE MATCHING FLANGES.
 9. FLANGED ASME B16.5 CLASS 150.

LEGEND		REV		DATE		DESCRIPTION		DRAW		CHECK		DESIGN		TECH APP		PROJ APP	
2000-F00-PID-PR-10007	LEGEND SHEET 7 - PIPING AND INSTRUMENTATION DIAGRAM																
2000-F00-PID-PR-10006	LEGEND SHEET 6 - PIPING AND INSTRUMENTATION DIAGRAM																
2000-F00-PID-PR-10005	LEGEND SHEET 5 - PIPING AND INSTRUMENTATION DIAGRAM																
2000-F00-PID-PR-10004	LEGEND SHEET 4 - PIPING AND INSTRUMENTATION DIAGRAM																
2000-F00-PID-PR-10003	LEGEND SHEET 3 - PIPING AND INSTRUMENTATION DIAGRAM																
2000-F00-PID-PR-10002	LEGEND SHEET 2 - PIPING AND INSTRUMENTATION DIAGRAM																
2000-F00-PID-PR-10001	LEGEND SHEET 1 - PIPING AND INSTRUMENTATION DIAGRAM																
DRG No.	REFERENCES	REV	DATE	DESCRIPTION		DRAW		CHECK		DESIGN		TECH APP		PROJ APP			
		1	12SEP25	GENERAL REVISIONS ADDED													
		0	15MAY25	APPROVED FOR CONSTRUCTION													

PROJECT: NORTHERN STAR RESOURCES LTD KCGM GROWTH PROJECT	
TITLE: CIL4 - CARBON TREATMENT & ELUTION ELUTION - SHEET 1 PIPING AND INSTRUMENTATION DIAGRAM	
SHEET: A1	SCALE: NTS
DRG No.: 2000-F22-PID-PR-10001	REVISION: 1



INFORMATION AND REPRESENTATIONS ON THIS DRAWING ARE THE INTELLECTUAL PROPERTY OF PRIMERO UNLESS SPECIFICALLY IDENTIFIED OTHERWISE. ALL RIGHTS INCLUDING USE RESERVED