


D:\CAD PROJECTS\235 NORTHERN STAR RESOURCES LTD\23517 KCGM GROWTH PROJECT\3 DELIVERABLES\PR\PI\NATIVES\2000-F22-PID-PR-10002_1.DWG 09SEP25 8:08AM ANNE HOYNE

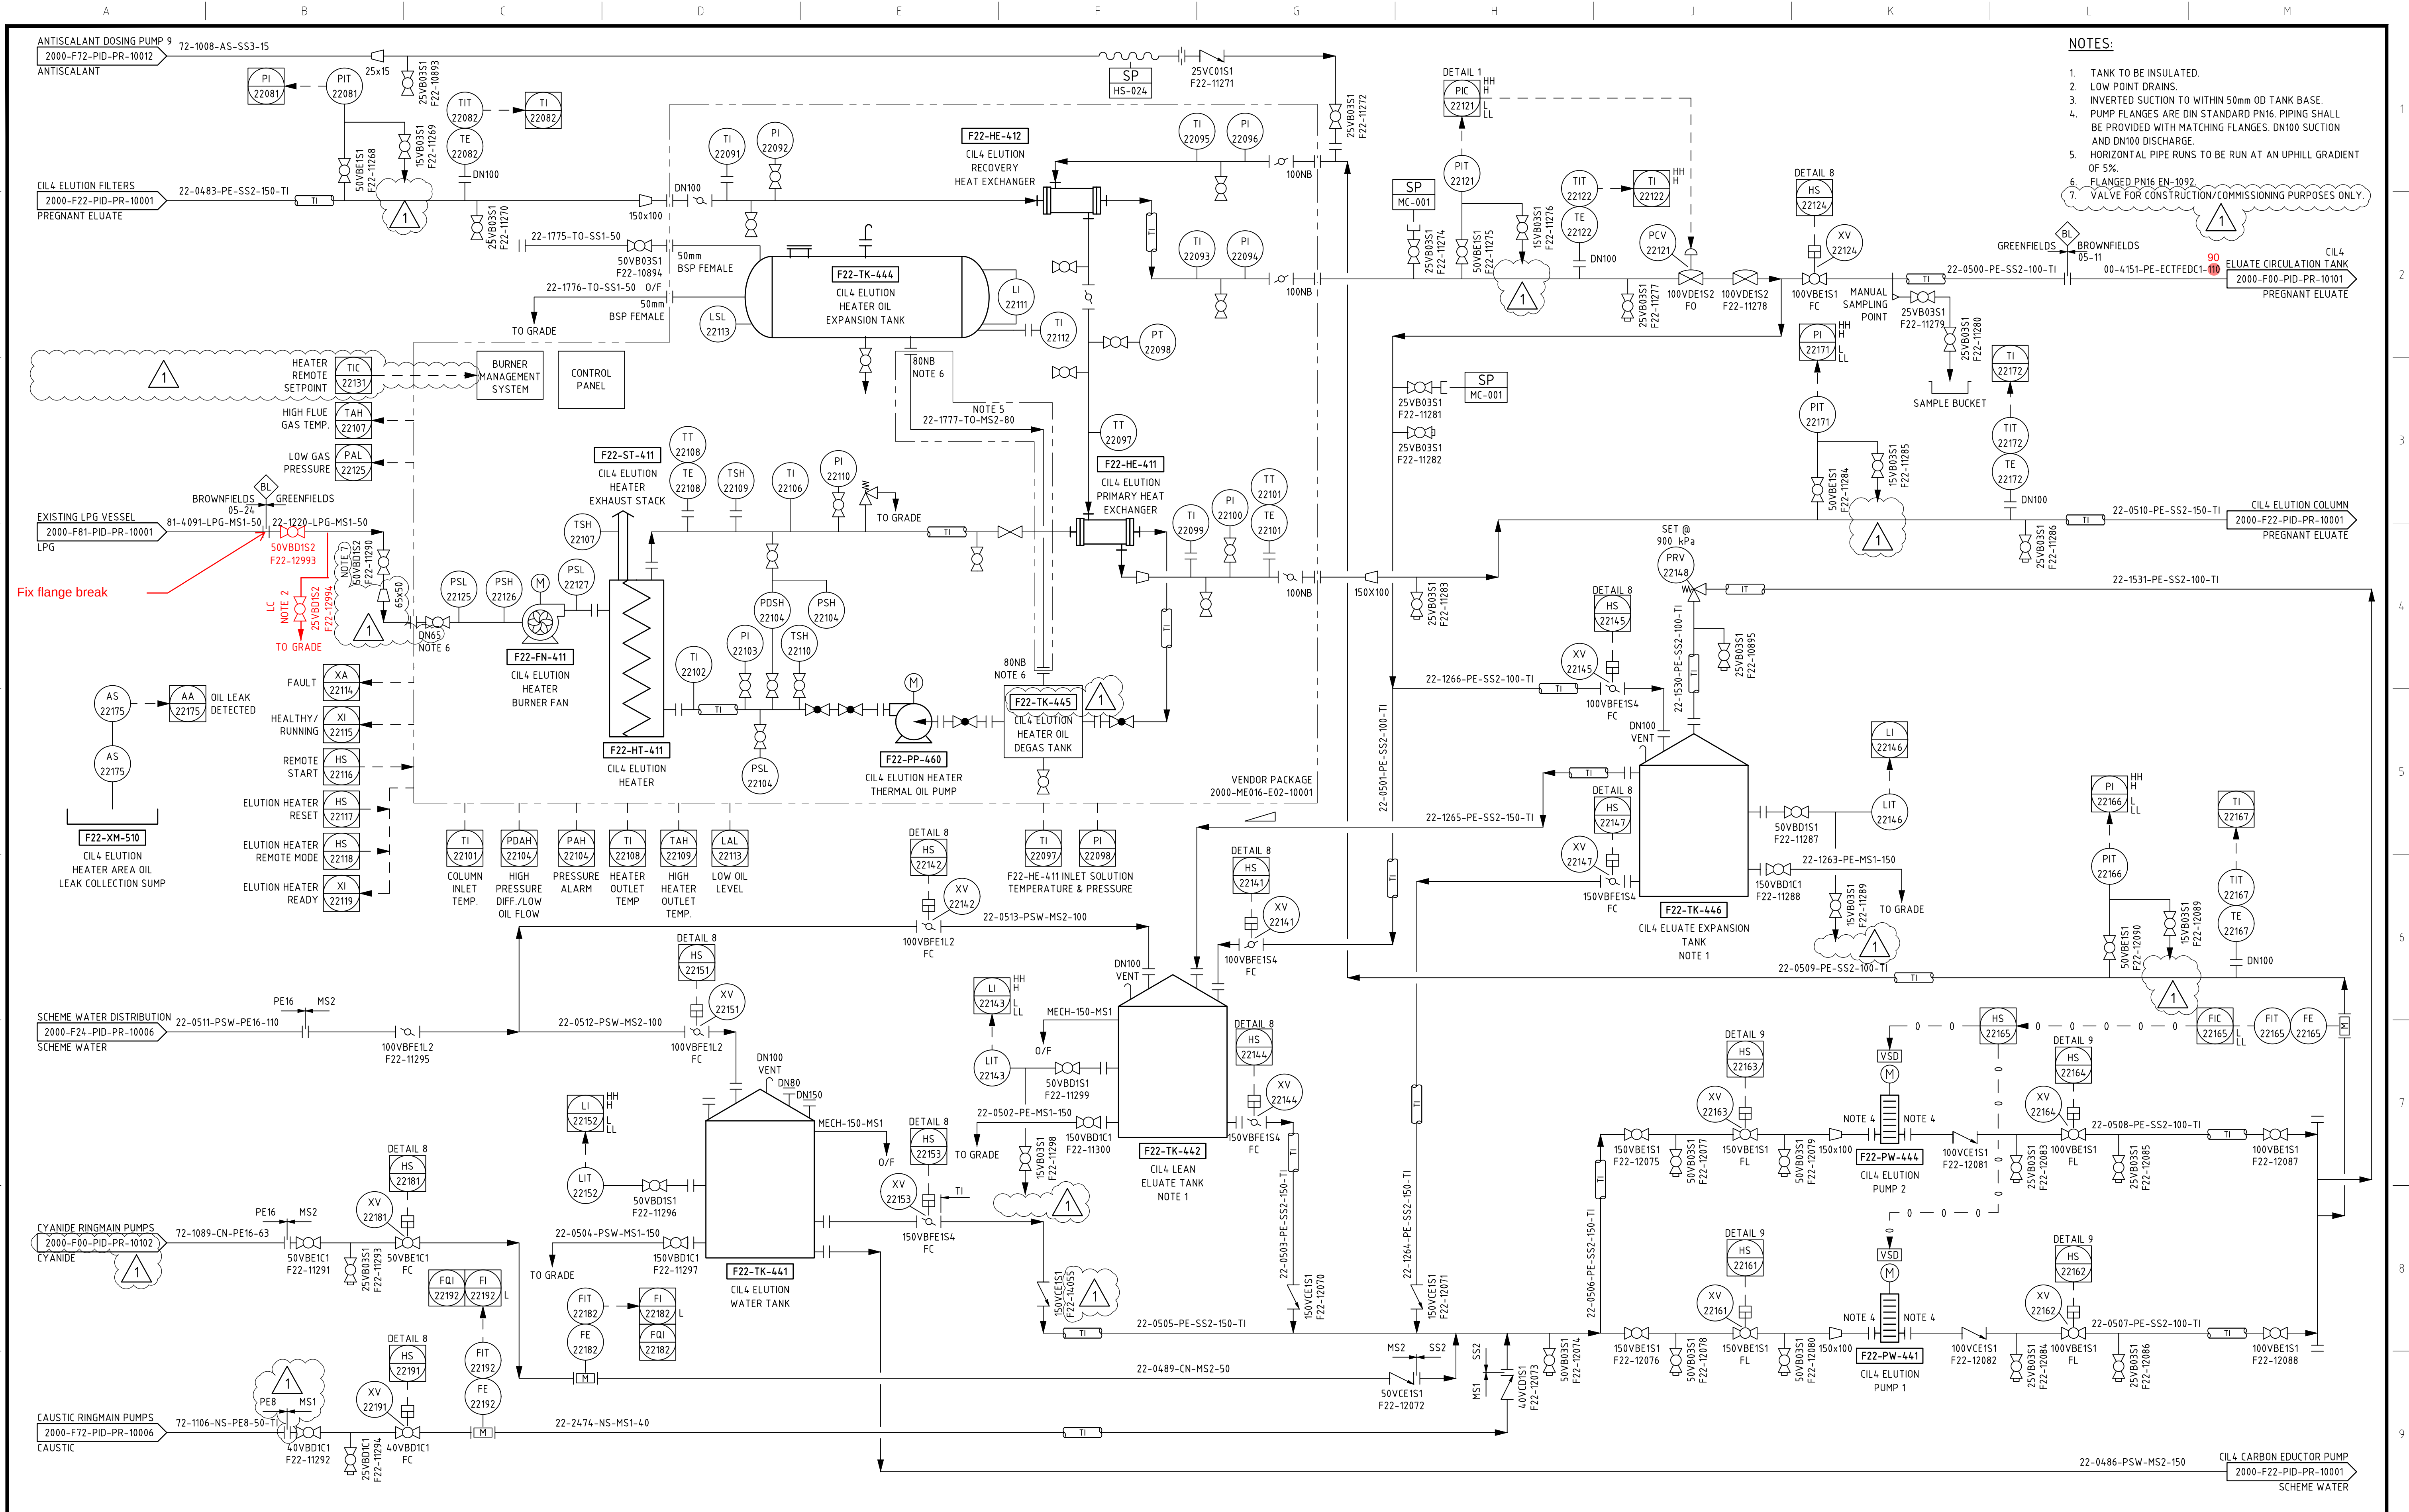


NOTES:

1. TANK TO BE INSULATED.
2. LOW POINT DRAINS.
3. INVERTED SUCTION TO WITHIN 50mm OD TANK BASE.
4. PUMP FLANGES ARE DIN STANDARD PN16. PIPING SHALL BE PROVIDED WITH MATCHING FLANGES. DN100 SUCTION AND DN100 DISCHARGE.
5. HORIZONTAL PIPE RUNS TO BE RUN AT AN UPHILL GRADIENT OF 5%.
6. FLANGED PN16 EN-1092
7. VALVE FOR CONSTRUCTION/COMMISSIONING PURPOSES ONLY.

2000-F00-PID-PR-10007	LEGEND SHEET 7 - PIPING AND INSTRUMENTATION DIAGRAM
2000-F00-PID-PR-10006	LEGEND SHEET 6 - PIPING AND INSTRUMENTATION DIAGRAM
2000-F00-PID-PR-10005	LEGEND SHEET 5 - PIPING AND INSTRUMENTATION DIAGRAM
2000-F00-PID-PR-10004	LEGEND SHEET 4 - PIPING AND INSTRUMENTATION DIAGRAM
2000-F00-PID-PR-10003	LEGEND SHEET 3 - PIPING AND INSTRUMENTATION DIAGRAM
2000-F00-PID-PR-10002	LEGEND SHEET 2 - PIPING AND INSTRUMENTATION DIAGRAM
2000-F00-PID-PR-10001	LEGEND SHEET 1 - PIPING AND INSTRUMENTATION DIAGRAM

DRG No.	REFERENCES
---------	------------

REV	DATE	DESCRIPTION
1	12SEP25	GENERAL REVISIONS AS NOTED
0	15MAY25	APPROVED FOR CONSTRUCTION

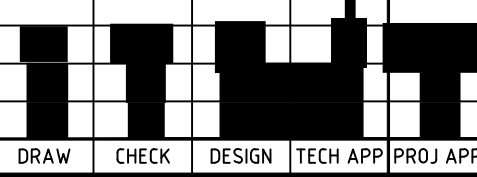

INFORMATION AND REPRESENTATIONS ON THIS DRAWING ARE THE INTELLECTUAL PROPERTY OF PRIMERO UNLESS SPECIFICALLY IDENTIFIED OTHERWISE. ALL RIGHTS INCLUDING USE RESERVED



PRIMERO PROJECT NUMBER:

23517

PROJECT: NORTHERN STAR RESOURCES LTD
KCGM GROWTH PROJECT

TITLE: CIL4 - CARBON TREATMENT & ELUTION
ELUTION - SHEET 2
PIPING AND INSTRUMENTATION DIAGRAM

SHEET: A1 SCALE: NTS DRG No.: 2000-F22-PID-PR-10002

REVISION

1