


D:\CAD PROJECTS\235 NORTHERN STAR RESOURCES LTD\23517 KCGM GROWTH PROJECT\03 DELIVERABLES\PR\PID\ISSUED 05.09.2025 - SIGNING NATIVES\2000-F28-PID-PR-10005_2.DWG 04SEP25 12:43PM ANNE HOYNE

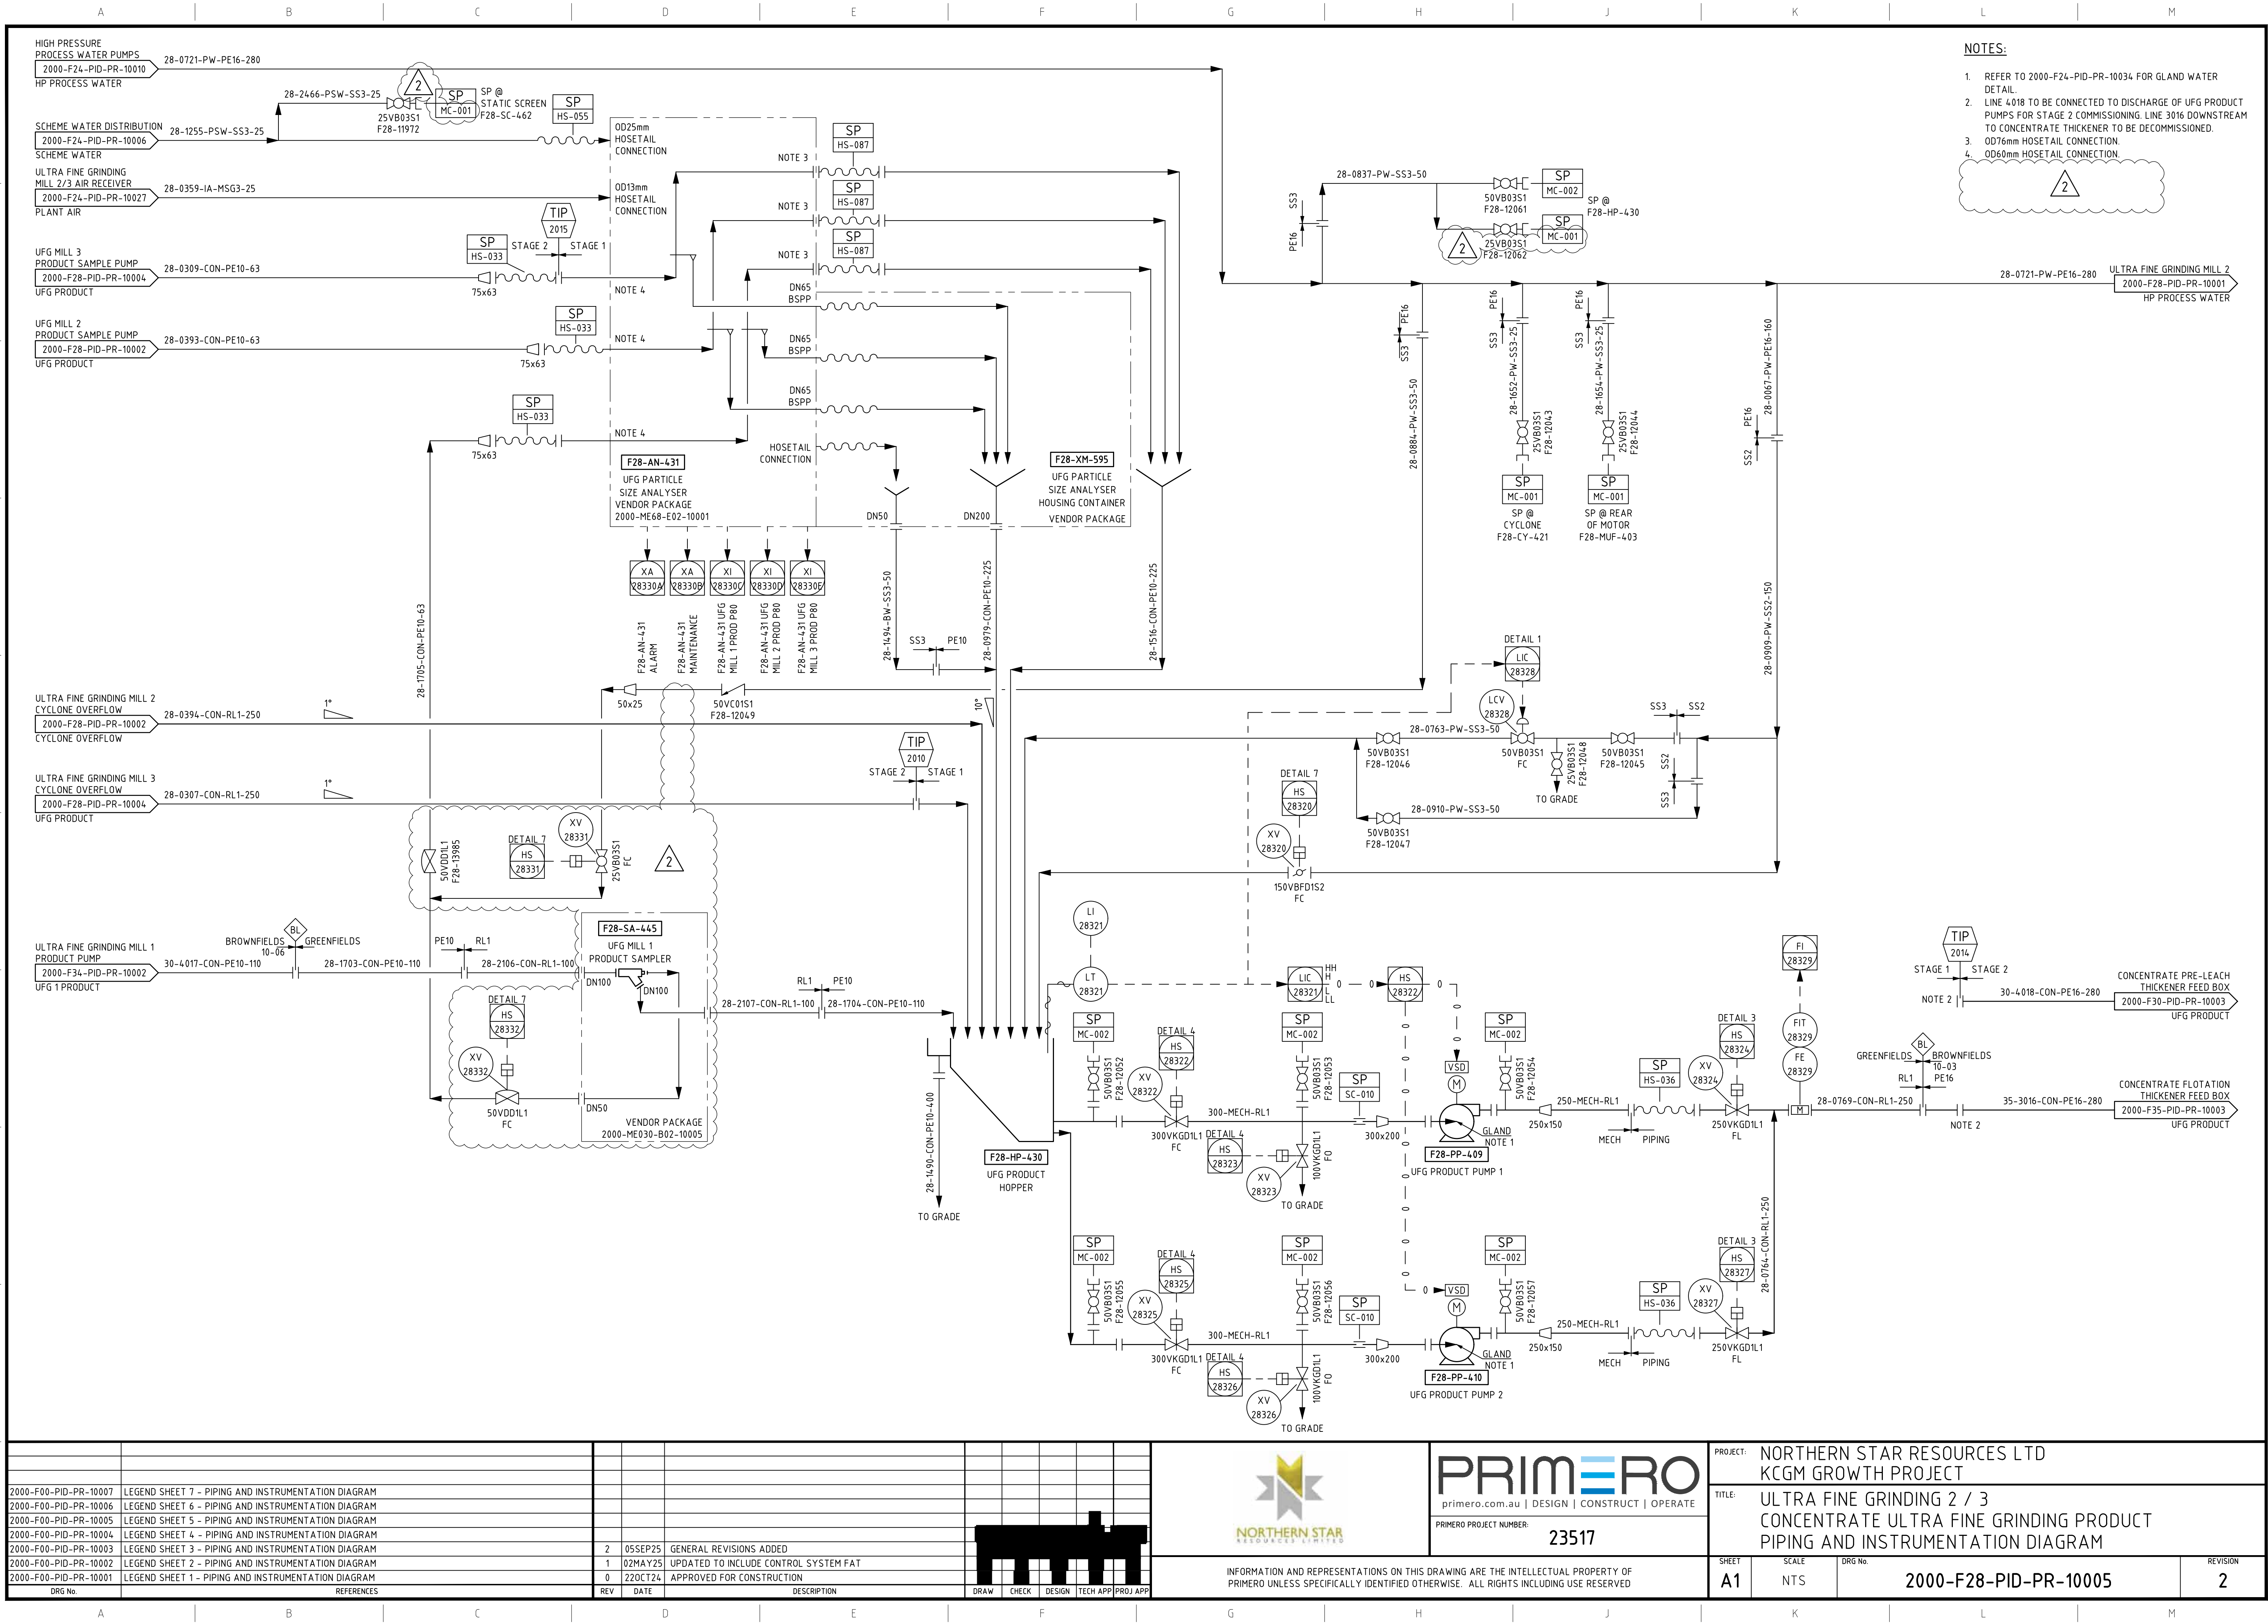

PROJECT: NORTHERN STAR RESOURCES LTD KCGM GROWTH PROJECT	
TITLE: ULTRA FINE GRINDING 2 / 3 CONCENTRATE ULTRA FINE GRINDING PRODUCT PIPING AND INSTRUMENTATION DIAGRAM	
SHEET: A1	SCALE: NTS
DRG No.: 2000-F28-PID-PR-10005	REVISION: 2

INFORMATION AND REPRESENTATIONS ON THIS DRAWING ARE THE INTELLECTUAL PROPERTY OF PRIMERO UNLESS SPECIFICALLY IDENTIFIED OTHERWISE. ALL RIGHTS INCLUDING USE RESERVED