


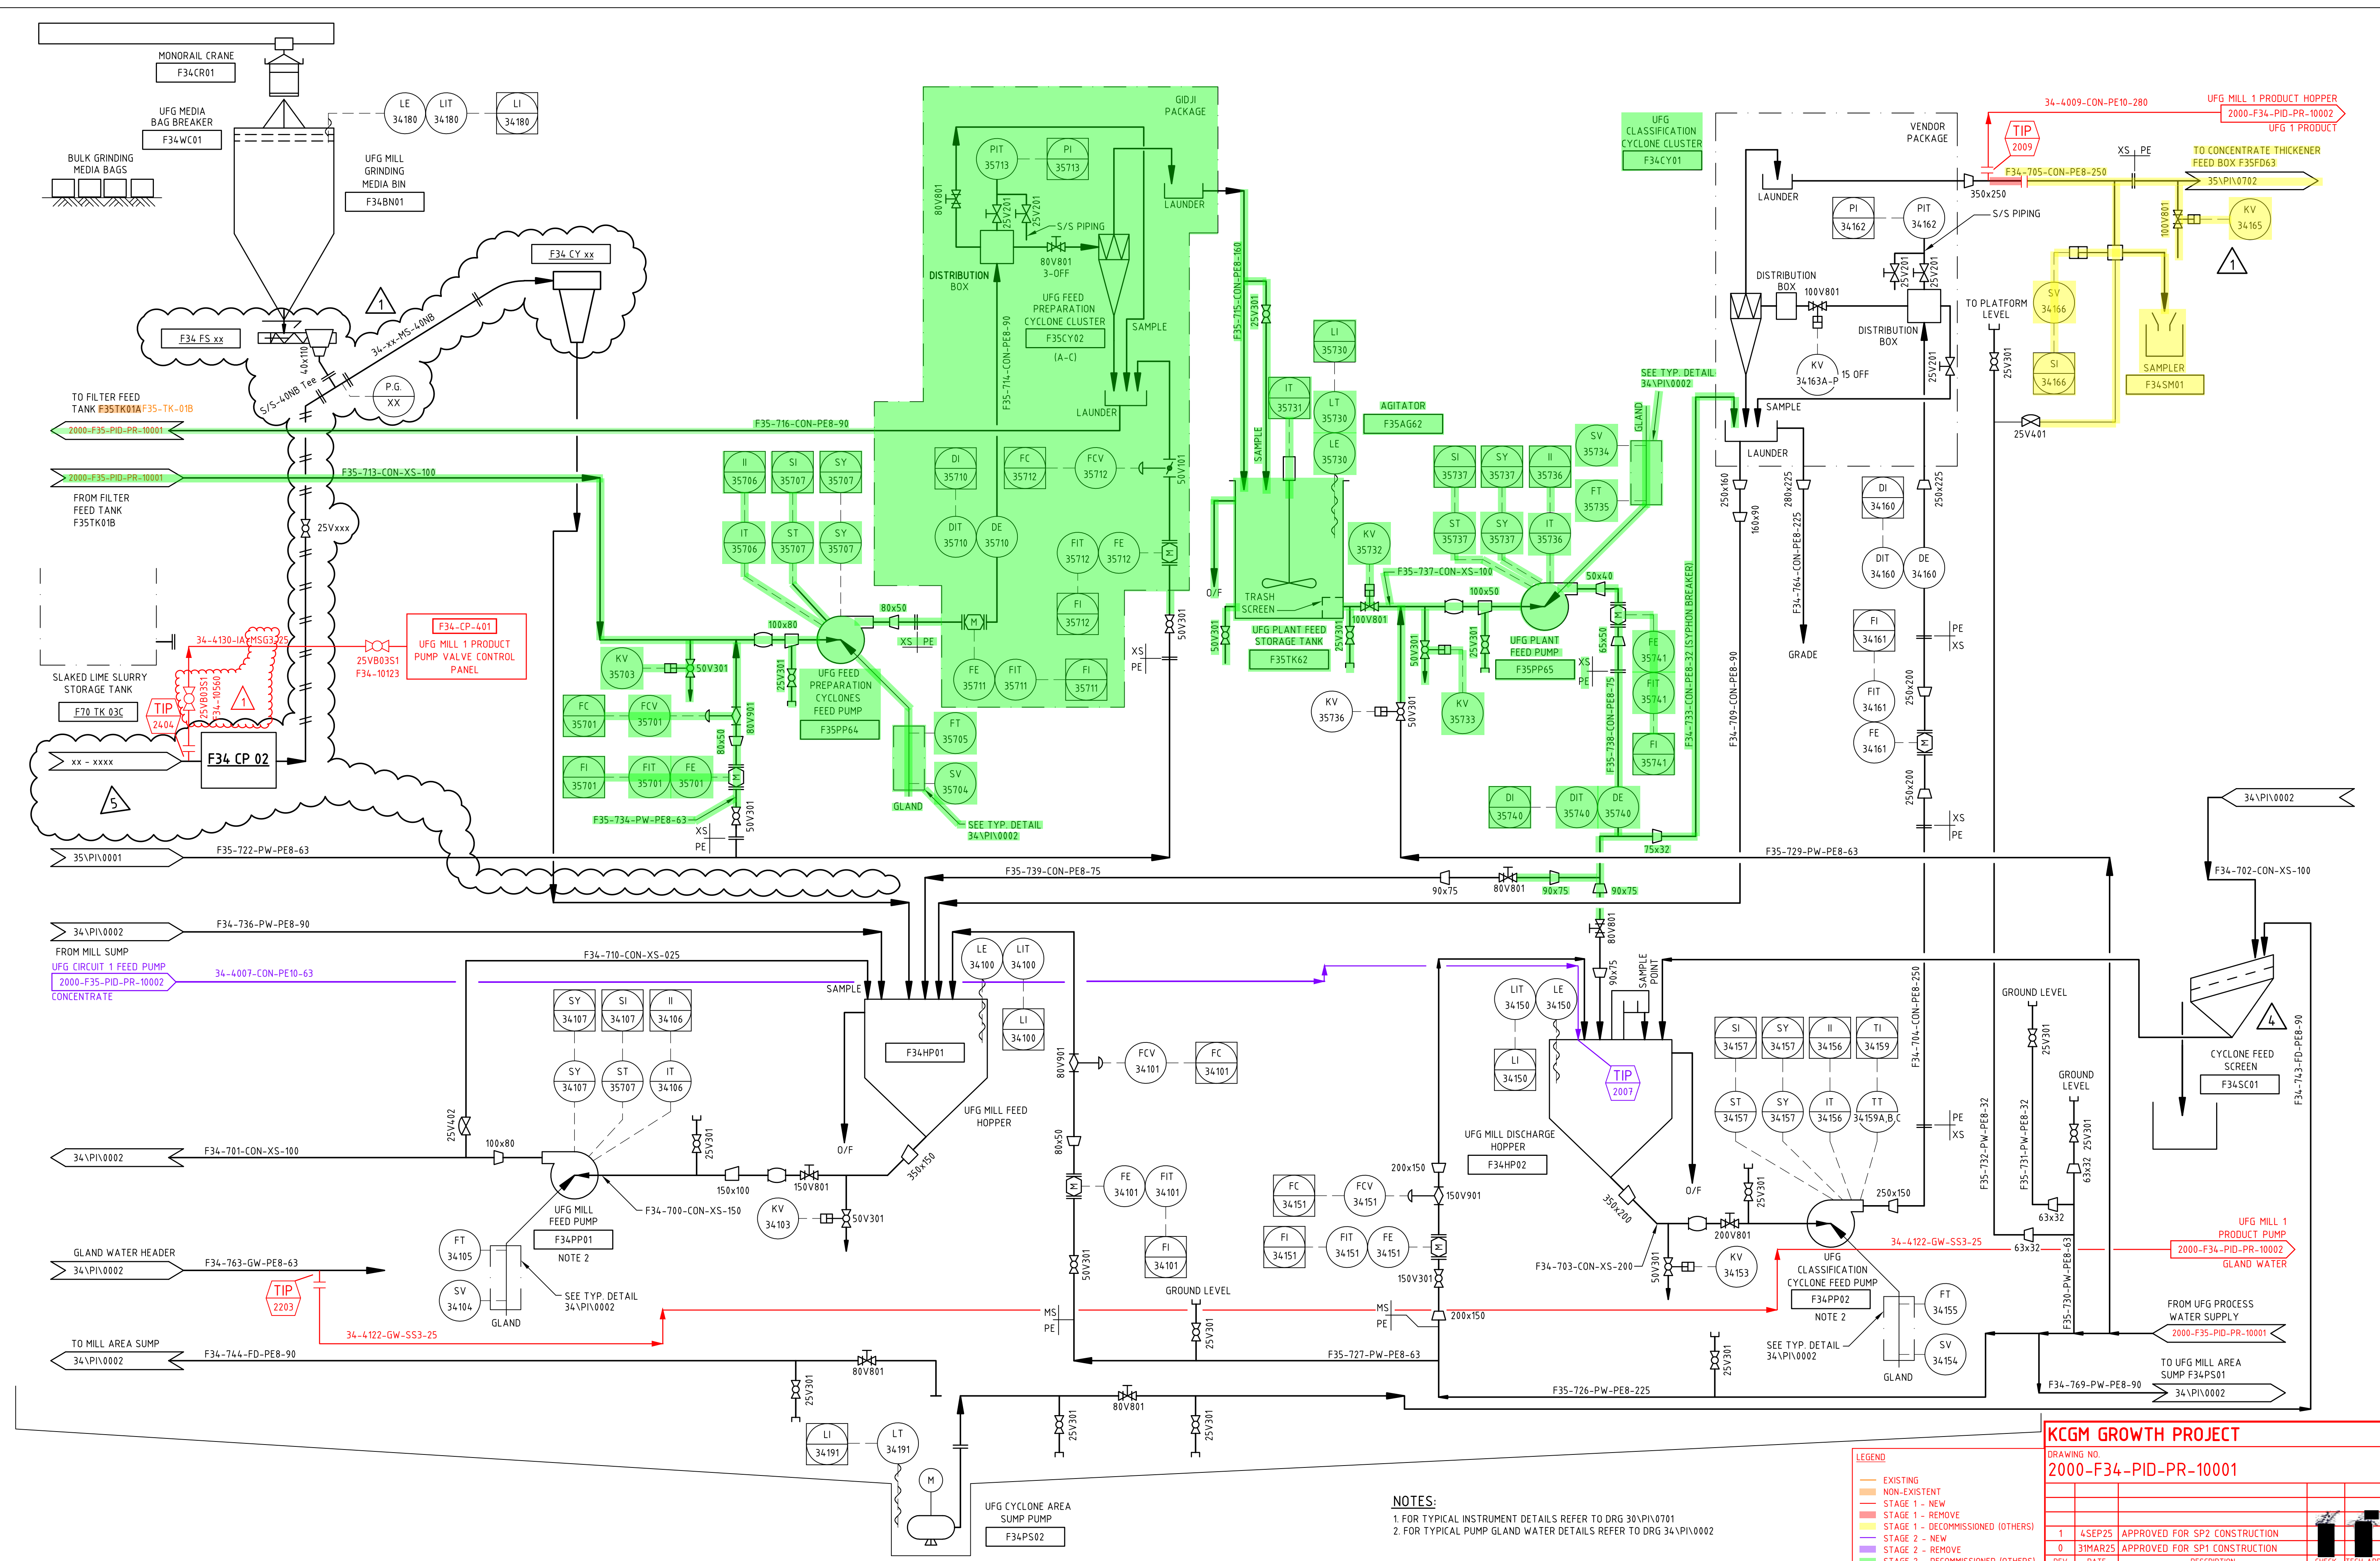

NOTES:
1. FOR TYPICAL INSTRUMENT DETAILS REFER TO DRG 30\PI\0701
2. FOR TYPICAL PUMP GLAND WATER DETAILS REFER TO DRG 34\PI\0002

LEGEND			
—	EXISTING		
—	NON-EXISTENT		
—	STAGE 1 - NEW		
—	STAGE 1 - REMOVE		
—	STAGE 1 - DECOMMISSIONED (OTHERS)		
—	STAGE 2 - NEW		
—	STAGE 2 - REMOVE		
—	STAGE 2 - DECOMMISSIONED (OTHERS)		

KCGM GROWTH PROJECT			
DRAWING NO. 2000-F34-PID-PR-10001			
REV	DATE	DESCRIPTION	CHECK TECH APP
1	4SEP25	APPROVED FOR SP2 CONSTRUCTION	
0	31MAR25	APPROVED FOR SP1 CONSTRUCTION	

				5	30.03.2020	NOT BUILT* EQUIPMENT REMOVED - AIR LIFT ADDED				T.R.		-					SCALE		NTS		FIMISTON PLANT ULTRA FINE GRINDING CLASSIFICATION AREA PIPING AND INSTRUMENTATION DIAGRAM				DRAWING NUMBER		REV	
				4	4/12/02	34SC01				-		-					DRAWN		30/08/01									
				3	22.05.02	NOT BUILT* NOTE ADDED							LEACH AREA - PIPING AND INSTRUMENTATION DIAGRAM				DESIGNED		30/08/01									
				2	08.03.02	4110 REMOVED							CONCENTRATE THICKENER AREA - PIPING AND INSTRUMENTATION DIAGRAM				CHECKED		23/10/01									
				1	22/11/01	AND DUMP VALVE ADDED				CP			GRINDING MILL AREA - PIPING AND INSTRUMENTATION DIAGRAM				APPROVED											
				0	21/11/01	APPROVED FOR CONSTRUCTION				CP			DESLEIME AREA - PIPING AND INSTRUMENTATION DIAGRAM				35\PIV0001		PROJ.APP									
MK		DATE		REVISION		BY		CKD		APP		REVISION		BY		CKD		APP		DWG NO.		PROJ. FILE #.		KALGOORLIE CONSOLIDATED GOLD MINES PTY. LTD. ABN 009 377 619 003				