


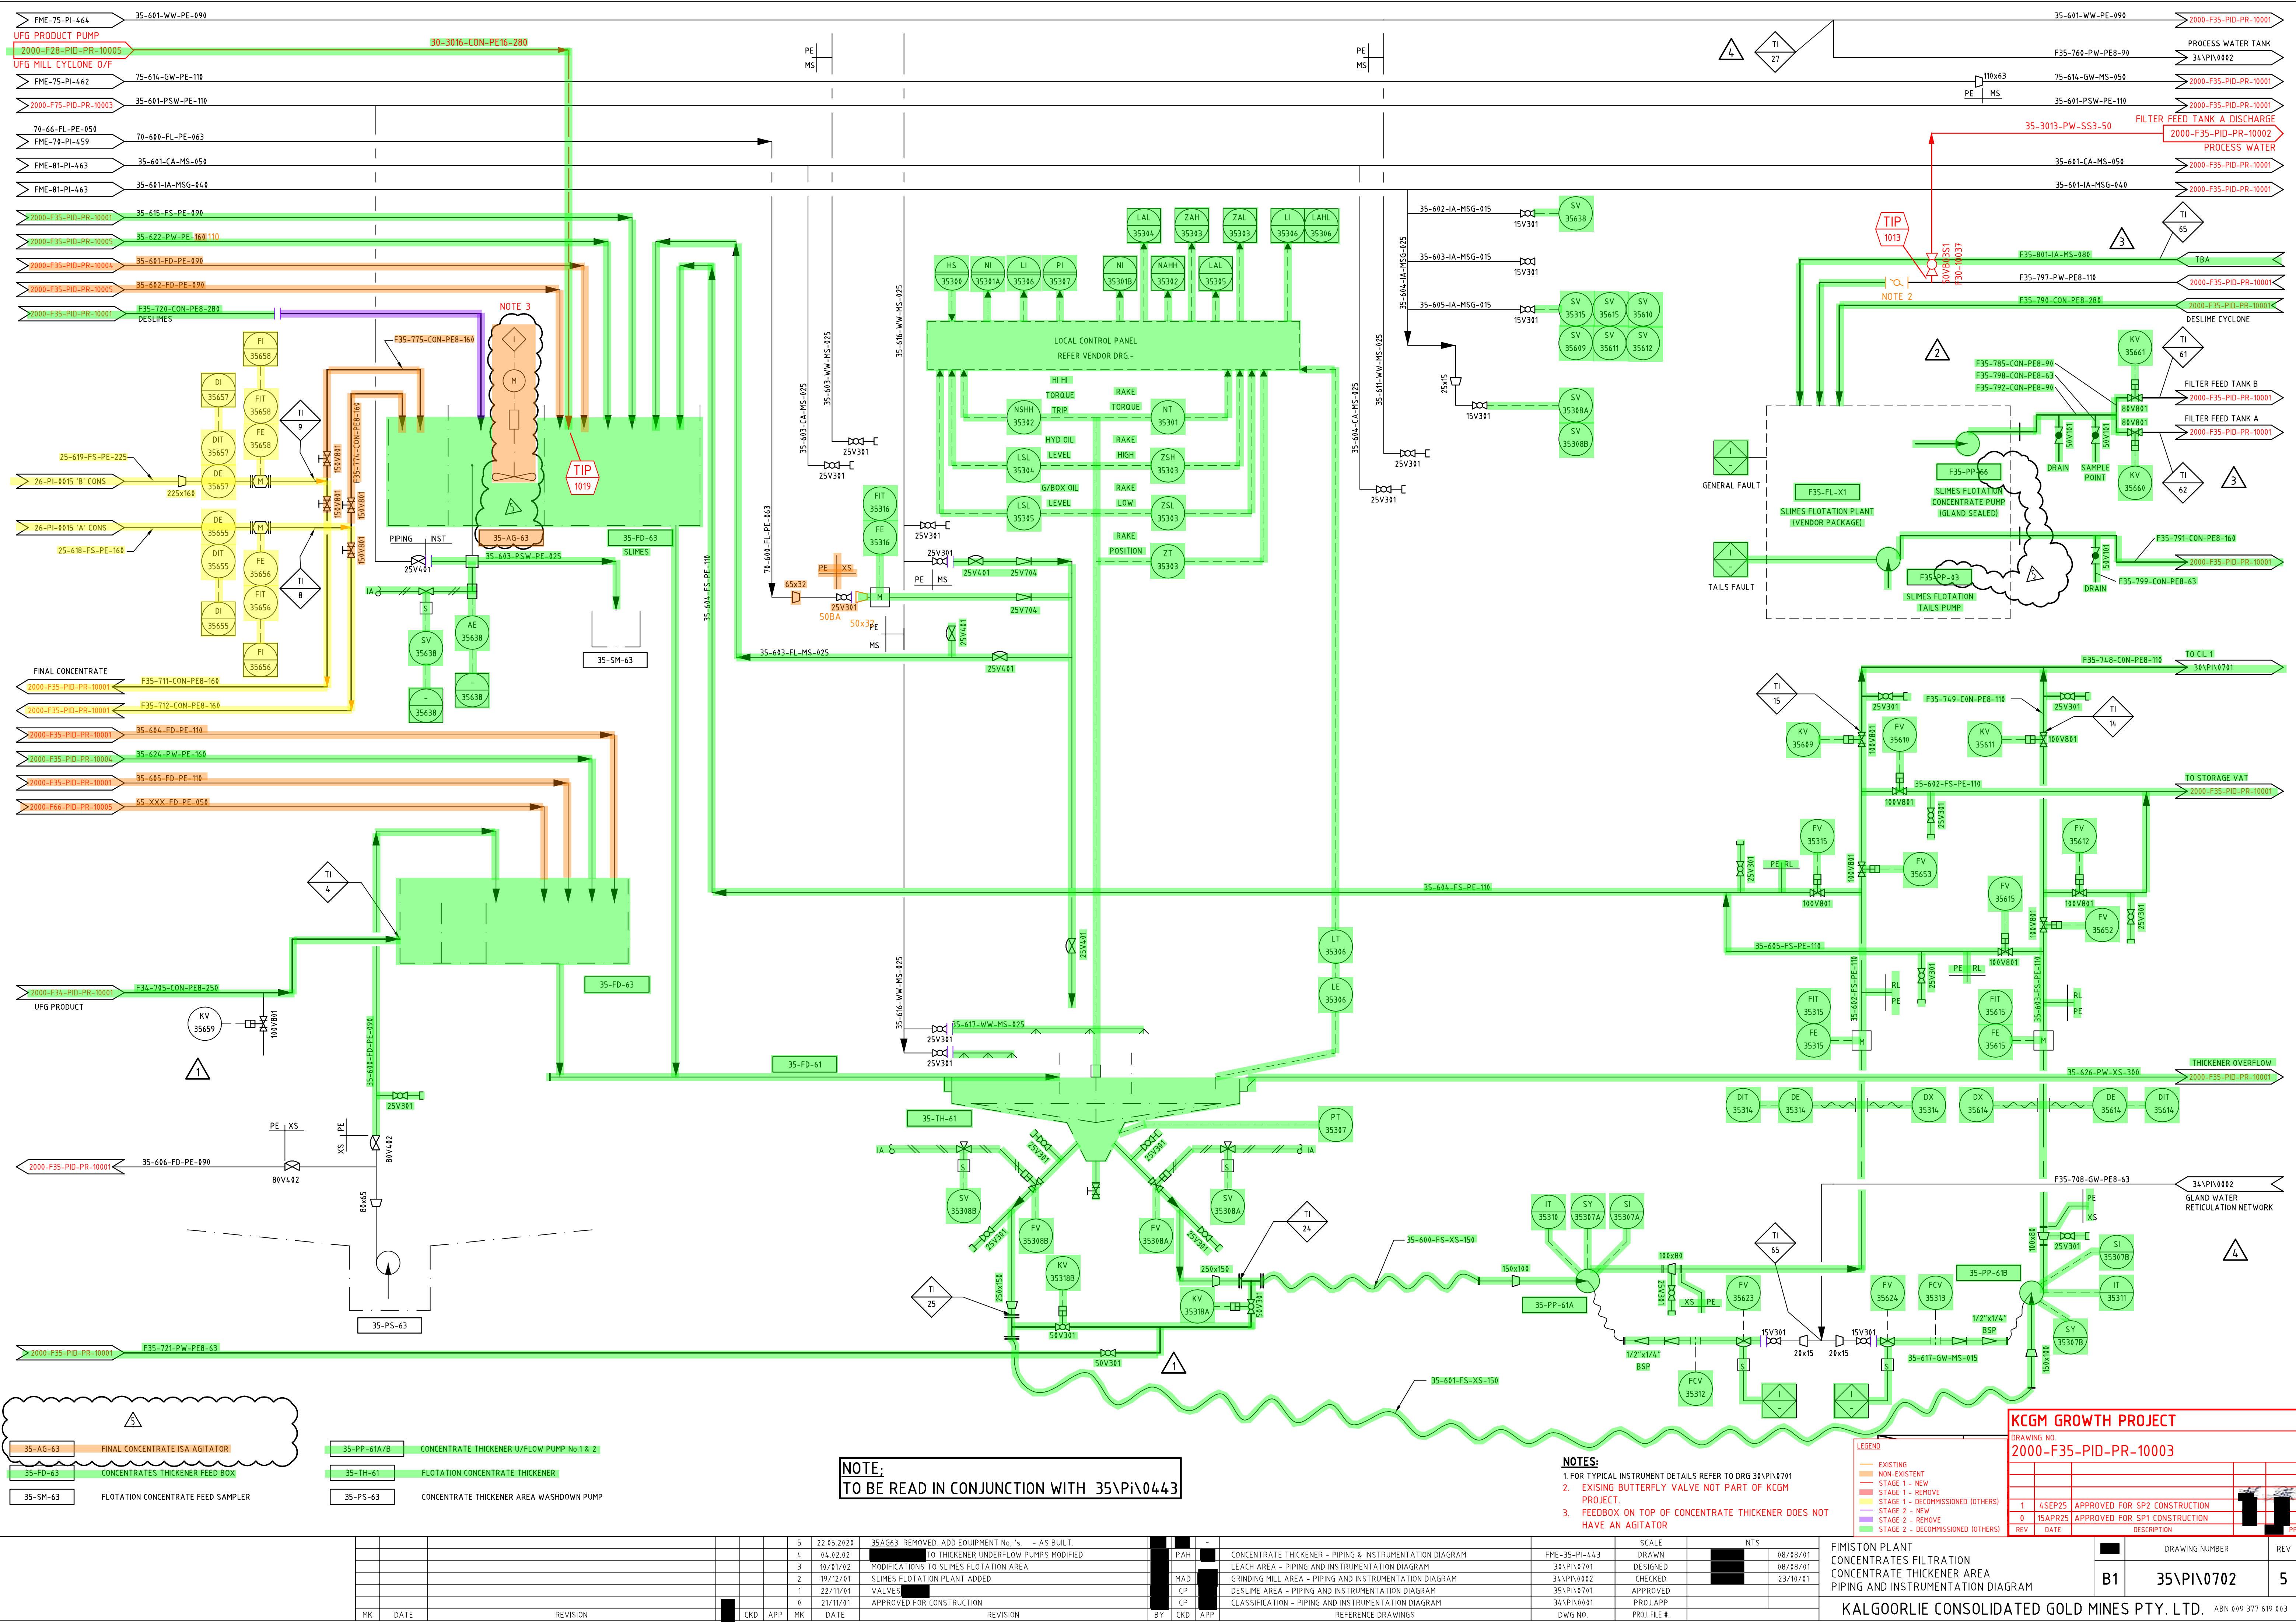

35-AG-63

FINAL CONCENTRATE ISA AGITATOR

35-FD-63

CONCENTRATES THICKENER FEED BOX

35-SM-63

FLOTATION CONCENTRATE FEED SAMPLER

35-PP-61A/B

CONCENTRATE THICKENER U/FLOW PUMP No.1 & 2

35-TH-61

FLOTATION CONCENTRATE THICKENER

35-PS-63

CONCENTRATE THICKENER AREA WASHDOWN PUMP

NOTE:
TO BE READ IN CONJUNCTION WITH 35\PI\0443

- NOTES:
- FOR TYPICAL INSTRUMENT DETAILS REFER TO DRG 30\PIV\0701
 - EXISTING BUTTERFLY VALVE NOT PART OF KCGM PROJECT.
 - FEEDBOX ON TOP OF CONCENTRATE THICKENER DOES NOT HAVE AN AGITATOR

LEGEND

EXISTING

NON-EXISTENT

STAGE 1 - NEW

STAGE 1 - REMOVE

STAGE 1 - DECOMMISSIONED (OTHERS)

STAGE 2 - NEW

STAGE 2 - REMOVE

STAGE 2 - DECOMMISSIONED (OTHERS)

DESCRIPTION

1 4SEP25 APPROVED FOR SP2 CONSTRUCTION

0 15APR25 APPROVED FOR SP1 CONSTRUCTION

REV DATE DESCRIPTION

FIMISTON PLANT CONCENTRATES FILTRATION CONCENTRATE THICKENER AREA PIPING AND INSTRUMENTATION DIAGRAM				DRAWING NO 2000-F35-PID-PR-10003				KCGM GROWTH PROJECT			
SCALE DRAWN CHECKED APPROVED PROJ APP DWG NO.				NTS				DRAWING NUMBER 35\PI\0702			
DATE 08/08/01 08/08/01 23/10/01				REV				REV			
KALGOORLIE CONSOLIDATED GOLD MINES PTY. LTD. ABN 09 377 619 003				B1				5			