


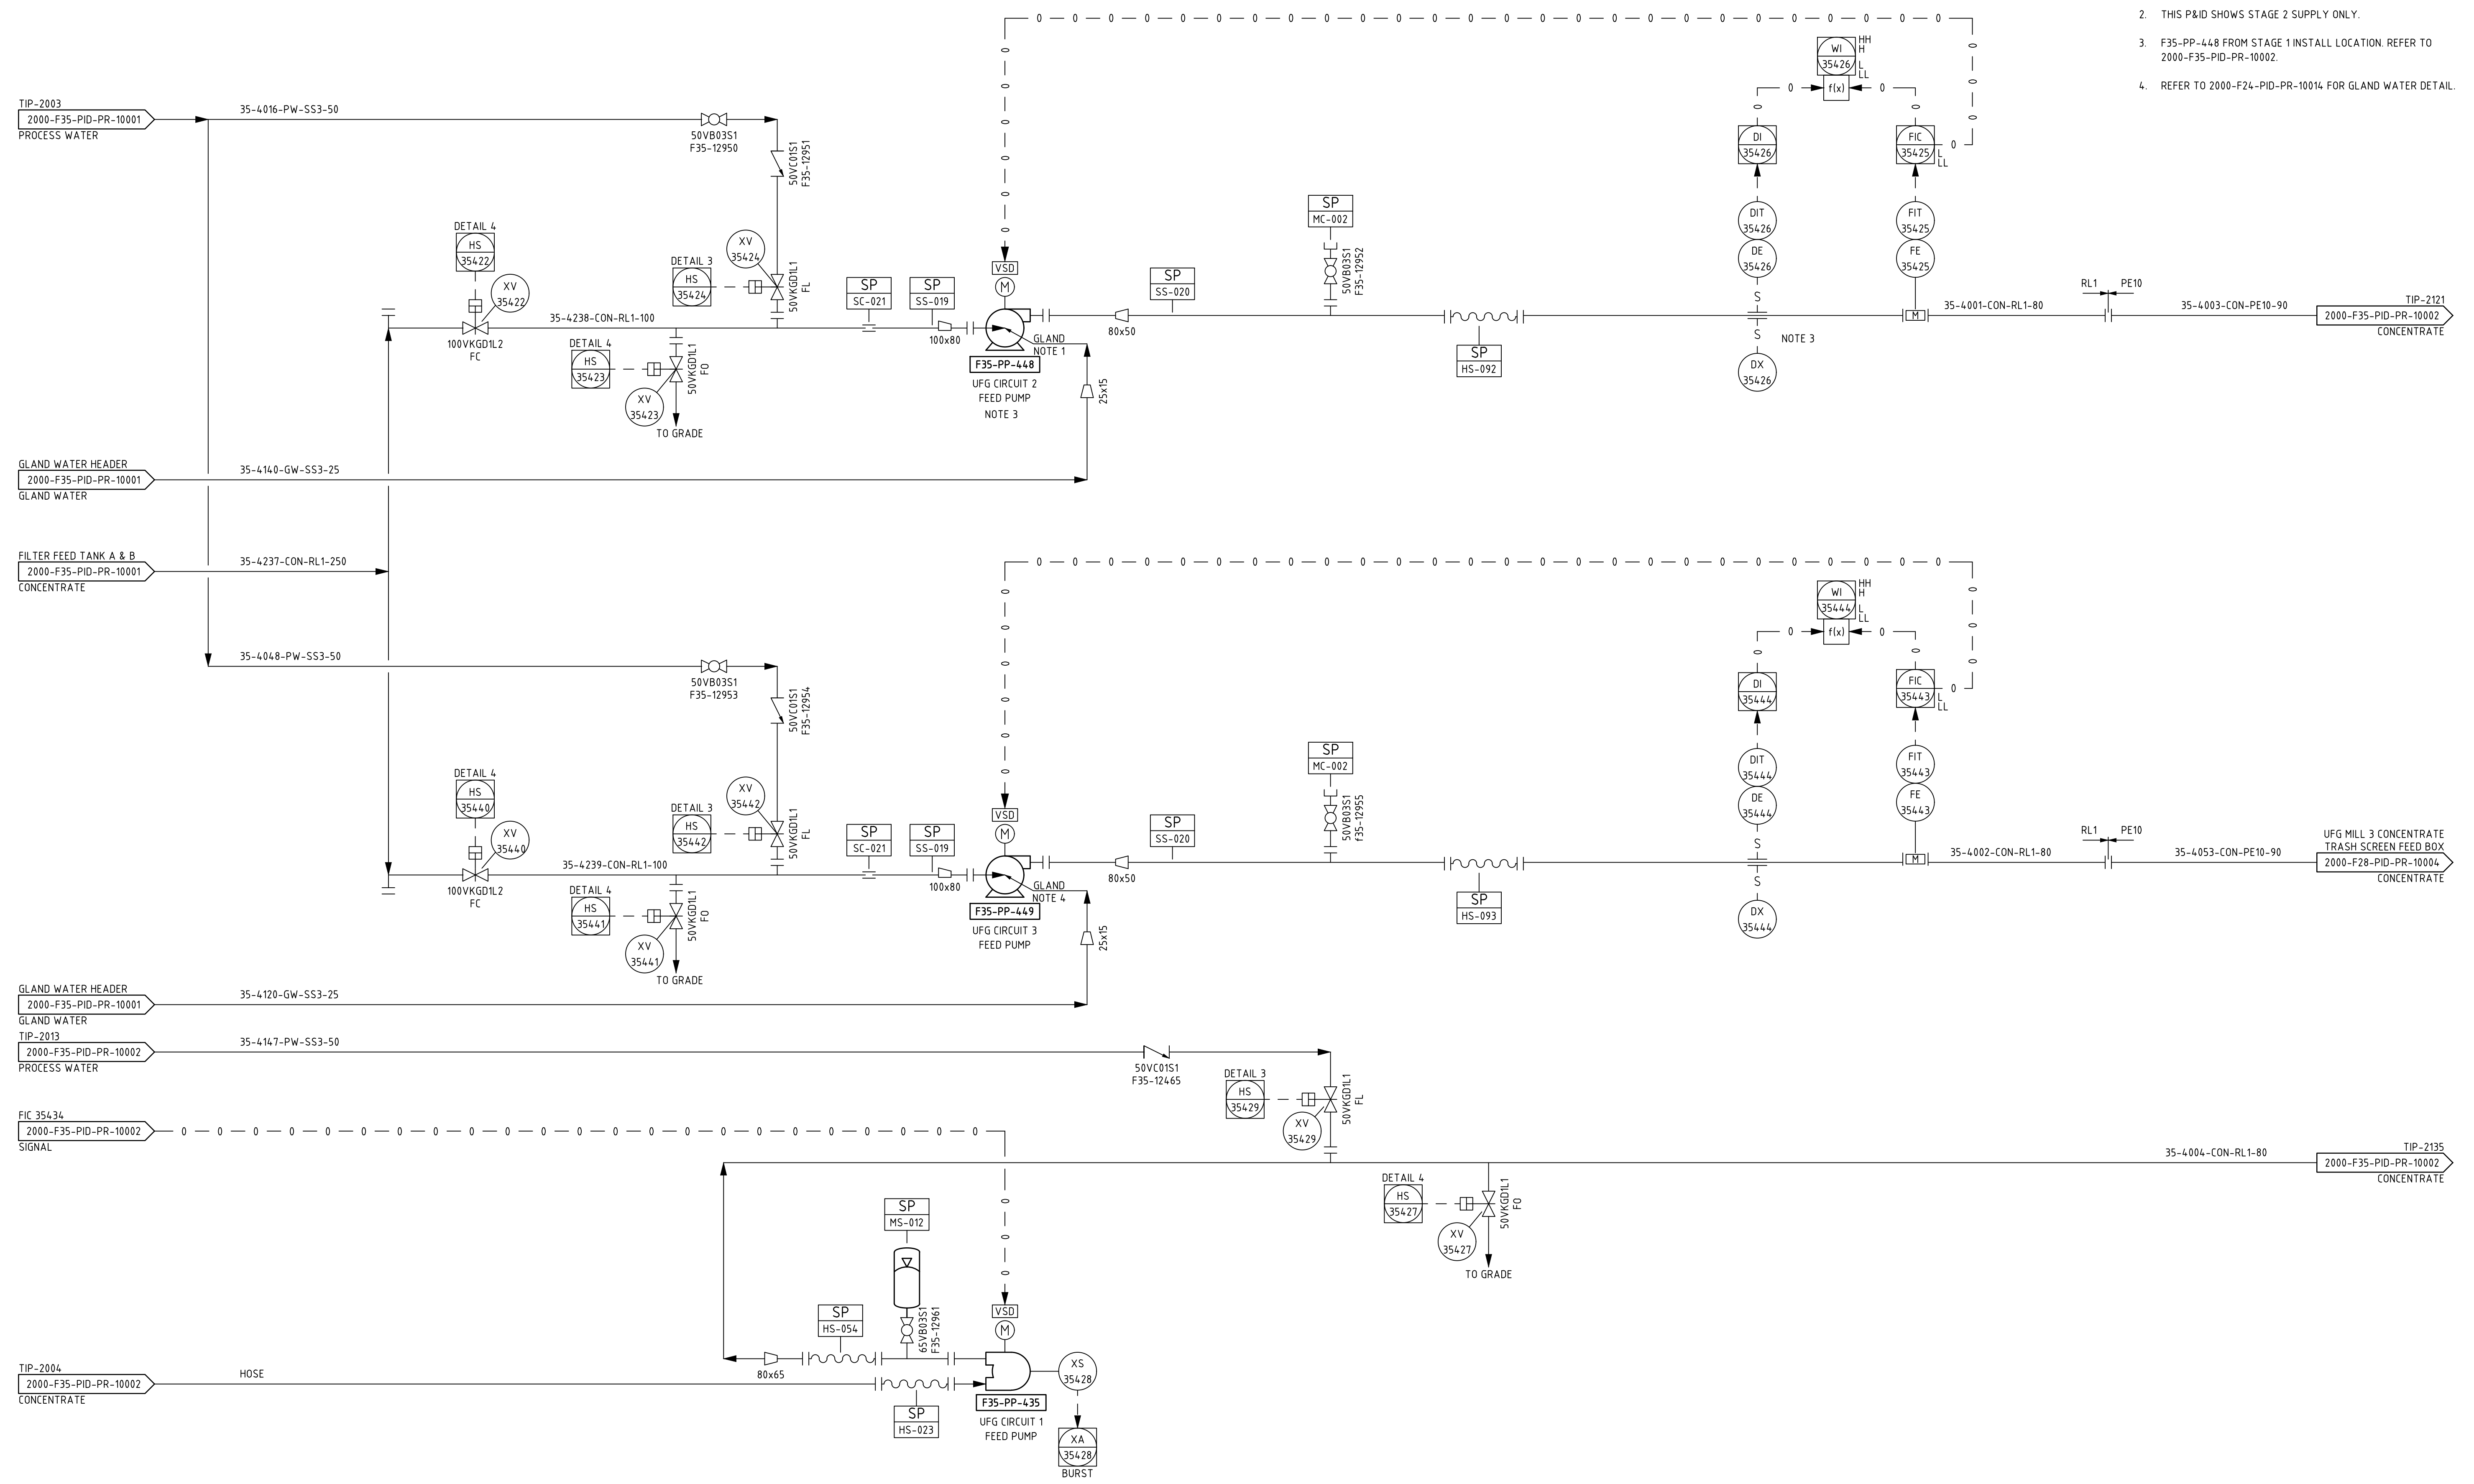

- NOTES:**
1. REFER TO 2000-F24-PID-PR-10003 FOR GLAND WATER DETAIL.
 2. THIS P&ID SHOWS STAGE 2 SUPPLY ONLY.
 3. F35-PP-448 FROM STAGE 1 INSTALL LOCATION. REFER TO 2000-F35-PID-PR-10002.
 4. REFER TO 2000-F24-PID-PR-10014 FOR GLAND WATER DETAIL.

[illegible]