


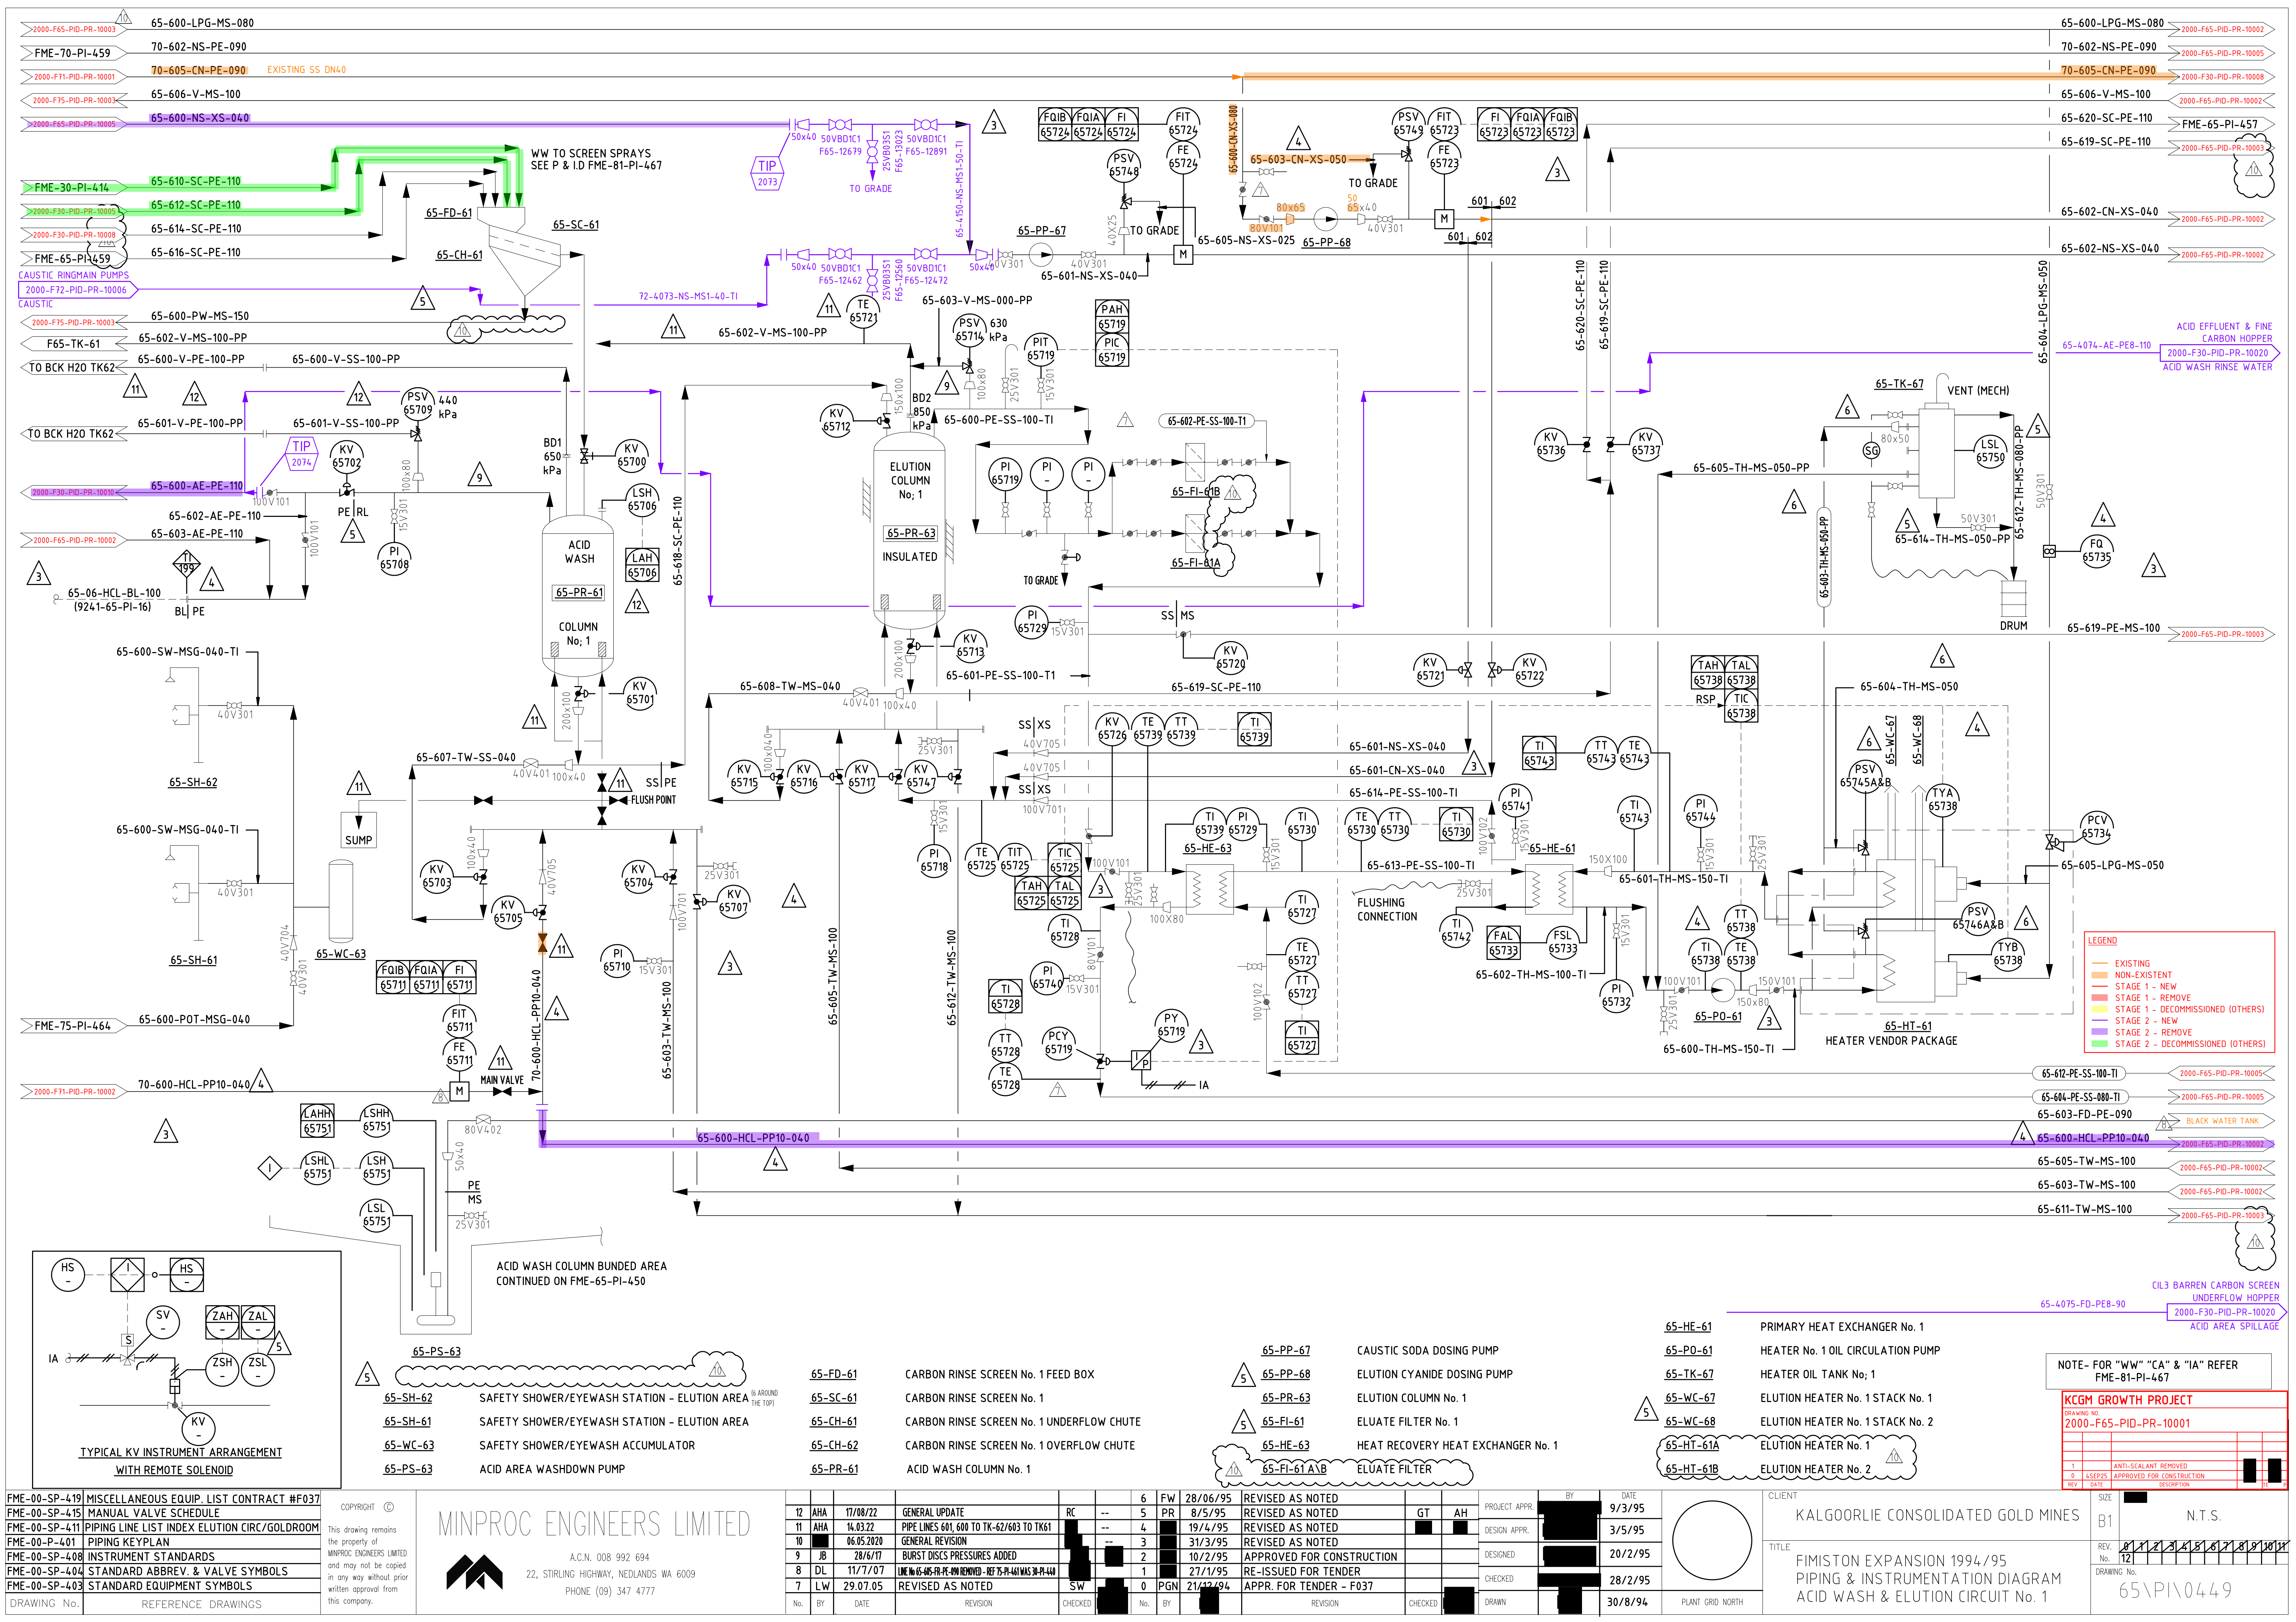

FME-00-SP-419	MISCELLANEOUS EQUIP. LIST CONTRACT #F037
FME-00-SP-415	MANUAL VALVE SCHEDULE
FME-00-SP-411	PIPING LINE LIST INDEX ELUTION CIRC/GOLDROOM
FME-00-P-401	PIPING KEYPLAN
FME-00-SP-408	INSTRUMENT STANDARDS
FME-00-SP-404	STANDARD ABBREV. & VALVE SYMBOLS
FME-00-SP-403	STANDARD EQUIPMENT SYMBOLS
DRAWING No.	REFERENCE DRAWINGS

COPYRIGHT ©
this drawing remains
the property of
MINPROC ENGINEERS LIMITED
and may not be copied
in any way without prior
written approval from
this company.



MINPROC ENGINEERS LIMITED
A.C.N. 008 992 694
22, STIRLING HIGHWAY, NEDLANDS WA 6009
PHONE (09) 347 4777

65-PS-63
ACID AREA WASHDOWN PUMP

65-SH-62
SAFETY SHOWER/EYEWASH STATION - ELUTION AREA (IS AROUND THE TOP)

65-SH-61
SAFETY SHOWER/EYEWASH STATION - ELUTION AREA

65-WC-63
SAFETY SHOWER/EYEWASH ACCUMULATOR

65-FD-61	CARBON RINSE SCREEN No. 1 FEED BOX
65-SC-61	CARBON RINSE SCREEN No. 1
65-CH-61	CARBON RINSE SCREEN No. 1 UNDERFLOW CHUTE
65-CH-62	CARBON RINSE SCREEN No. 1 OVERFLOW CHUTE
65-PR-61	ACID WASH COLUMN No. 1

65-PP-67	CAUSTIC SODA DOSING PUMP
65-PP-68	ELUTION CYANIDE DOSING PUMP
65-PR-63	ELUTION COLUMN No. 1
65-FI-61	ELUATE FILTER No. 1
65-HE-63	HEAT RECOVERY HEAT EXCHANGER No. 1
65-FI-61A/B	ELUATE FILTER

65-HE-61	PRIMARY HEAT EXCHANGER No. 1
65-PO-61	HEATER No. 1 OIL CIRCULATION PUMP
65-TK-67	HEATER OIL TANK No. 1
65-WC-67	ELUTION HEATER No. 1 STACK No. 1
65-WC-68	ELUTION HEATER No. 1 STACK No. 2
65-HT-61A	ELUTION HEATER No. 1
65-HT-61B	ELUTION HEATER No. 2

NOTE- FOR "WW" "CA" & "IA" REFER
FME-81-PI-467

KCGM GROWTH PROJECT			
DRAWING NO.	2000-F65-PID-PR-10001	DATE	30/8/94
REV	DATE	DESCRIPTION	
1		ANTI-SALANT REMOVED	
2		APPROVED FOR CONSTRUCTION	

12	AHA	17/08/22	GENERAL UPDATE	RC	--	5	FW	28/06/95	REVISED AS NOTED			PROJECT APPR.	BY	DATE	9/3/95
11	AHA	14.03.22	PIPE LINES 601, 600 TO TK-62/603 TO TK61	--	--	4	PR	8/5/95	REVISED AS NOTED	GT	AH	DESIGN APPR.		3/5/95	
10		06.05.2020	GENERAL REVISION		--	3		31/3/95	REVISED AS NOTED			DESIGNED		20/2/95	
9	JB	28/6/17	BURST DISCS PRESSURES ADDED			2		10/2/95	APPROVED FOR CONSTRUCTION			CHECKED		28/2/95	
8	DL	11/7/07	LINE No 65-405-FR-PR-100010002 - REF 75-PI-441 WAS 30-PI-440			1		27/1/95	RE-ISSUED FOR TENDER						
7	LW	29.07.05	REVISED AS NOTED	SW		0	PGN	21/12/94	APPR. FOR TENDER - F037					30/8/94	
No.	BY	DATE	REVISION	CHECKED		No.	BY		REVISION	CHECKED		DRAWN			



PLANT GRID NORTH

CLIENT
KALGOORLIE CONSOLIDATED GOLD MINES

TITLE
**FIMISTON EXPANSION 1994/95
PIPING & INSTRUMENTATION DIAGRAM
ACID WASH & ELUTION CIRCUIT No. 1**

REV. No. 12

DRAWING No. 65\PI\0449

N.T.S.