



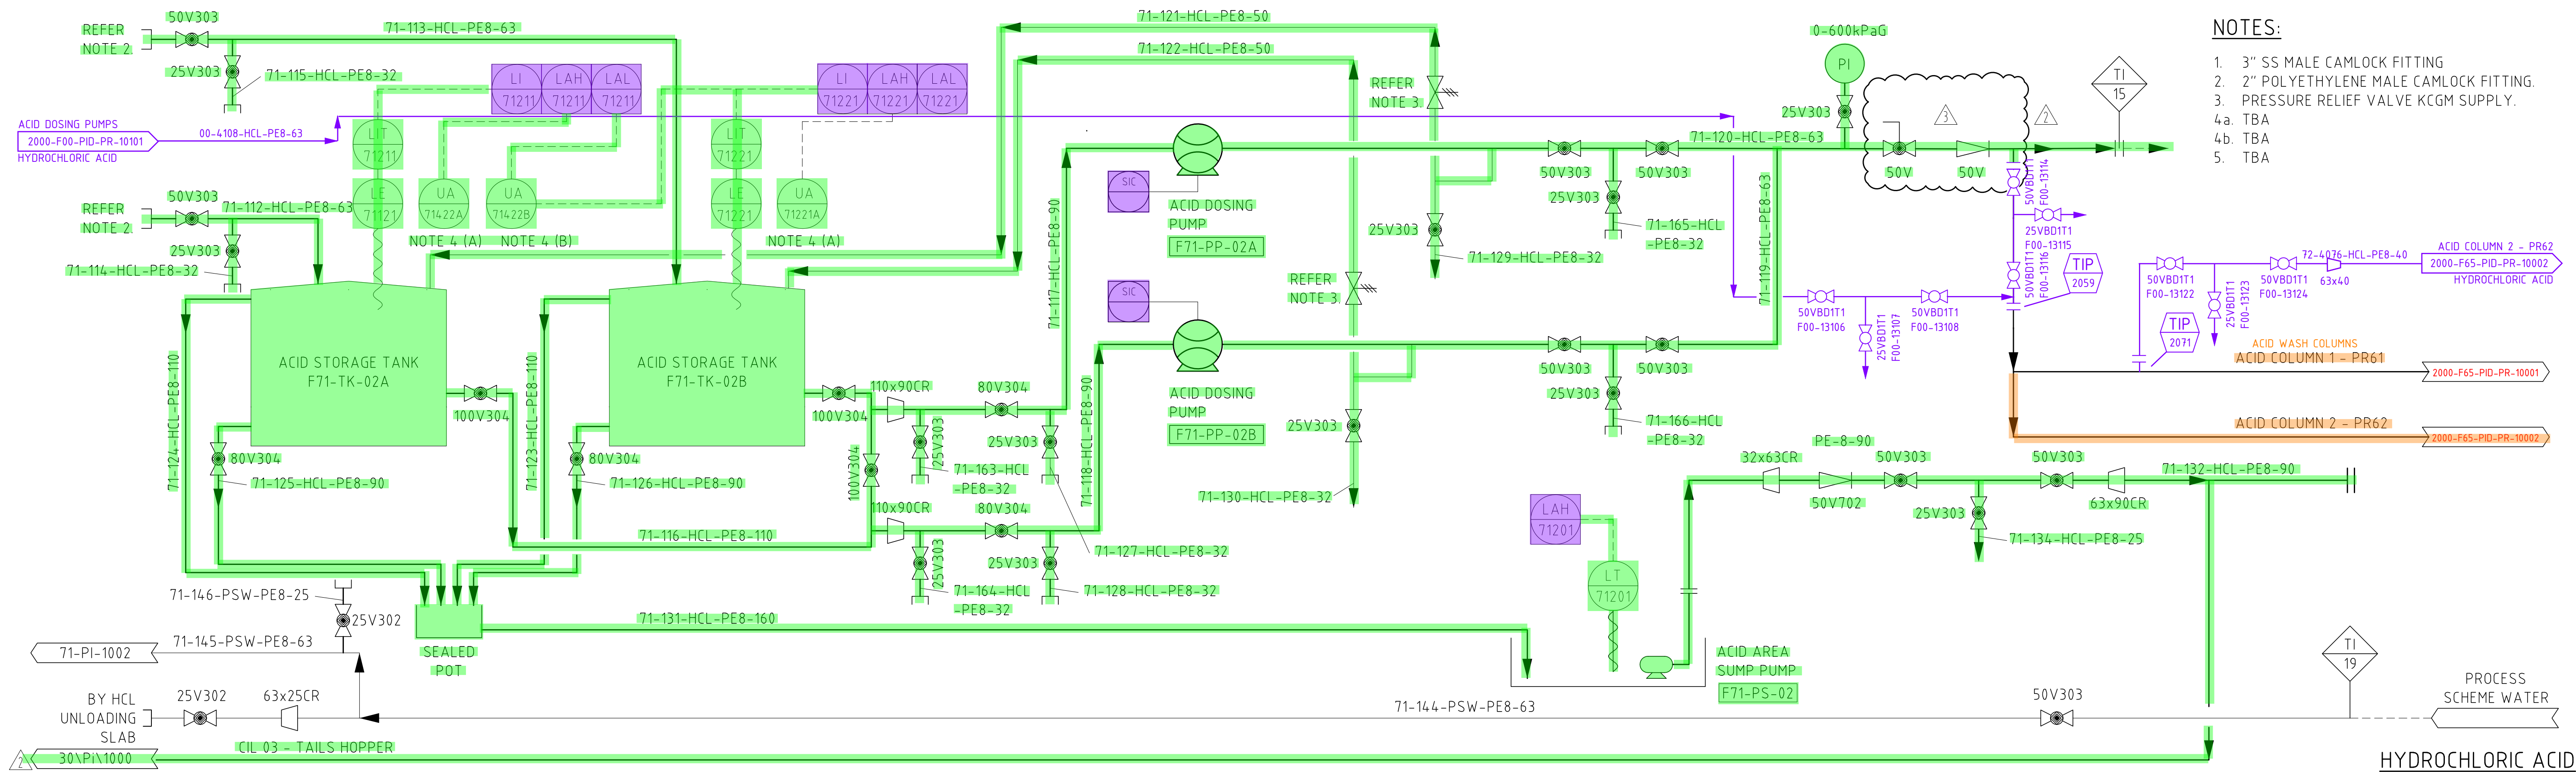

- NOTES:
- 3" SS MALE CAMLOCK FITTING
 - 2" POLYETHYLENE MALE CAMLOCK FITTING
 - PRESSURE RELIEF VALVE KCGM SUPPLY.
 - TBA
 - TBA

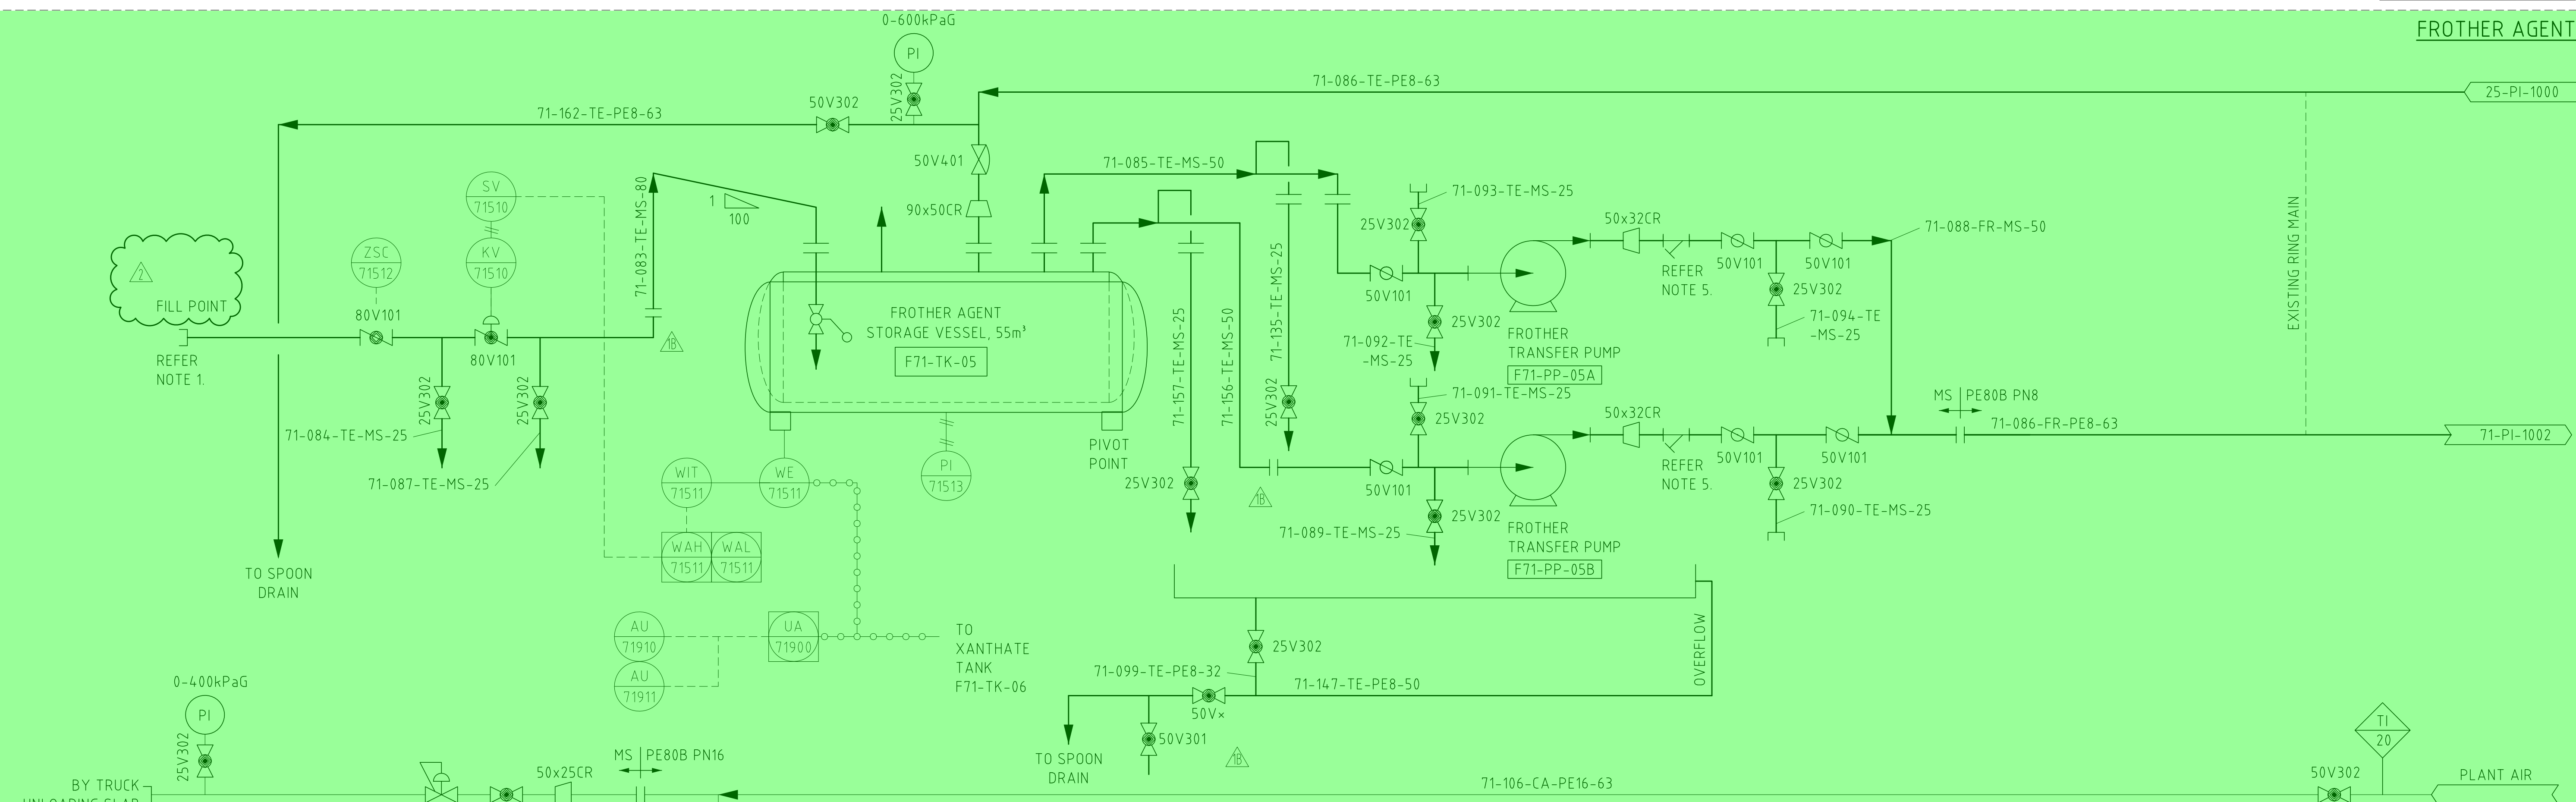

NOTE:
× DENOTES POLY VALVES

LEGEND

- EXISTING
- NON-EXISTENT
- STAGE 1 - NEW
- STAGE 1 - REMOVE
- STAGE 1 - DECOMMISSIONED (OTHERS)
- STAGE 2 - NEW
- STAGE 2 - REMOVE
- STAGE 2 - DECOMMISSIONED (OTHERS)

KCGM GROWTH PROJECT

DRAWING NO.
2000-F71-PID-PR-10002

REV	DATE	APPROVED FOR CONSTRUCTION	DESCRIPTION
0	22SEP25	APPROVED FOR CONSTRUCTION	

--	--	