


D:\CAD PROJECTS\235 NORTHERN STAR RESOURCES LTD\23517 KCGM GROWTH PROJECT\03 DELIVERABLES\PRP\PID\ISSUED\12.09.25 - SIGNING\NATIVES\2000-F72-PID-PR-10012\_1.DWG 09SEP25 8:47AM ANNE.HOYNE

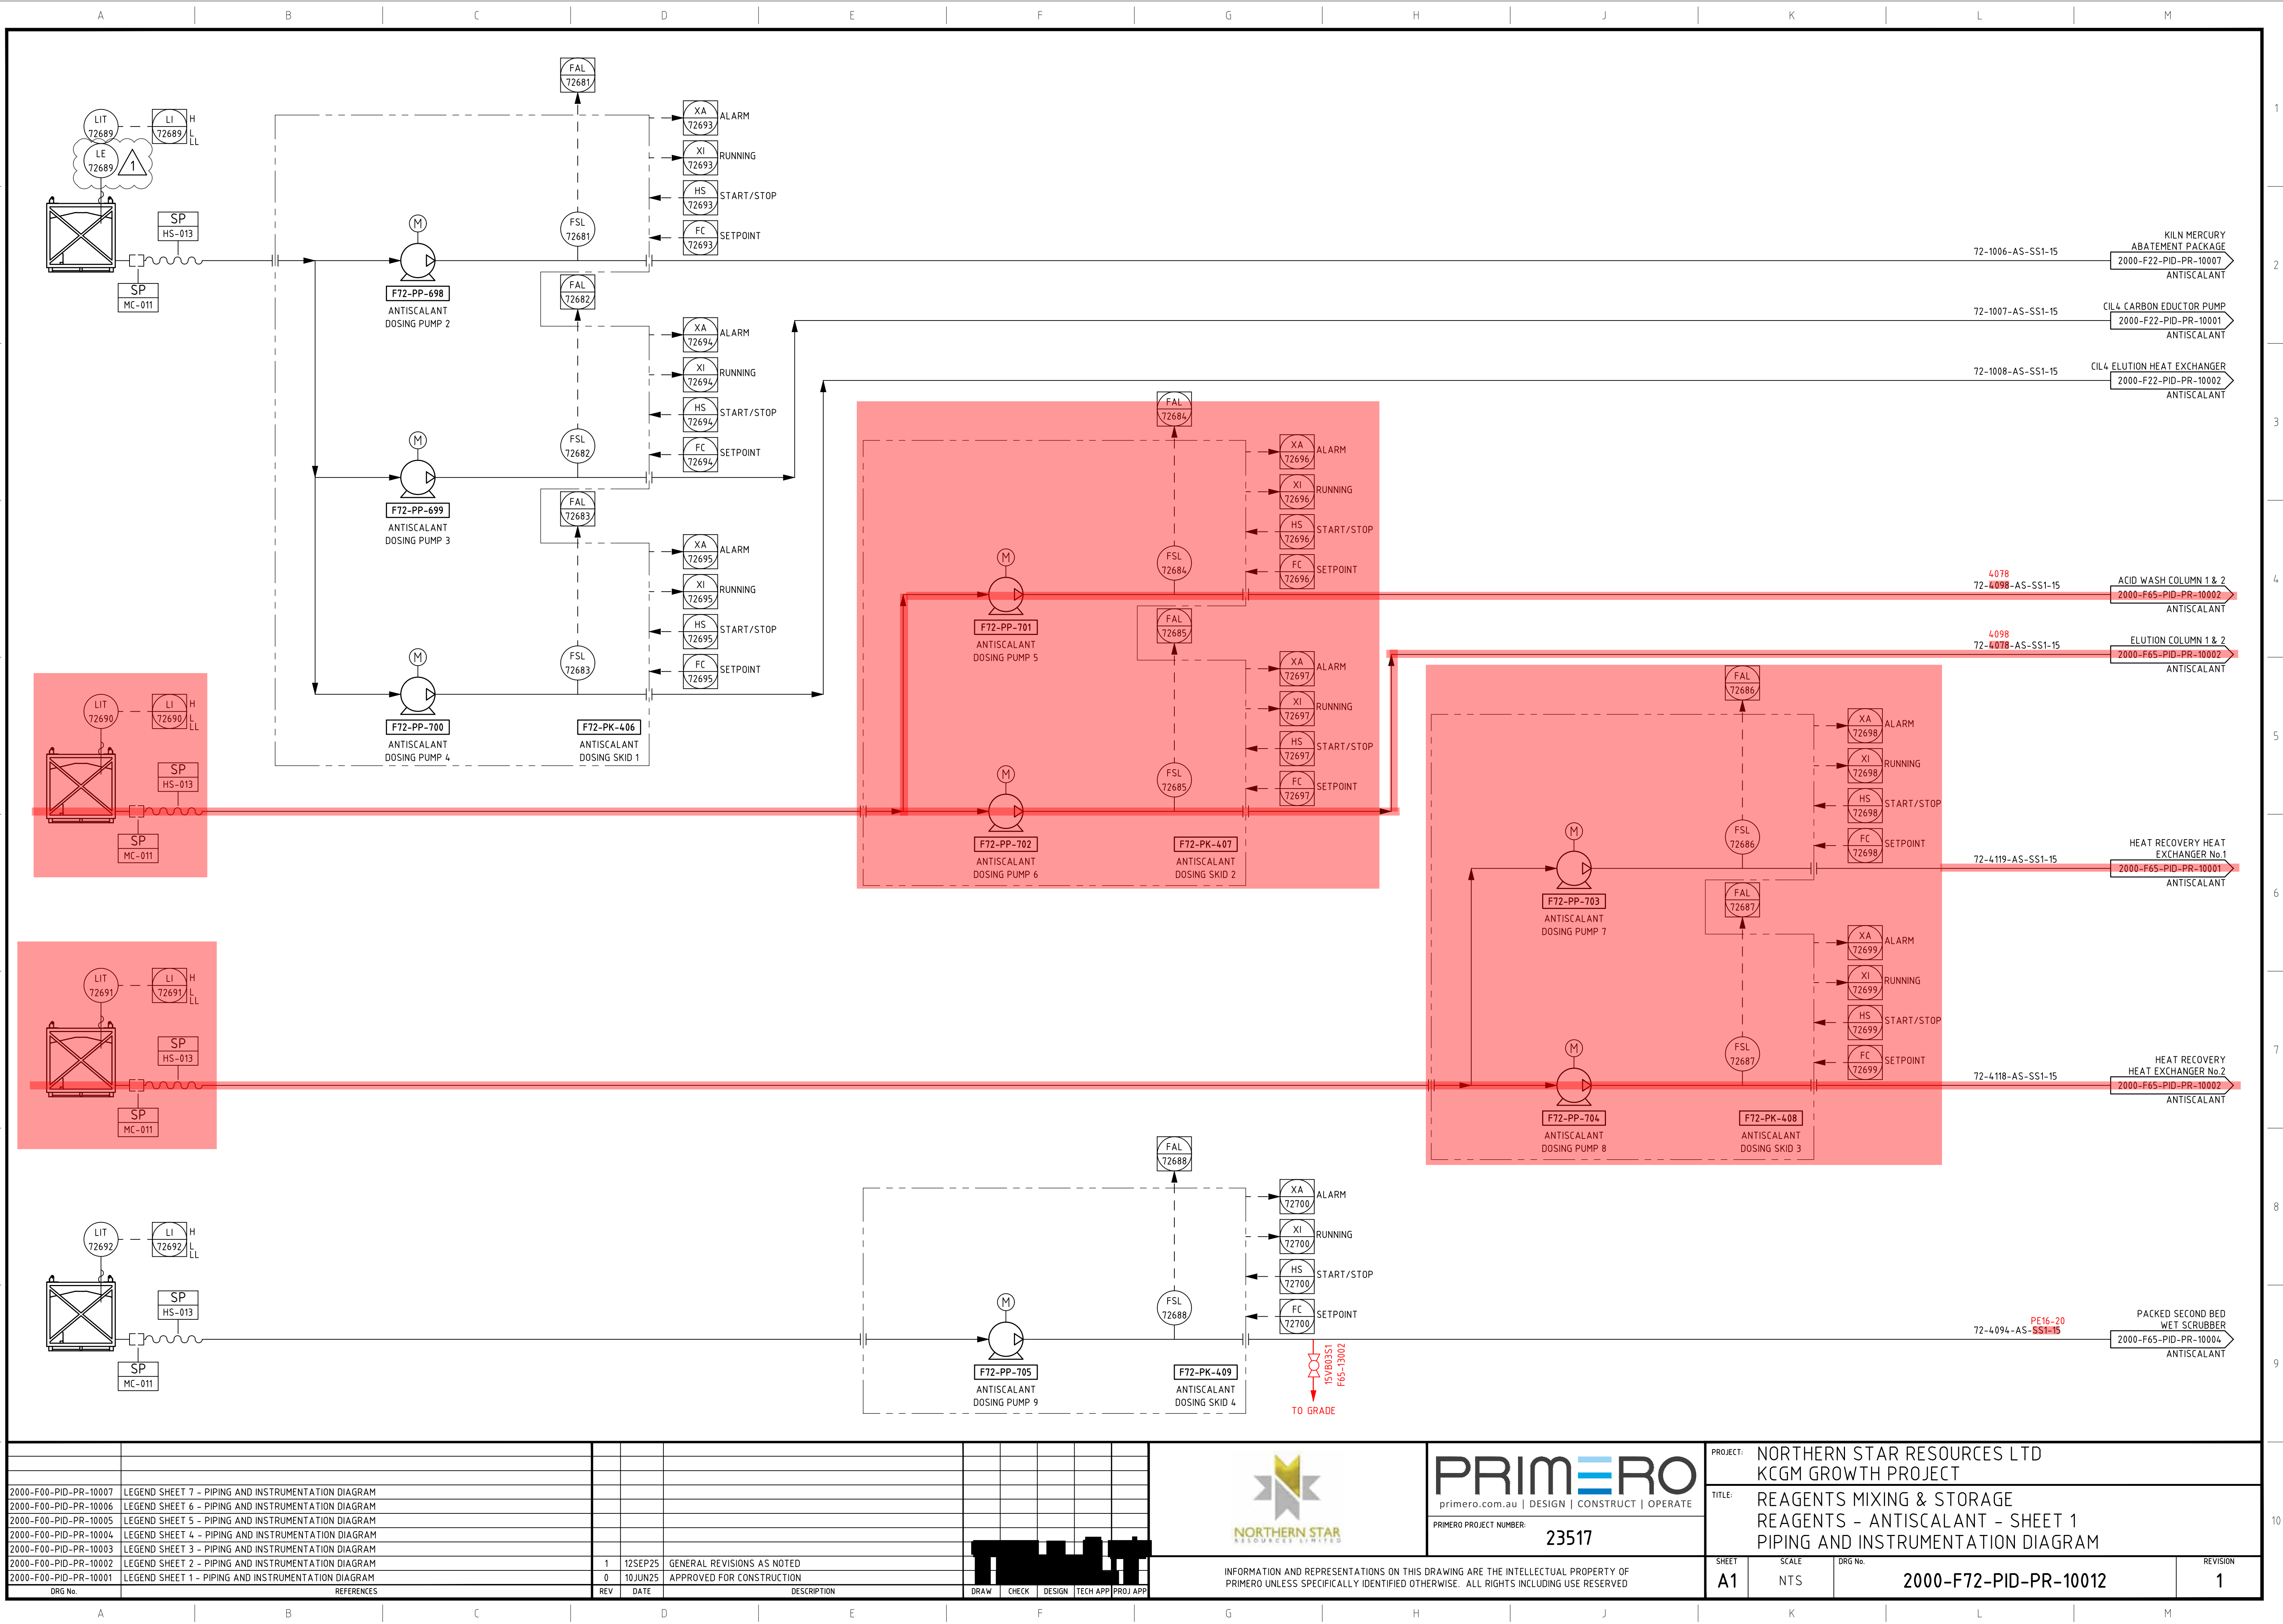

| REV | DATE    | DESCRIPTION                | DRAW | CHECK | DESIGN | TECH APP | PROJ APP |
|-----|---------|----------------------------|------|-------|--------|----------|----------|
| 1   | 12SEP25 | GENERAL REVISIONS AS NOTED |      |       |        |          |          |
| 0   | 10JUN25 | APPROVED FOR CONSTRUCTION  |      |       |        |          |          |

|                       |                                                     |
|-----------------------|-----------------------------------------------------|
| 2000-F00-PID-PR-10007 | LEGEND SHEET 7 - PIPING AND INSTRUMENTATION DIAGRAM |
| 2000-F00-PID-PR-10006 | LEGEND SHEET 6 - PIPING AND INSTRUMENTATION DIAGRAM |
| 2000-F00-PID-PR-10005 | LEGEND SHEET 5 - PIPING AND INSTRUMENTATION DIAGRAM |
| 2000-F00-PID-PR-10004 | LEGEND SHEET 4 - PIPING AND INSTRUMENTATION DIAGRAM |
| 2000-F00-PID-PR-10003 | LEGEND SHEET 3 - PIPING AND INSTRUMENTATION DIAGRAM |
| 2000-F00-PID-PR-10002 | LEGEND SHEET 2 - PIPING AND INSTRUMENTATION DIAGRAM |
| 2000-F00-PID-PR-10001 | LEGEND SHEET 1 - PIPING AND INSTRUMENTATION DIAGRAM |

|         |            |
|---------|------------|
| DRG No. | REFERENCES |
|         |            |



**PRIMERO**  
primero.com.au | DESIGN | CONSTRUCT | OPERATE  
PRIMERO PROJECT NUMBER: 23517

INFORMATION AND REPRESENTATIONS ON THIS DRAWING ARE THE INTELLECTUAL PROPERTY OF PRIMERO UNLESS SPECIFICALLY IDENTIFIED OTHERWISE. ALL RIGHTS INCLUDING USE RESERVED

|          |   |                       |          |
|----------|---|-----------------------|----------|
| PROJECT: | NORTHERN STAR RESOURCES LTD<br>KCGM GROWTH PROJECT                                                  |                       |          |
| TITLE:   | REAGENTS MIXING & STORAGE<br>REAGENTS - ANTISCALANT - SHEET 1<br>PIPING AND INSTRUMENTATION DIAGRAM |                       |          |
| SHEET    | SCALE                                                                                               | DRG No.               | REVISION |
| A1       | NTS                                                                                                 | 2000-F72-PID-PR-10012 | 1        |