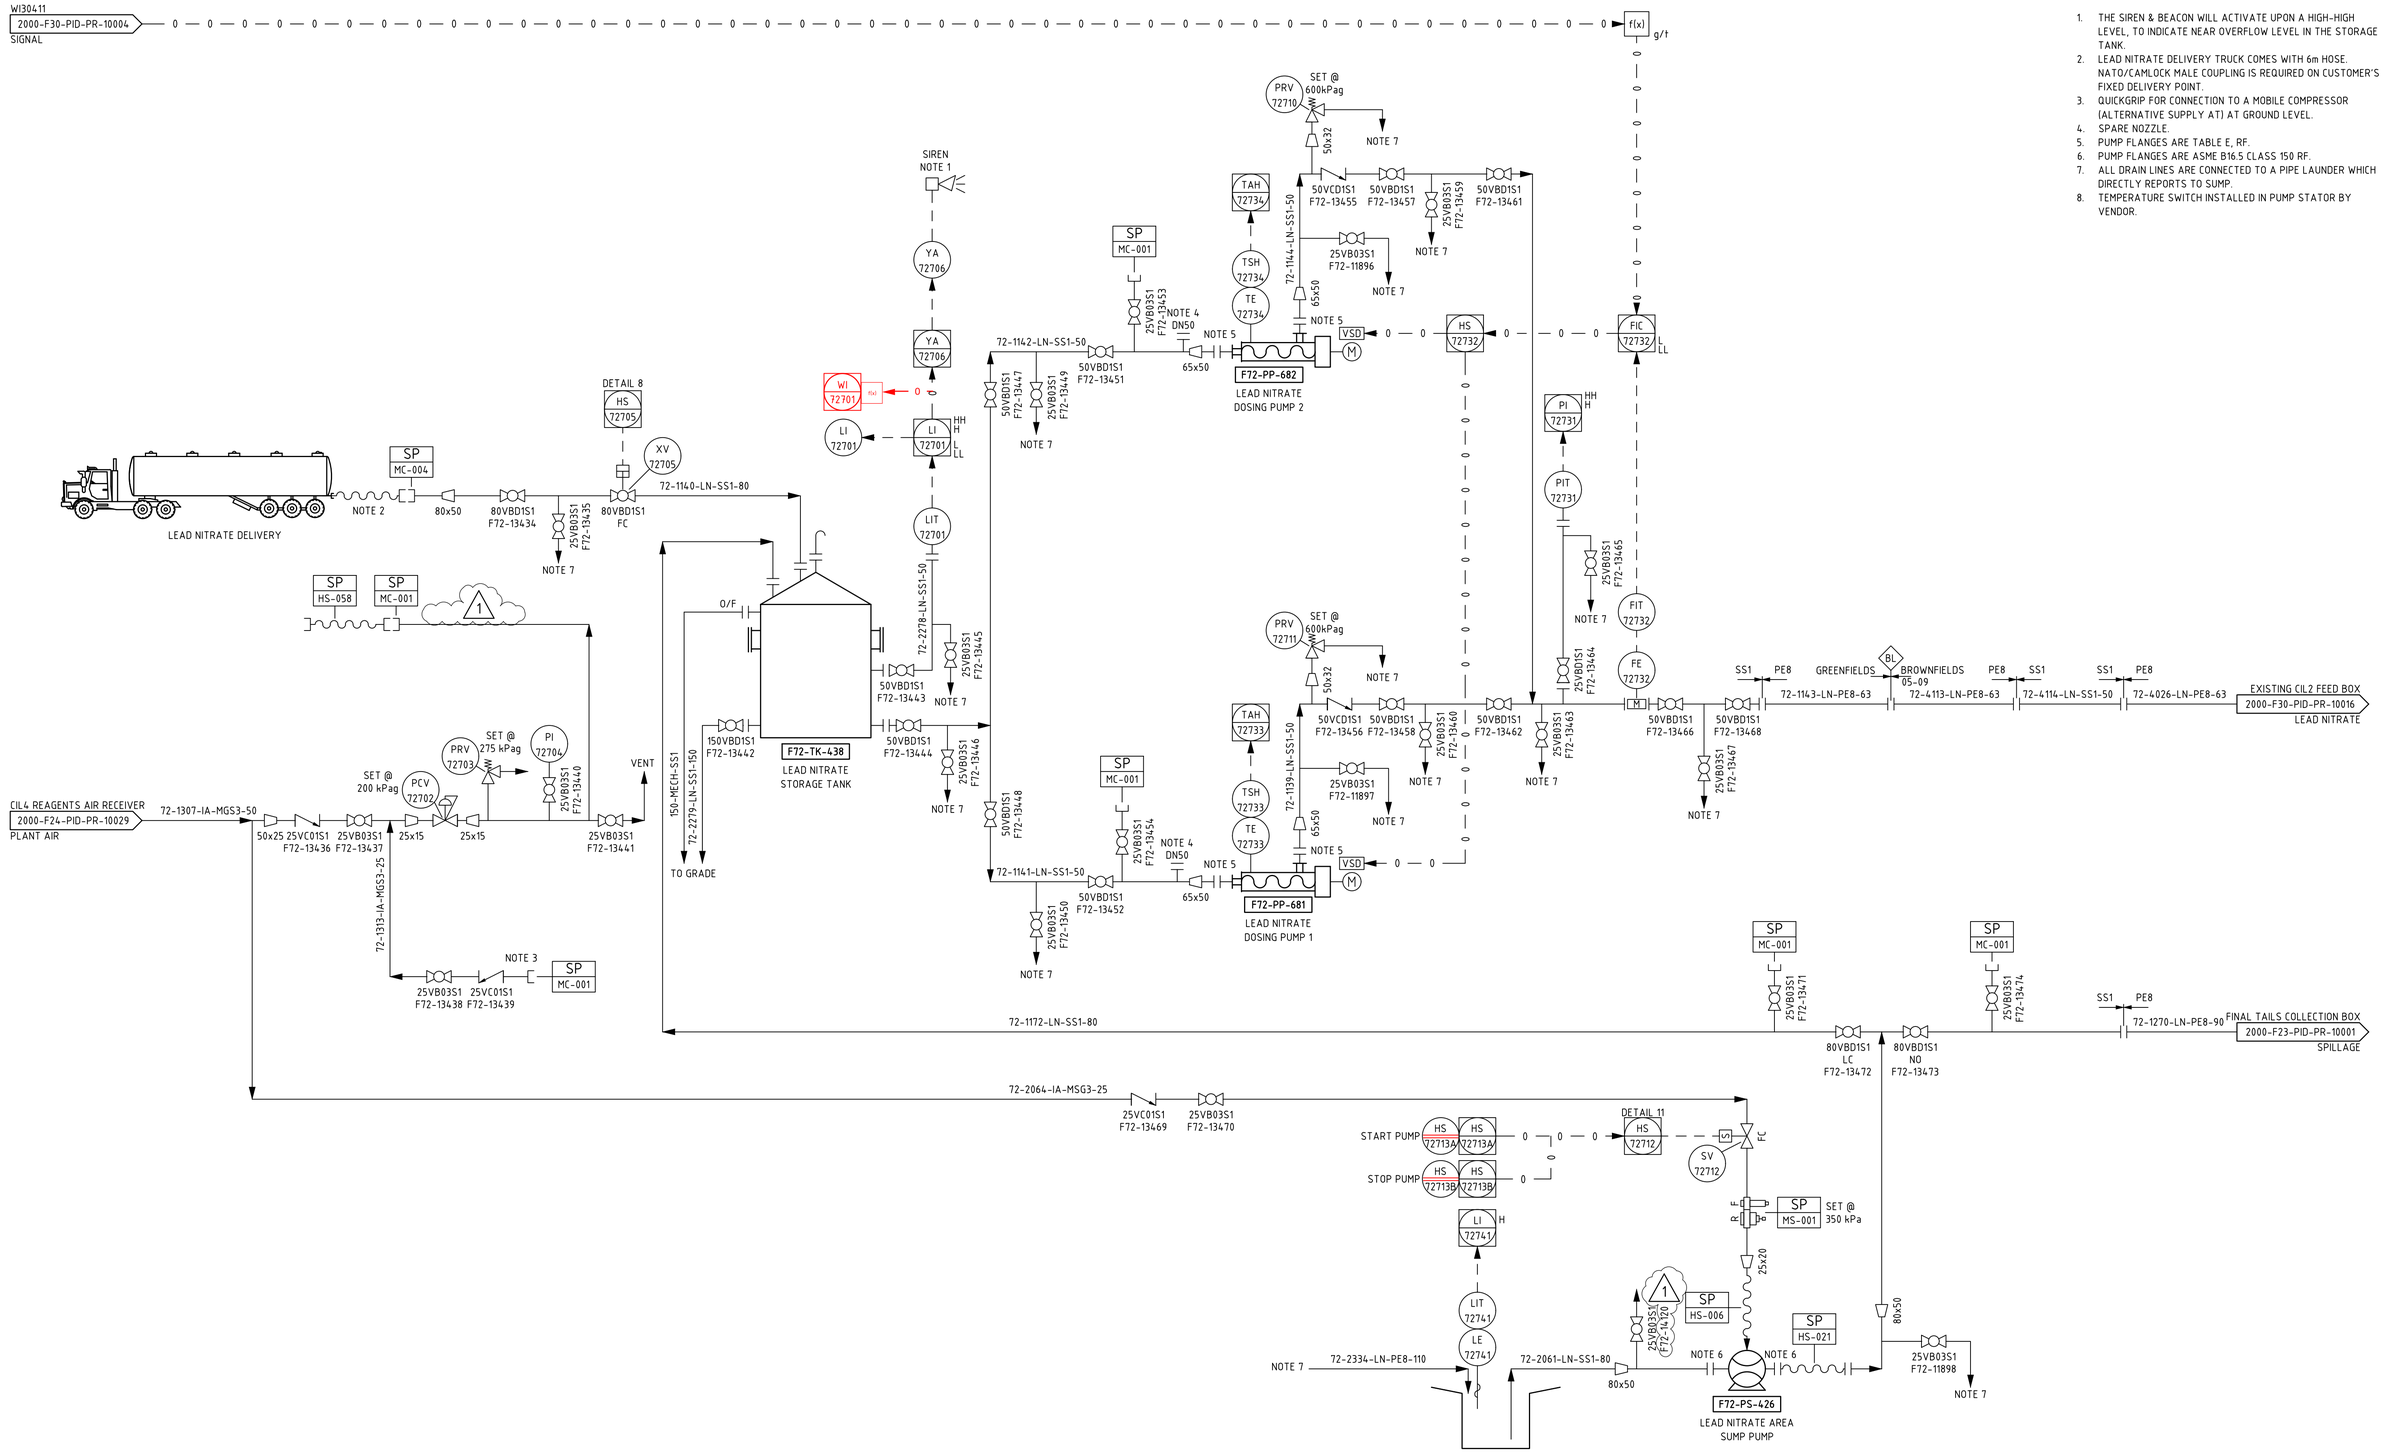


NOTES:

1. THE SIREN & BEACON WILL ACTIVATE UPON A HIGH-HIGH LEVEL, TO INDICATE NEAR OVERFLOW LEVEL IN THE STORAGE TANK.
2. LEAD NITRATE DELIVERY TRUCK COMES WITH 6m HOSE. NATO/CAMLOCK MALE COUPLING IS REQUIRED ON CUSTOMER'S FIXED DELIVERY POINT.
3. QUICKGRIP FOR CONNECTION TO A MOBILE COMPRESSOR (ALTERNATIVE SUPPLY AT) AT GROUND LEVEL.
4. SPARE NOZZLE.
5. PUMP FLANGES ARE TABLE E, RF.
6. PUMP FLANGES ARE ASME B16.5 CLASS 150 RF.
7. ALL DRAIN LINES ARE CONNECTED TO A PIPE LAUNDER WHICH DIRECTLY REPORTS TO SUMP.
8. TEMPERATURE SWITCH INSTALLED IN PUMP STATOR BY VENDOR.

DRG No.	REFERENCES	REV	DATE	DESCRIPTION	DRAW	CHECK	DESIGN	TECH APP	PROJ APP
2000-F00-PID-PR-10007	LEGEND SHEET 7 - PIPING AND INSTRUMENTATION DIAGRAM								
2000-F00-PID-PR-10006	LEGEND SHEET 6 - PIPING AND INSTRUMENTATION DIAGRAM								
2000-F00-PID-PR-10005	LEGEND SHEET 5 - PIPING AND INSTRUMENTATION DIAGRAM								
2000-F00-PID-PR-10004	LEGEND SHEET 4 - PIPING AND INSTRUMENTATION DIAGRAM								
2000-F00-PID-PR-10003	LEGEND SHEET 3 - PIPING AND INSTRUMENTATION DIAGRAM								
2000-F00-PID-PR-10002	LEGEND SHEET 2 - PIPING AND INSTRUMENTATION DIAGRAM	1	12SEP25	GENERAL REVISIONS AS NOTED					
2000-F00-PID-PR-10001	LEGEND SHEET 1 - PIPING AND INSTRUMENTATION DIAGRAM	0	10JUN25	APPROVED FOR CONSTRUCTION					

NORTHERN STAR RESOURCES LIMITED

INFORMATION AND REPRESENTATIONS ON THIS DRAWING ARE THE INTELLECTUAL PROPERTY OF PRIMERO UNLESS SPECIFICALLY IDENTIFIED OTHERWISE. ALL RIGHTS INCLUDING USE RESERVED

PRIMERO
primero.com.au | DESIGN | CONSTRUCT | OPERATE

PRIMERO PROJECT NUMBER: 23517

PROJECT: NORTHERN STAR RESOURCES LTD
KCGM GROWTH PROJECT

TITLE: REAGENTS MIXING & STORAGE
REAGENTS - LEAD NITRATE
PIPING AND INSTRUMENTATION DIAGRAM

SHEET	SCALE	DRG No.	REVISION
A1	NTS	2000-F72-PID-PR-10015	1

O:\CAD PROJECTS\235 NORTHERN STAR RESOURCES LTD\23517 KCGM GROWTH PROJECT\03 DELIVERABLES\PRI\PID\ISSUED\12 09 25 - SIGNING\NATIVES\2000-F72-PID-PR-10015_1.DWG 09SEP25 3:32PM ANNE.HOYNE