


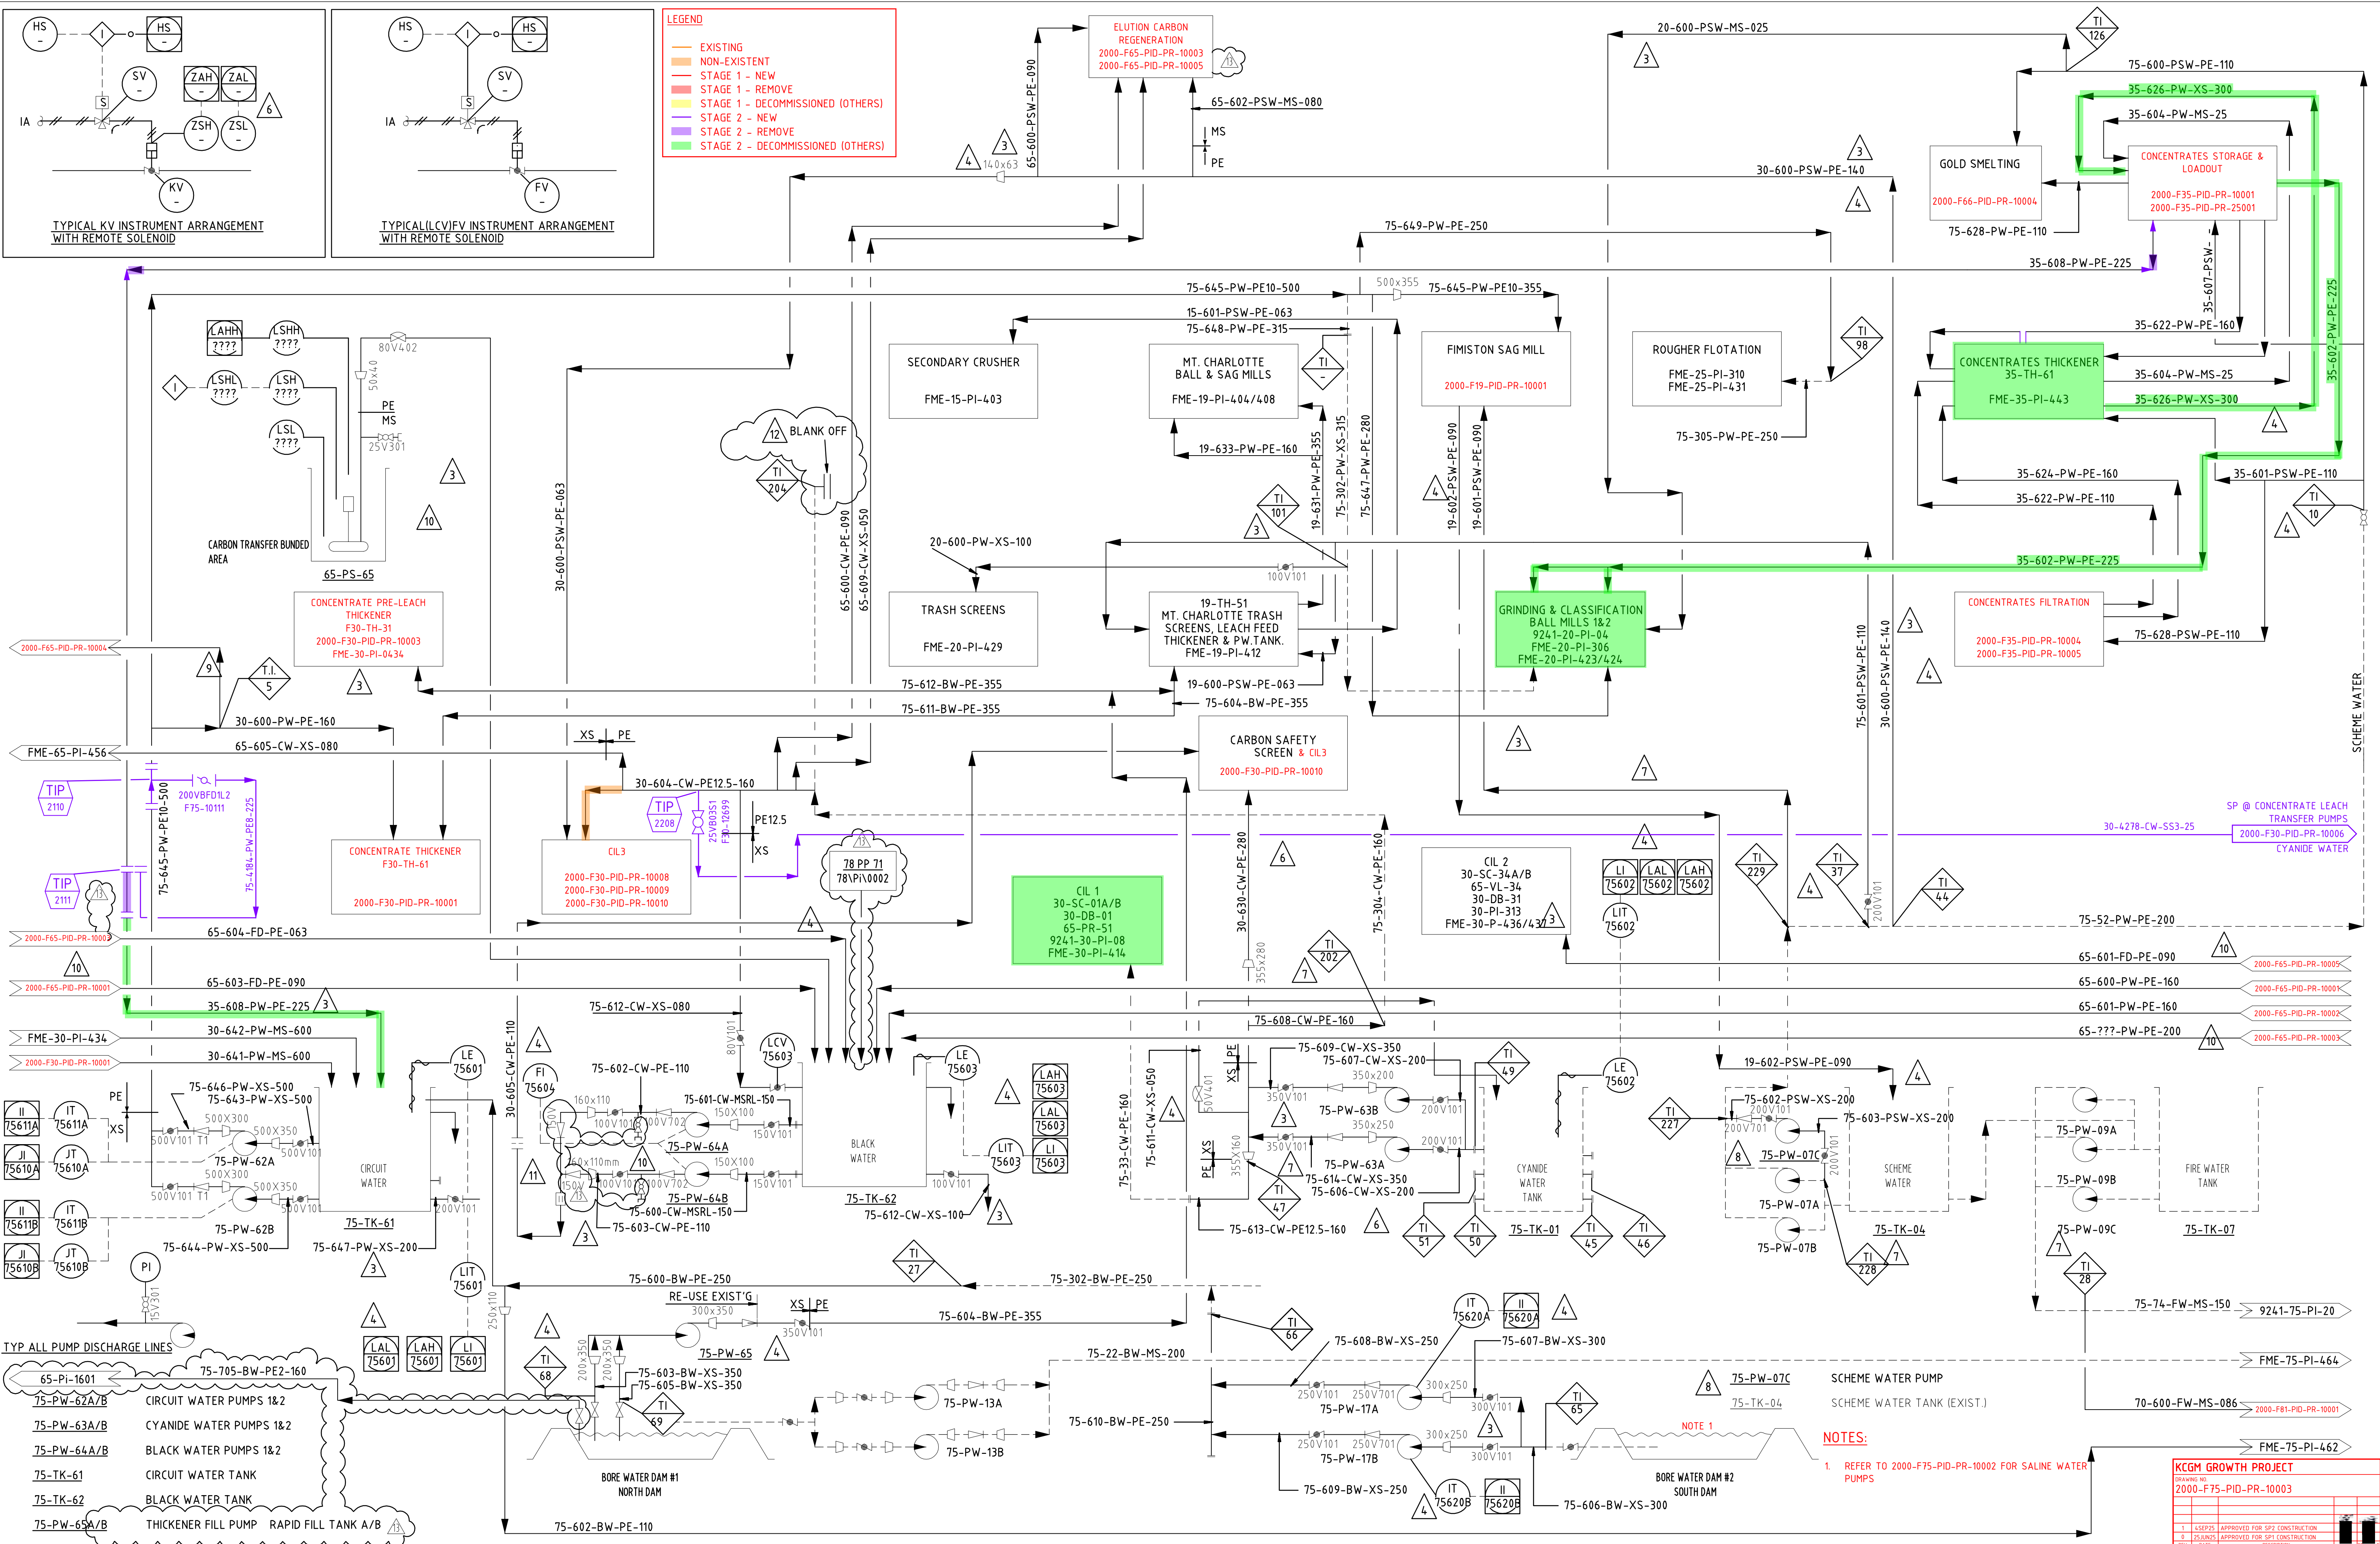

FME-00-SP-403 STANDARD EQUIPMENT SYMBOLS		COPYRIGHT ©		MINPROC ENGINEERS LIMITED		13 LW 01/04/2020 REV'D AS NOTED. VALVE & F/M ADDED		TR -		6 PR 8/5/95		REVISED AS NOTED		GT AH		PROJECT APPR.		BY		DATE		CLIENT		SIZE	
FME-00-SP-404 ABBREVIATIONS & VALVE SYMBOLS		This drawing remains the property of MINPROC ENGINEERS LIMITED and may not be copied in any way without prior written approval from this company.		A/CN 008 992 694		12 JB 28/1/14		5 PR 21/4/95		4 PR 20/4/95		APPROVED FOR CONSTRUCTION F-035		DESIGN APPR.		BY		DATE		10/3/95		KALGOORLIE CONSOLIDATED GOLD MINES		B1	
FME-00-SP-408 INSTRUMENT STANDARDS				22, STIRLING HIGHWAY, NEOLANDS WA 6009		11 RH 29/9/11		3 30/03/95		3 30/03/95		REVISED AS NOTED F-037		DESIGNED				20/2/95		23/2/95		FIMISTON EXPANSION 1994/95 PIPING & INSTRUMENT DIAGRAM WATER MANAGEMENT		N.T.S.	
FME-75-PI-321 STAGE 2 WATER MANAGEMENT P&ID				PHONE (09) 347 4777		10 11/7/07		2 17/03/95		1 10/2/95		APPROVED FOR TENDER F-035		CHECKED				05-10-94						REV	
9241-75-PI-20 STAGE 1 WATER MANAGEMENT P&ID						9 18/07/06		1 27/1/95		0 27/1/95		APPROVED FOR CONSTRUCTION		DRAWN										DATE	
9241-00-PI-23 STAGE 1 WASHDOWN WATER P&ID						8 28/06/95		1 10/2/95		0 27/1/95		APPROVED FOR TENDER												DESCRIPTION	
DRAWING No.		REFERENCE DRAWINGS				7 9/6/95		0 27/1/95																FME-75-PI-0461	