


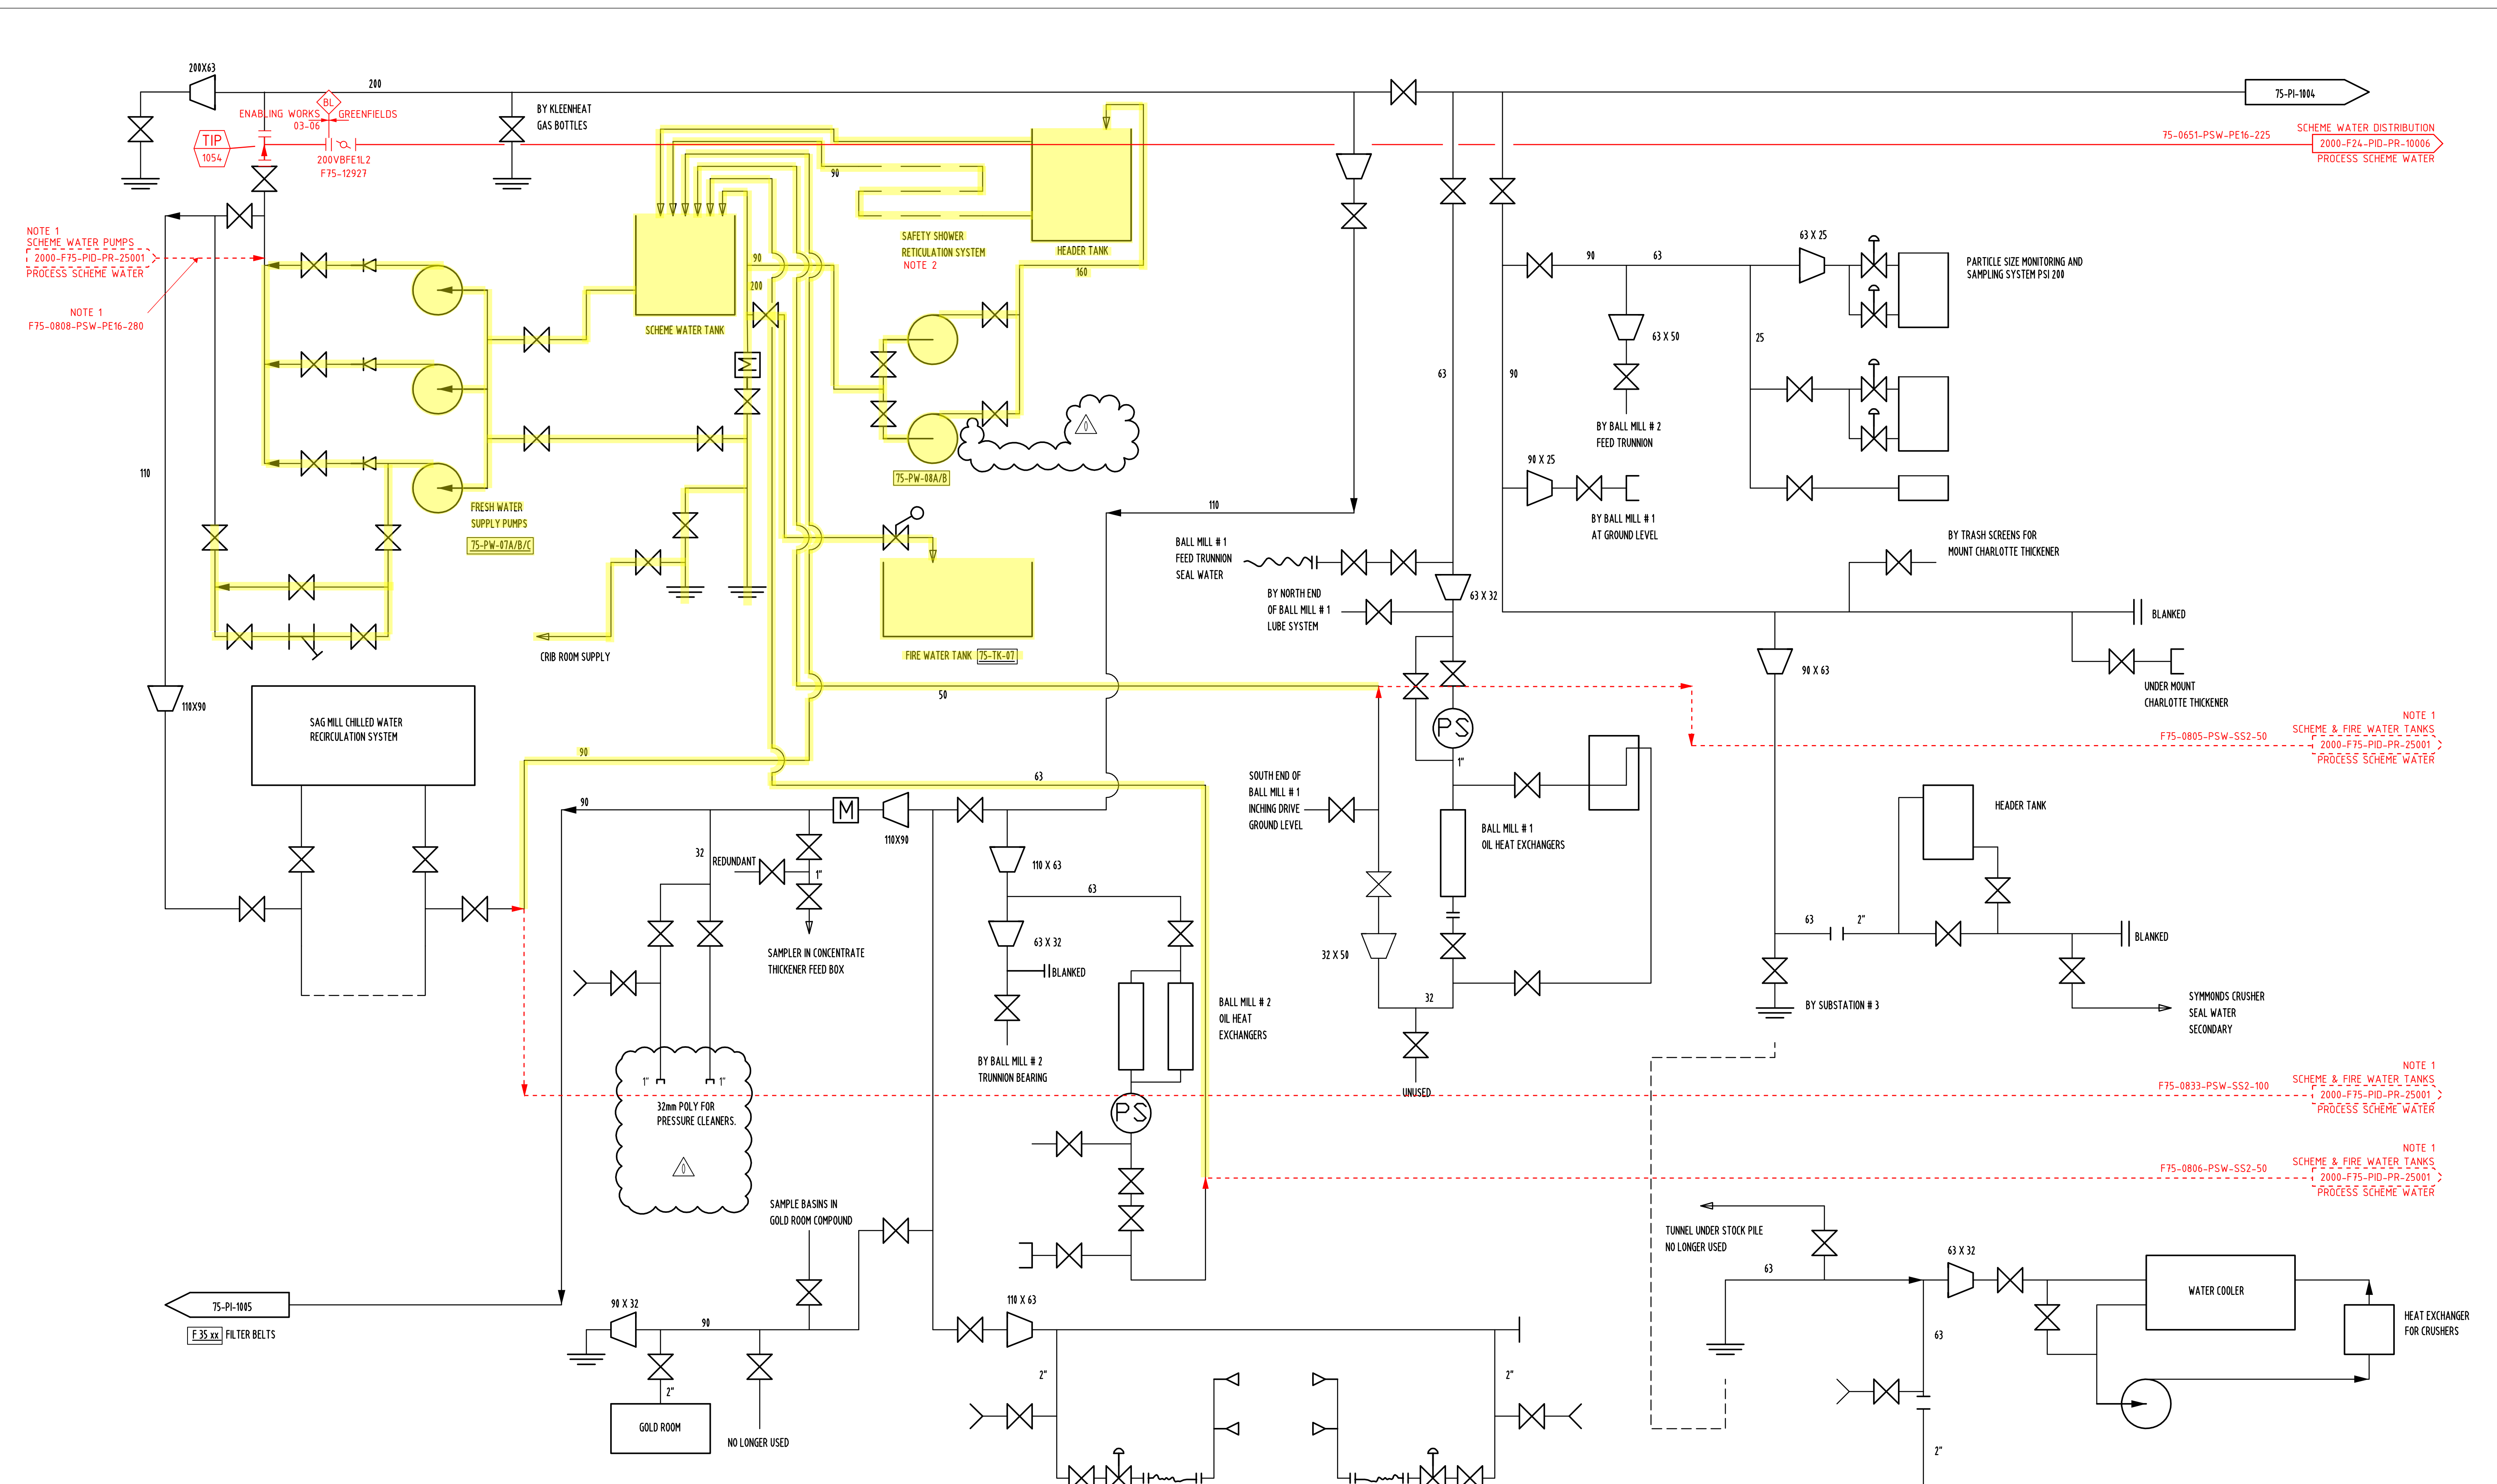

- NOTES:**
- 1. SCHEME WATER SYSTEM RELOCATED AND UPGRADED PER ENABLING WORKS FOR KCGM GROWTH PROJECT. REFER TO DRAWING 2000-F75-PID-PR-25001
 - 2. SAFETY SHOWER RETICULATION NOT SHOWN ON ANY DRAWING. ENABLING WORKS UPGRADE SHOWN ON 2000-F75-PID-PR-25002.

LEGEND

—	STAGE 1 - NEW
—	STAGE 1 - REMOVE
—	STAGE 1 - DECOMMISSIONED (OTHERS)
—	STAGE 2 - NEW
—	STAGE 2 - REMOVE
—	STAGE 2 - DECOMMISSIONED (OTHERS)

KCGM GROWTH PROJECT				
DRAWING NO. 2000-F75-PID-PR-10008				
REV	DATE	DESCRIPTION	CHECK	TECH APP
0	31MAR25	APPROVED FOR CONSTRUCTION		

--	--	