


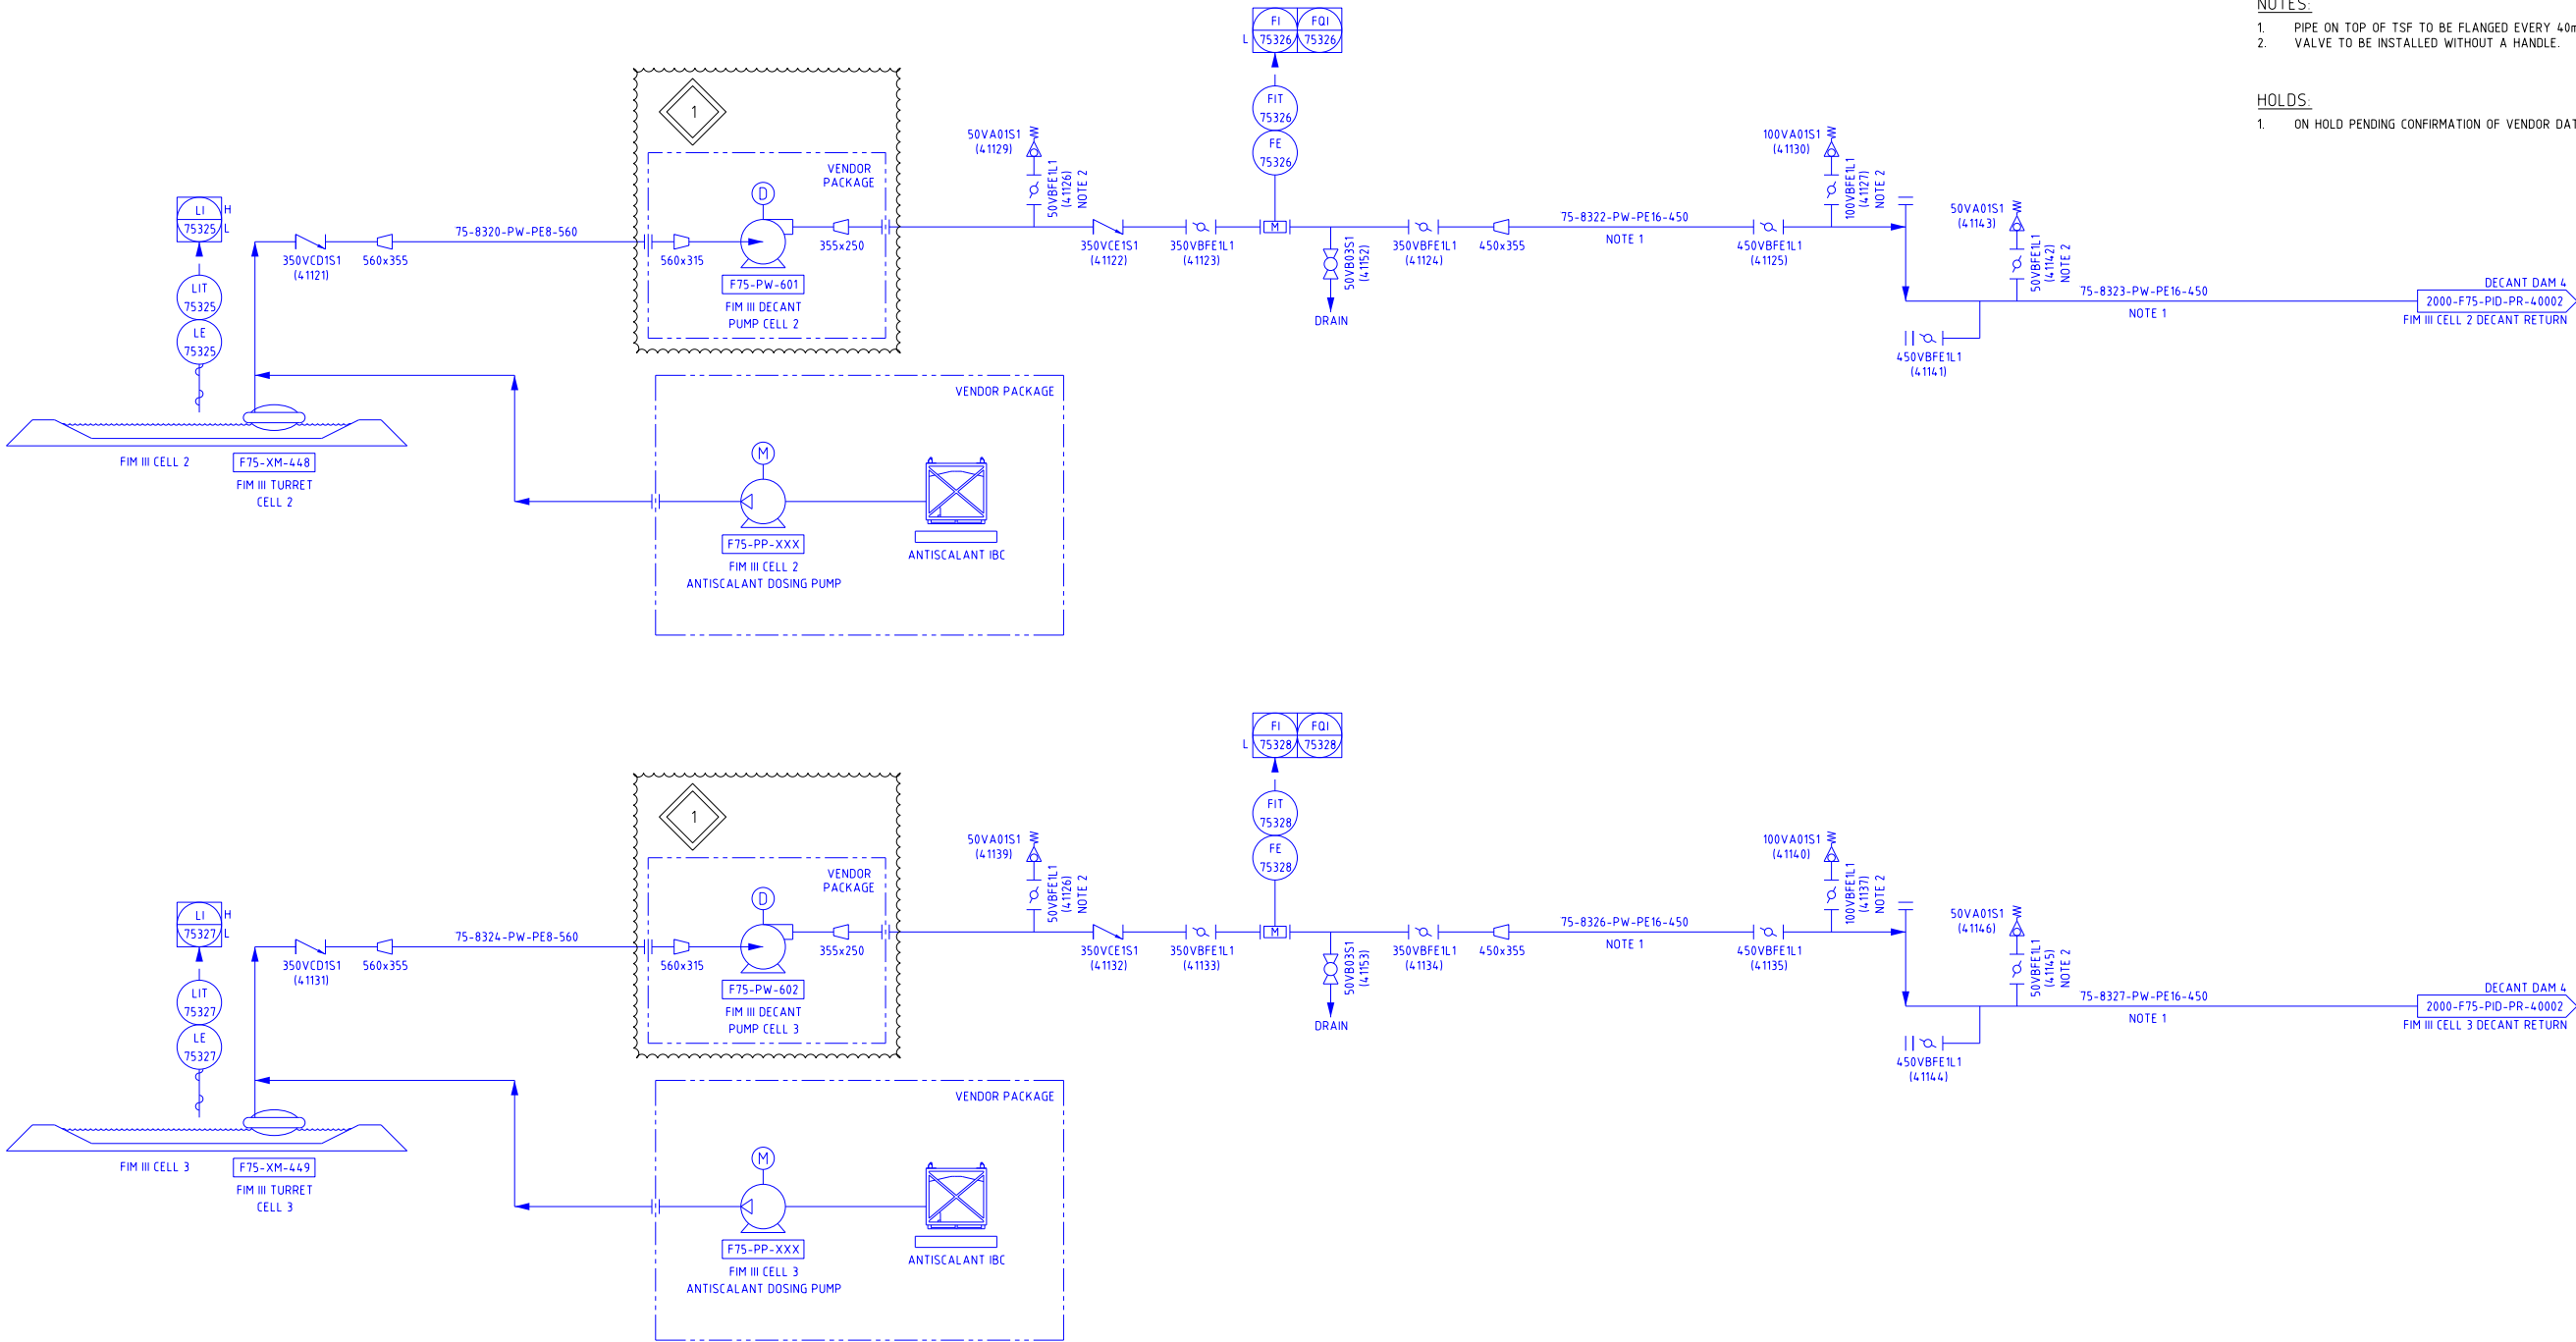

APPROVED FOR
CONSTRUCTION

DRG No	REV	DATE	DESCRIPTION	DRAW	CHECK	DESIGN	TECH APP	PROJ APP
	0	05DEC24	APPROVED FOR CONSTRUCTION					



PROJECT: KCGM GROWTH PROJECT			
TITLE: WATER SERVICES FIM III DECANT - SHEET 2 OF 2 PIPING AND INSTRUMENTATION DIAGRAM			
SHEET A1	SCALE NTS	DRG No 2000-F75-PID-PR-40003	REVISION 0