


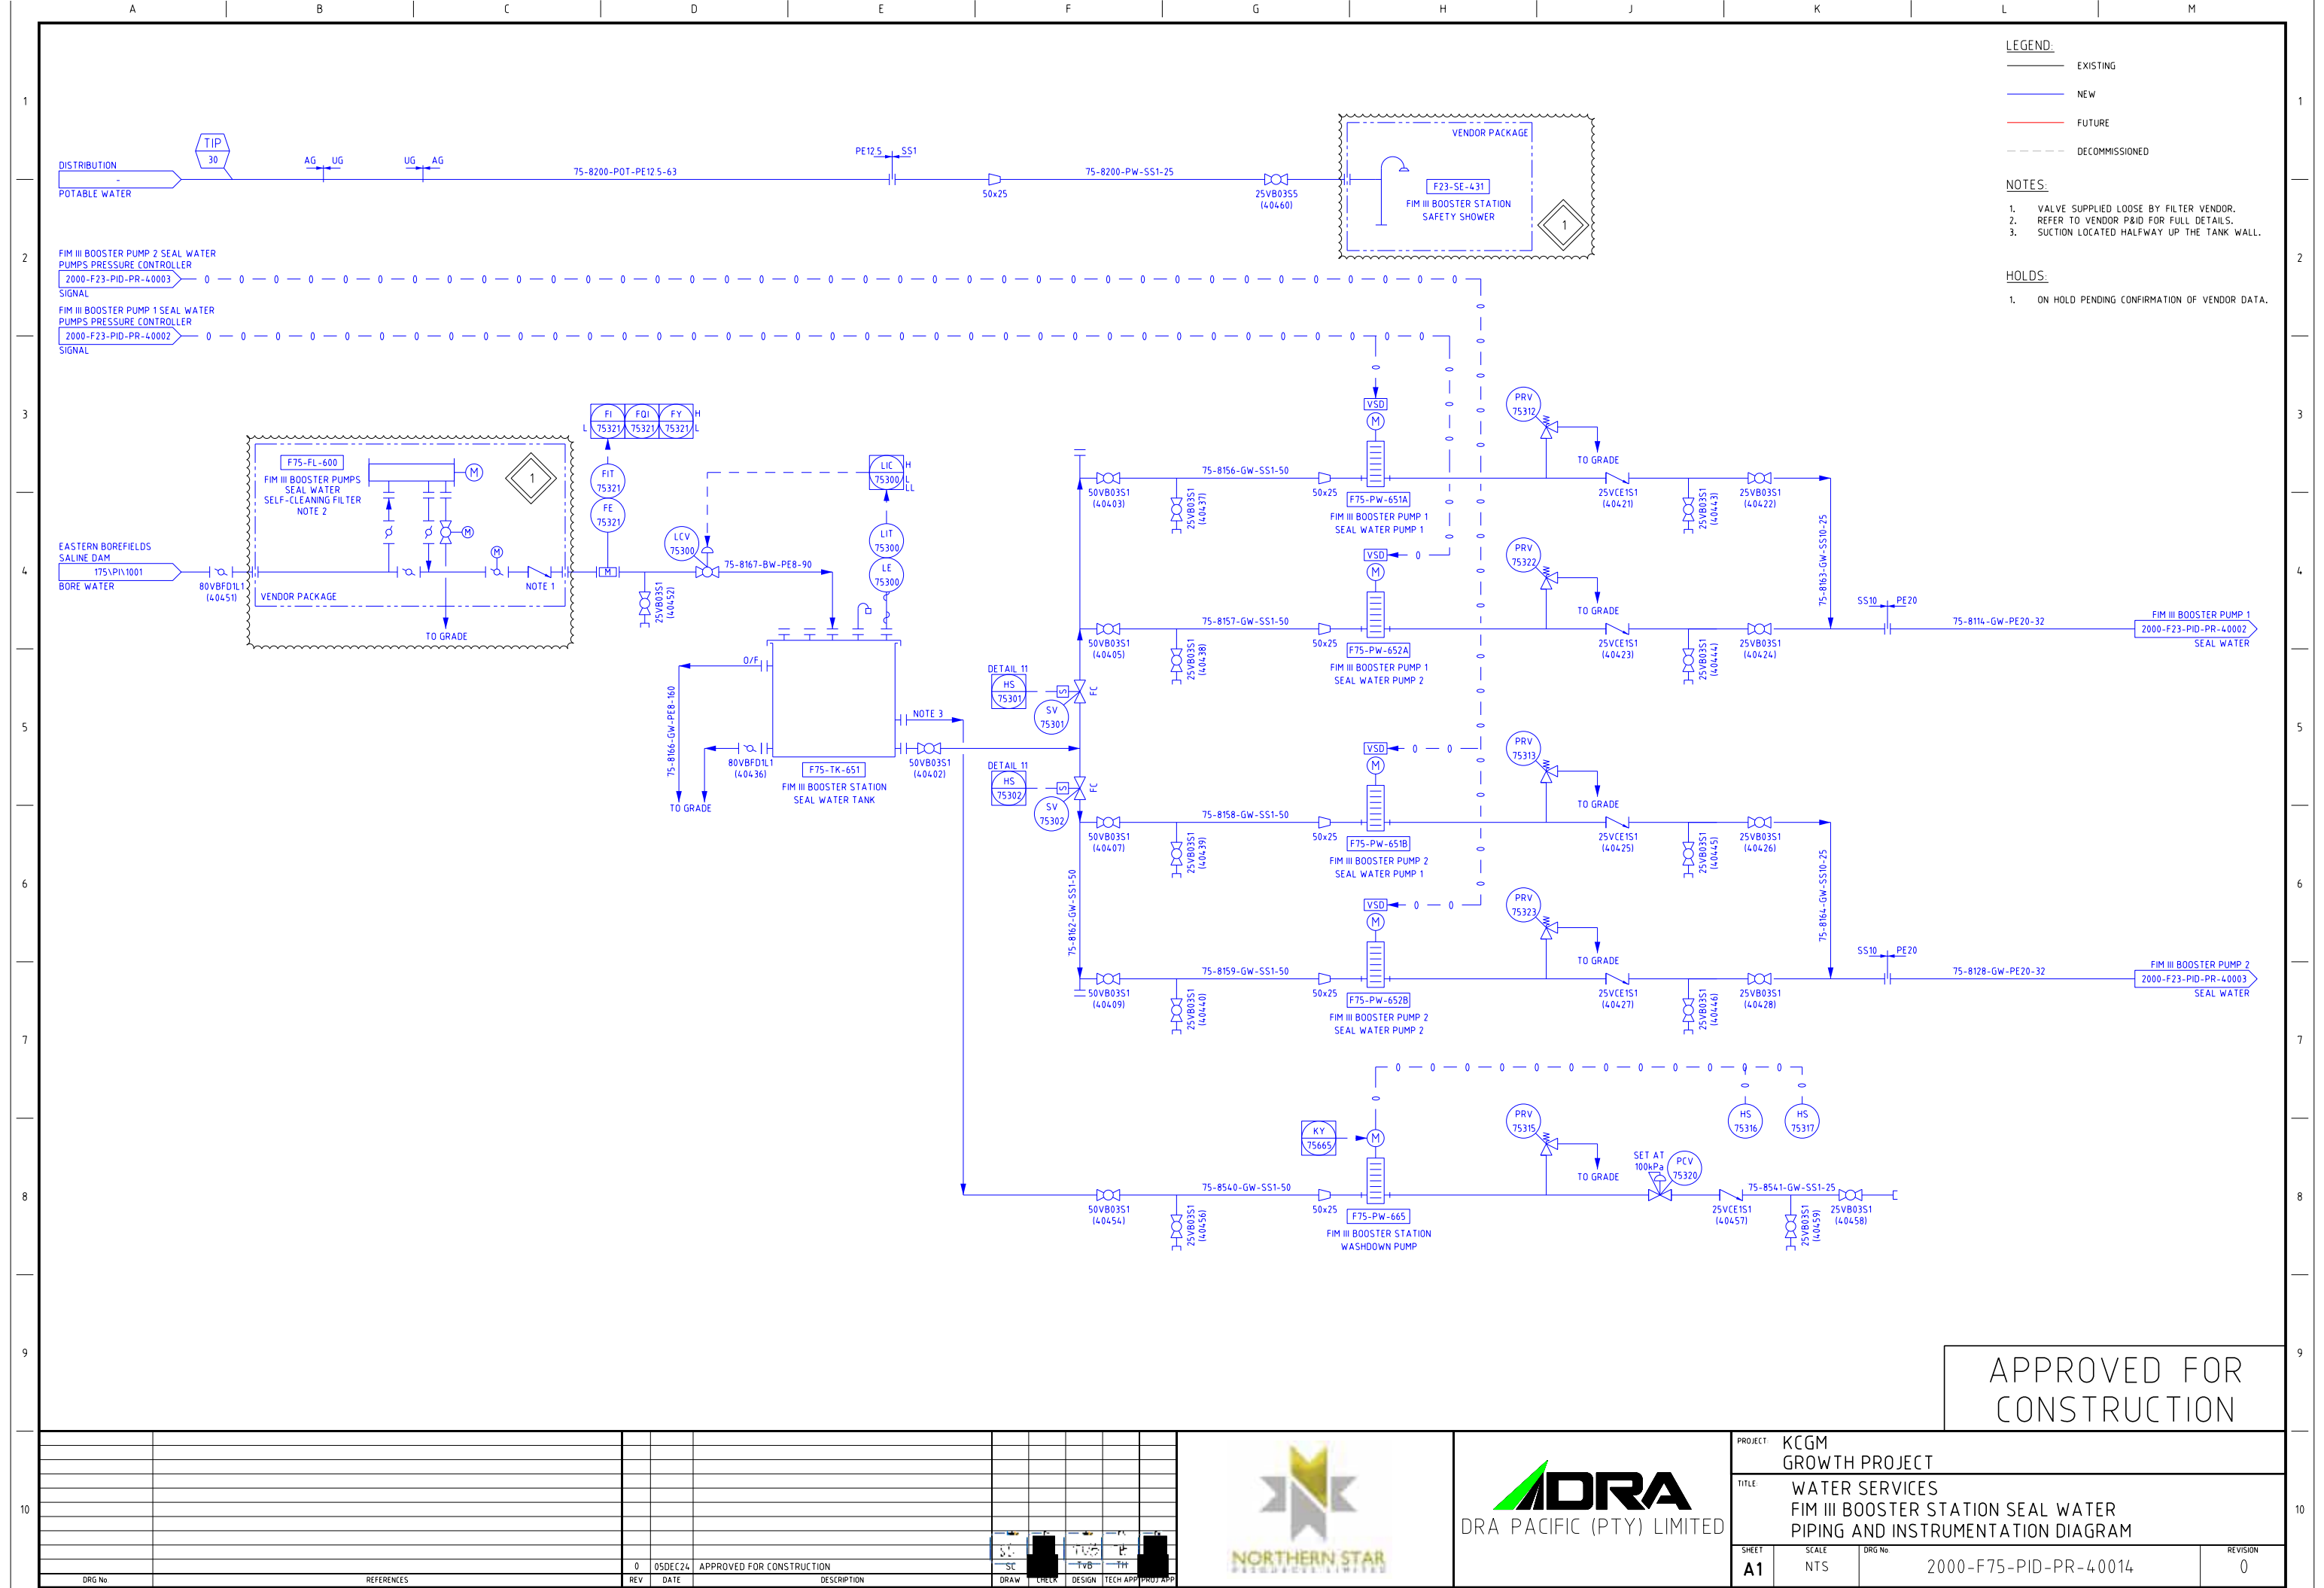

PROJECT: KCGM GROWTH PROJECT		TITLE: WATER SERVICES FIM III BOOSTER STATION SEAL WATER PIPING AND INSTRUMENTATION DIAGRAM	
SHEET: A1	SCALE: NTS	DRG No: 2000-F75-PID-PR-40014	REVISION: 0

DRG No	REV	DATE	DESCRIPTION	DRAW	CHECK	DESIGN	TECH APP	PROJ APP
	0	05DEC24	APPROVED FOR CONSTRUCTION					