


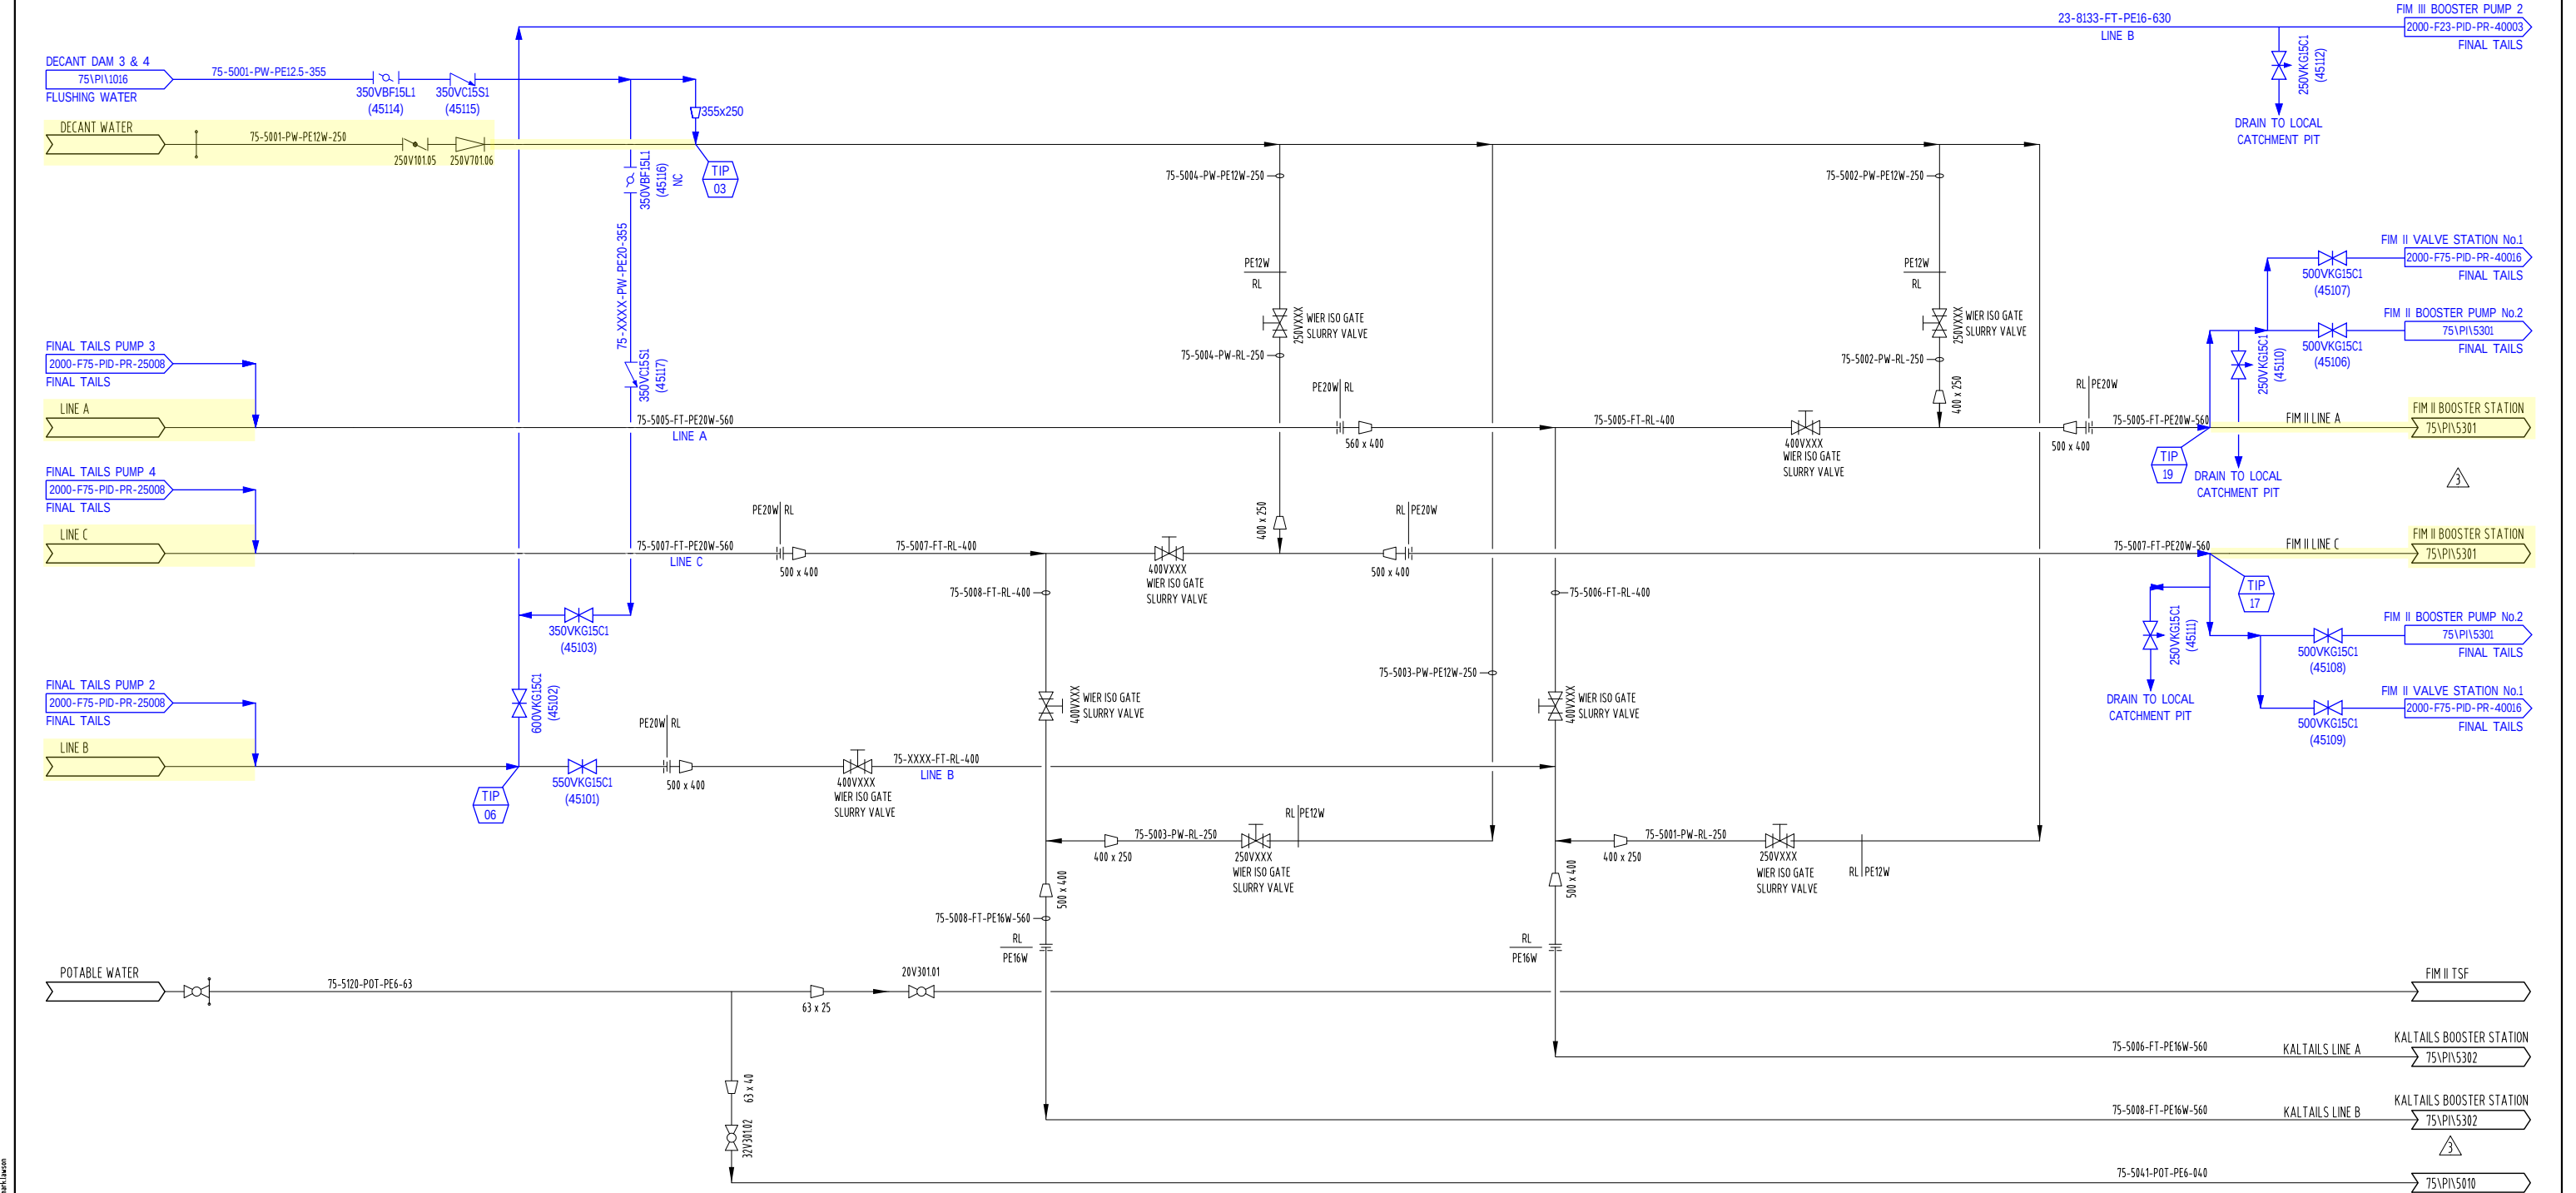

KCGM GROWTH PROJECT

DRAWING NO.
2000-F75-PID-PR-40021

REV	DATE	DESCRIPTION	CHECK	TECH APP
0	05DEC24	APPROVED FOR CONSTRUCTION		

LEGEND

EXISTING

NEW

FUTURE

DECOMMISSIONED

DECOMMISSIONED

PLOT DATE: 22/02/20 09:43 - Cad File: P:\A051 - Kallails Recommissioning\10 CAD\21\051-2-2-4010.dwg [0251-2-2-4010] - Printed by mark lawson										MAL										NTS										FIMSTON PLANT WATER TREATMENT FIMSTON KALTAILS TSF RECOMMISSIONING PIPING & INSTRUMENTATION DIAGRAM - KEARNS CORNER										SIZE										DRAWING NUMBER										REV										KALGOORLIE CONSOLIDATED GOLD MINES PTY. LTD.										ABN 009 377 619 003	
4 21 JULY 2019 GENERAL REVISION										AG										CHECKED										APPROVED										DATE										DATE										