


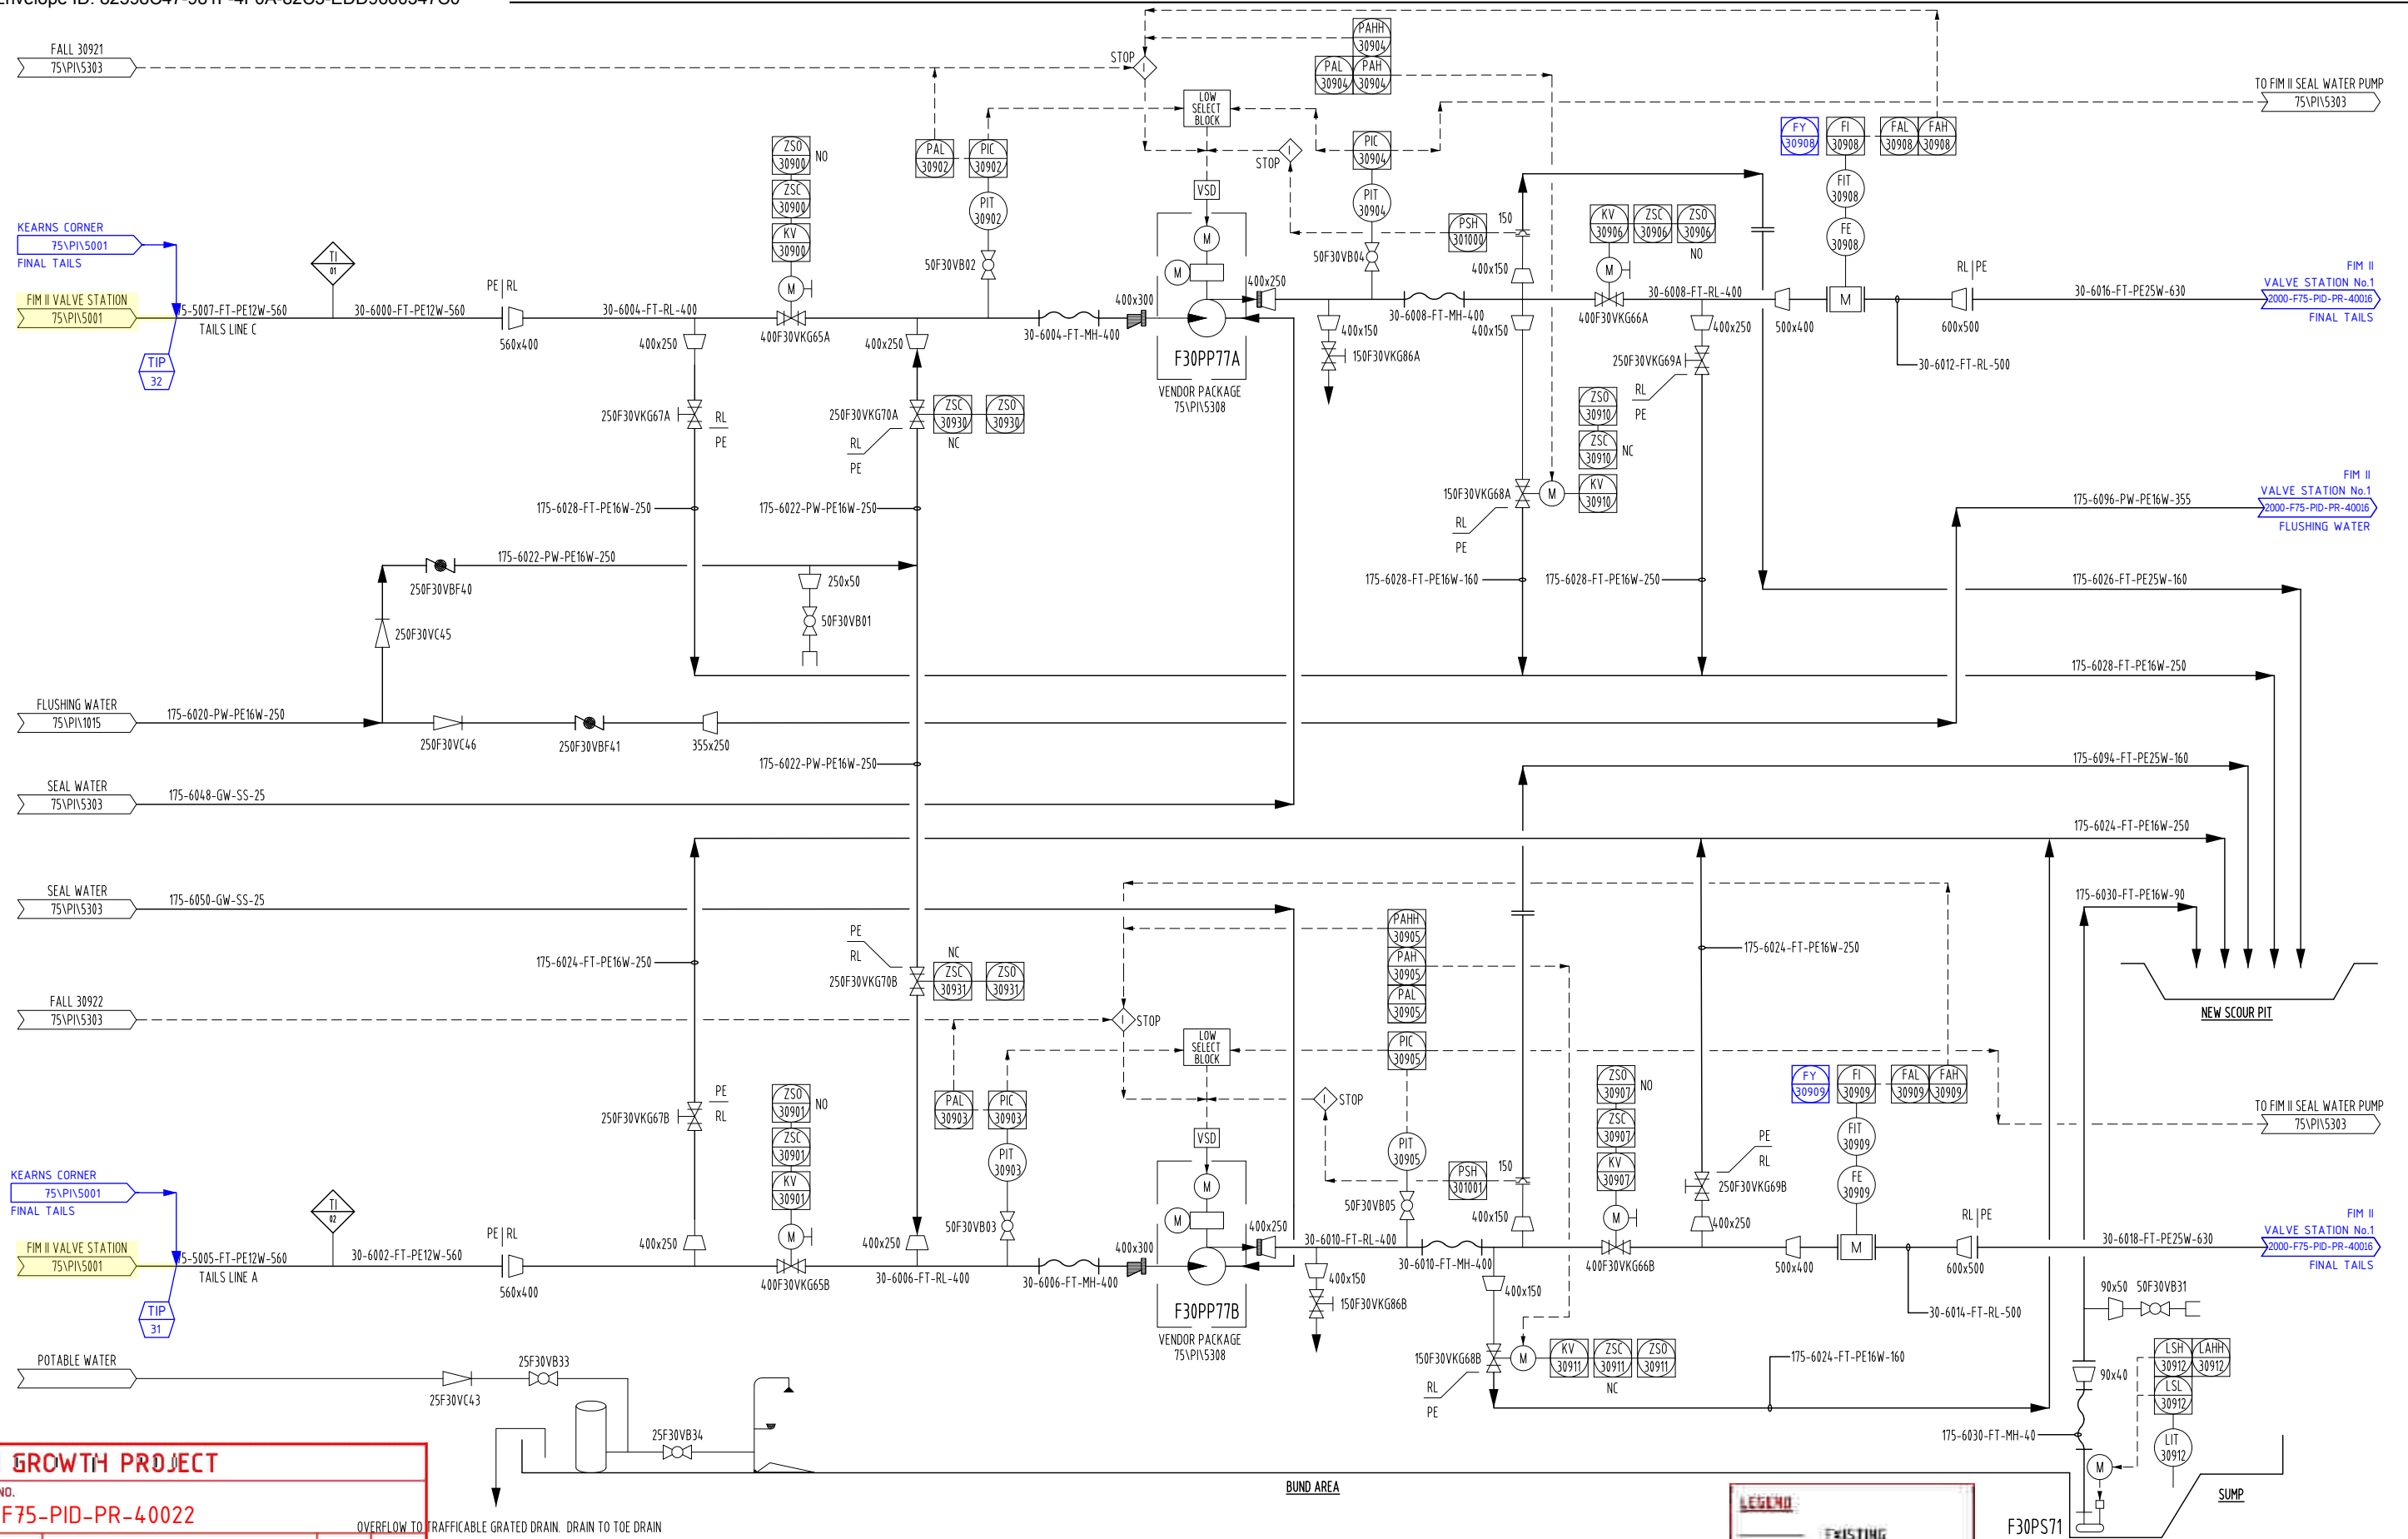

KCGM GROWTH PROJECT				
DRAWING NO.				
2000-F75-PID-PR-40022				
				OVERFLOW TO
0	05DEC24	APPROVED FOR CONSTRUCTION		
REV	DATE	DESCRIPTION		CHECK
				TECH APP

[illegible]