


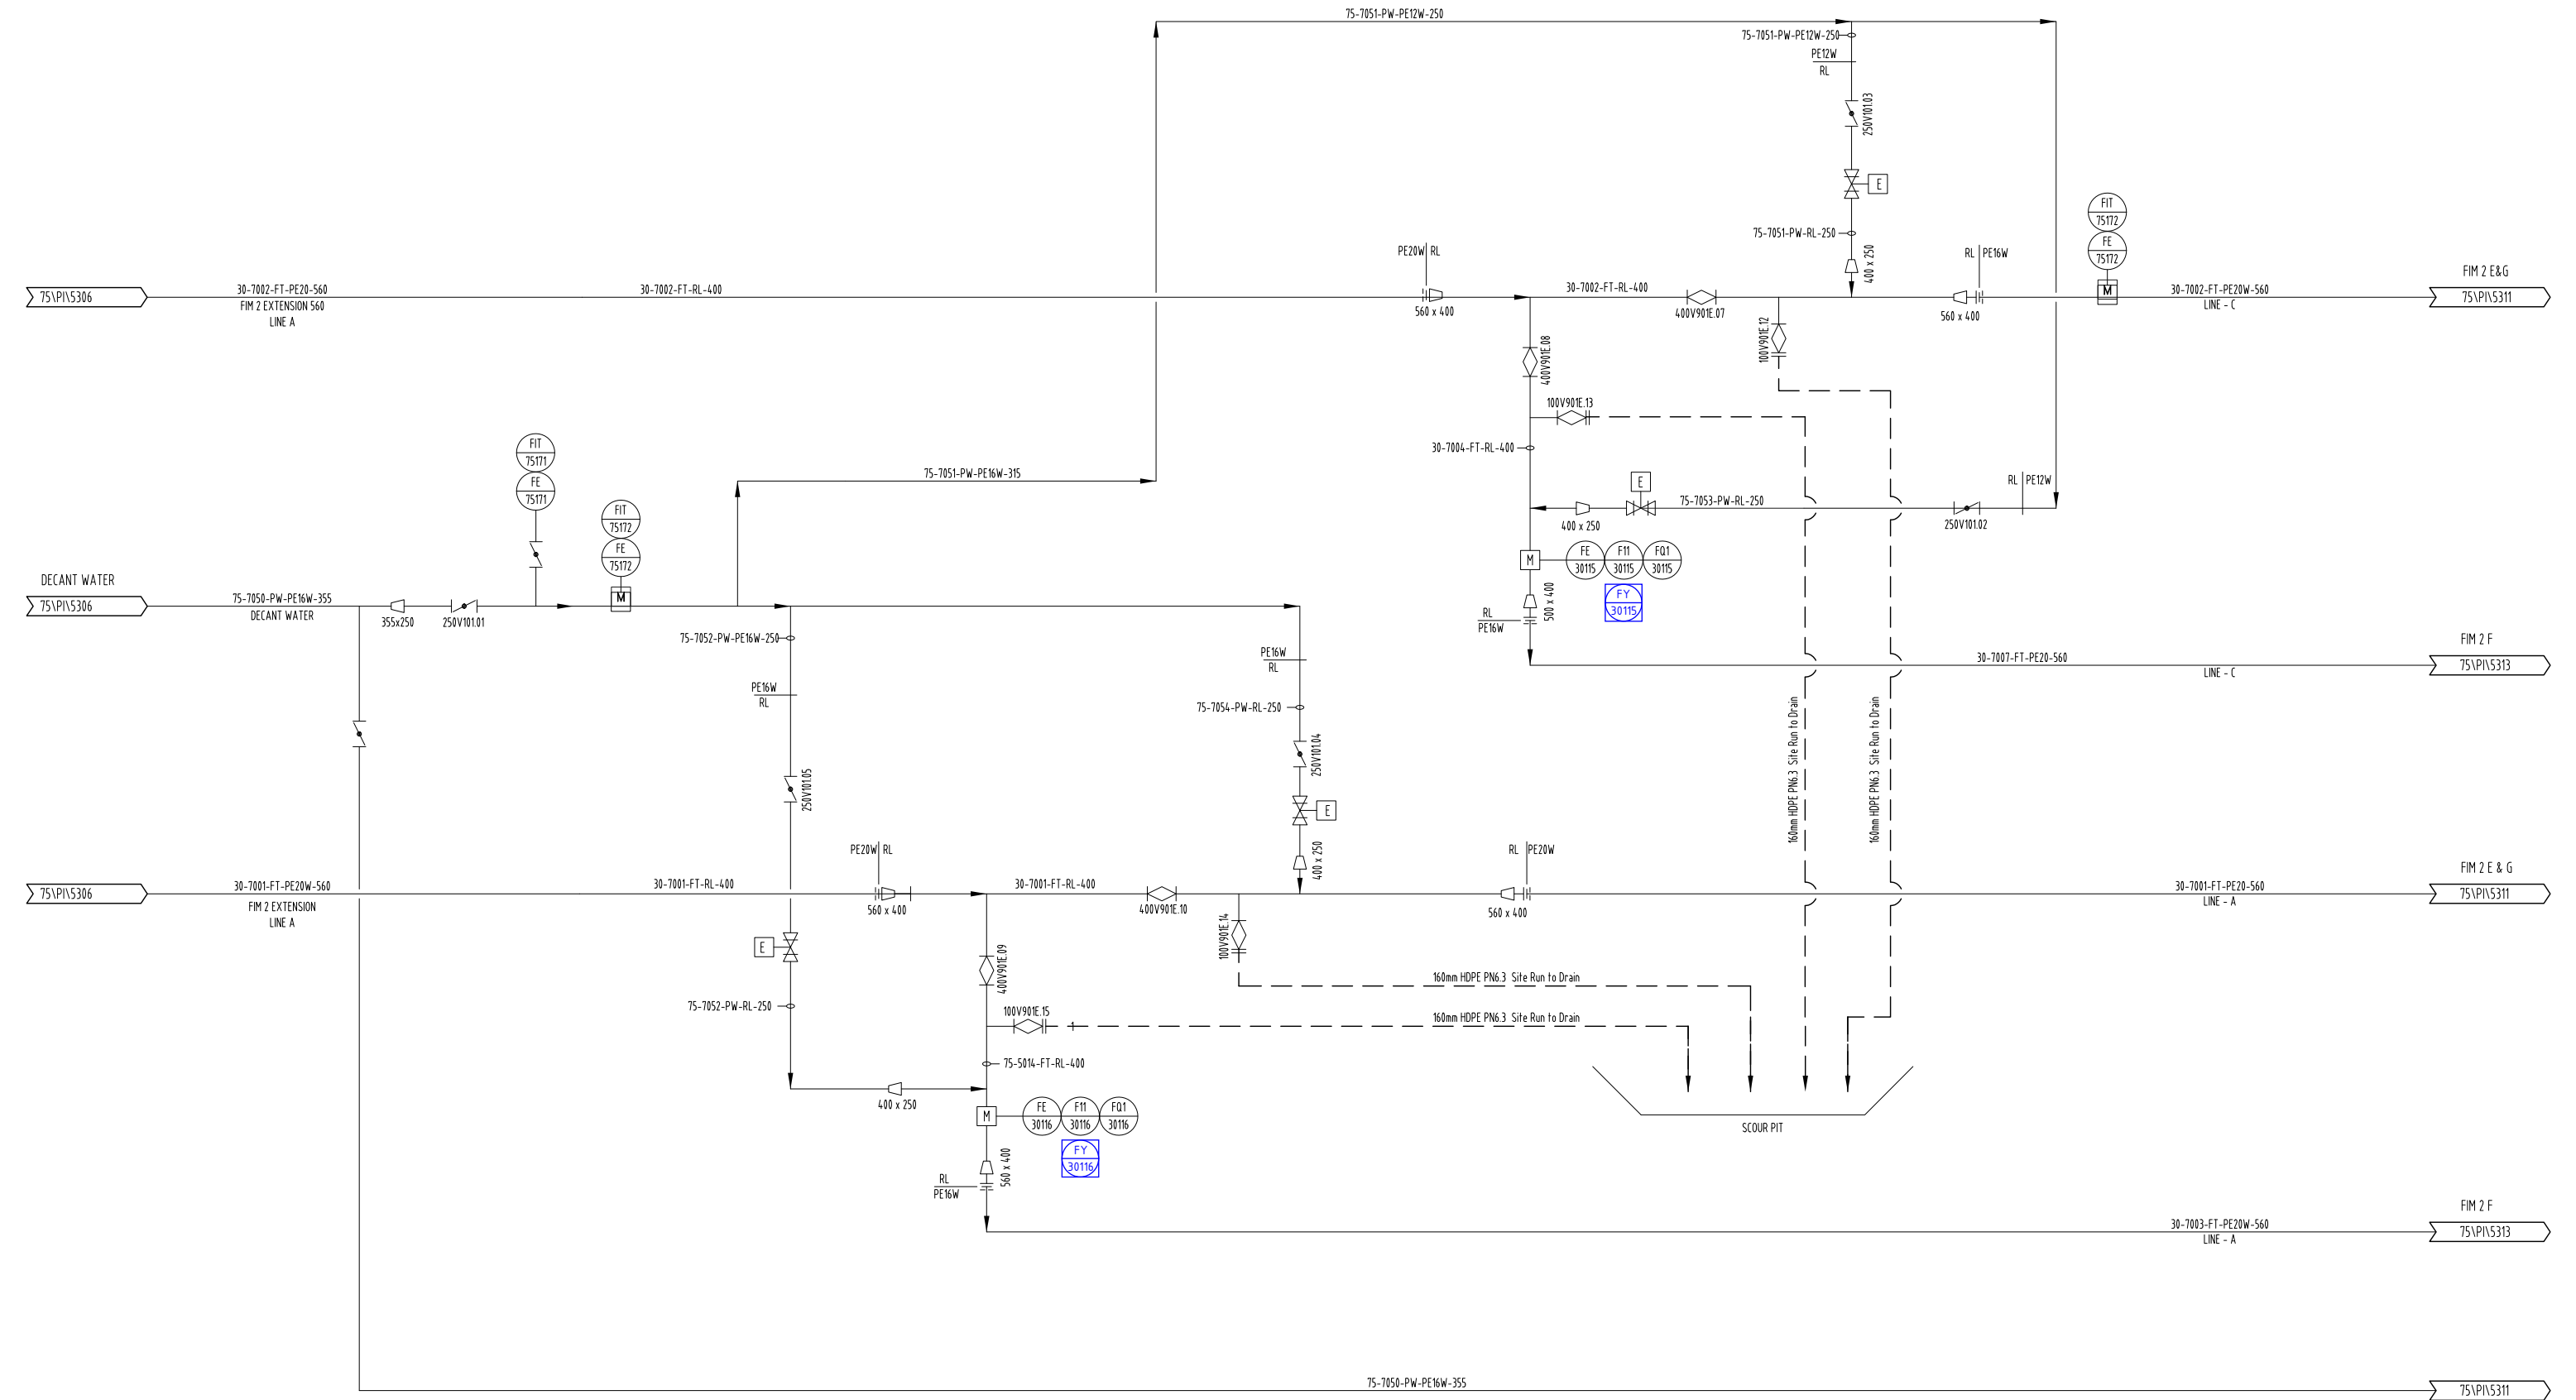

KCGM GROWTH PROJECT				
DRAWING NO.				
2000-F75-PID-PR-40025				
0	05DEC24	APPROVED FOR CONSTRUCTION		
REV	DATE	DESCRIPTION		CHECK
				KEEL APP

LEGEND:

- EXISTING
- NEW
- FUTURE
- DESIGNATED
- DESIGNATED

VALVE STATION No.2

LEGEND

— — — — — EXISTING

————— NEW

 WILSHAW		+61 8 9479 0800 wilshaw.com.au	
WILSHAW DWG No.	REV	JOB No	7117

[illegible]