


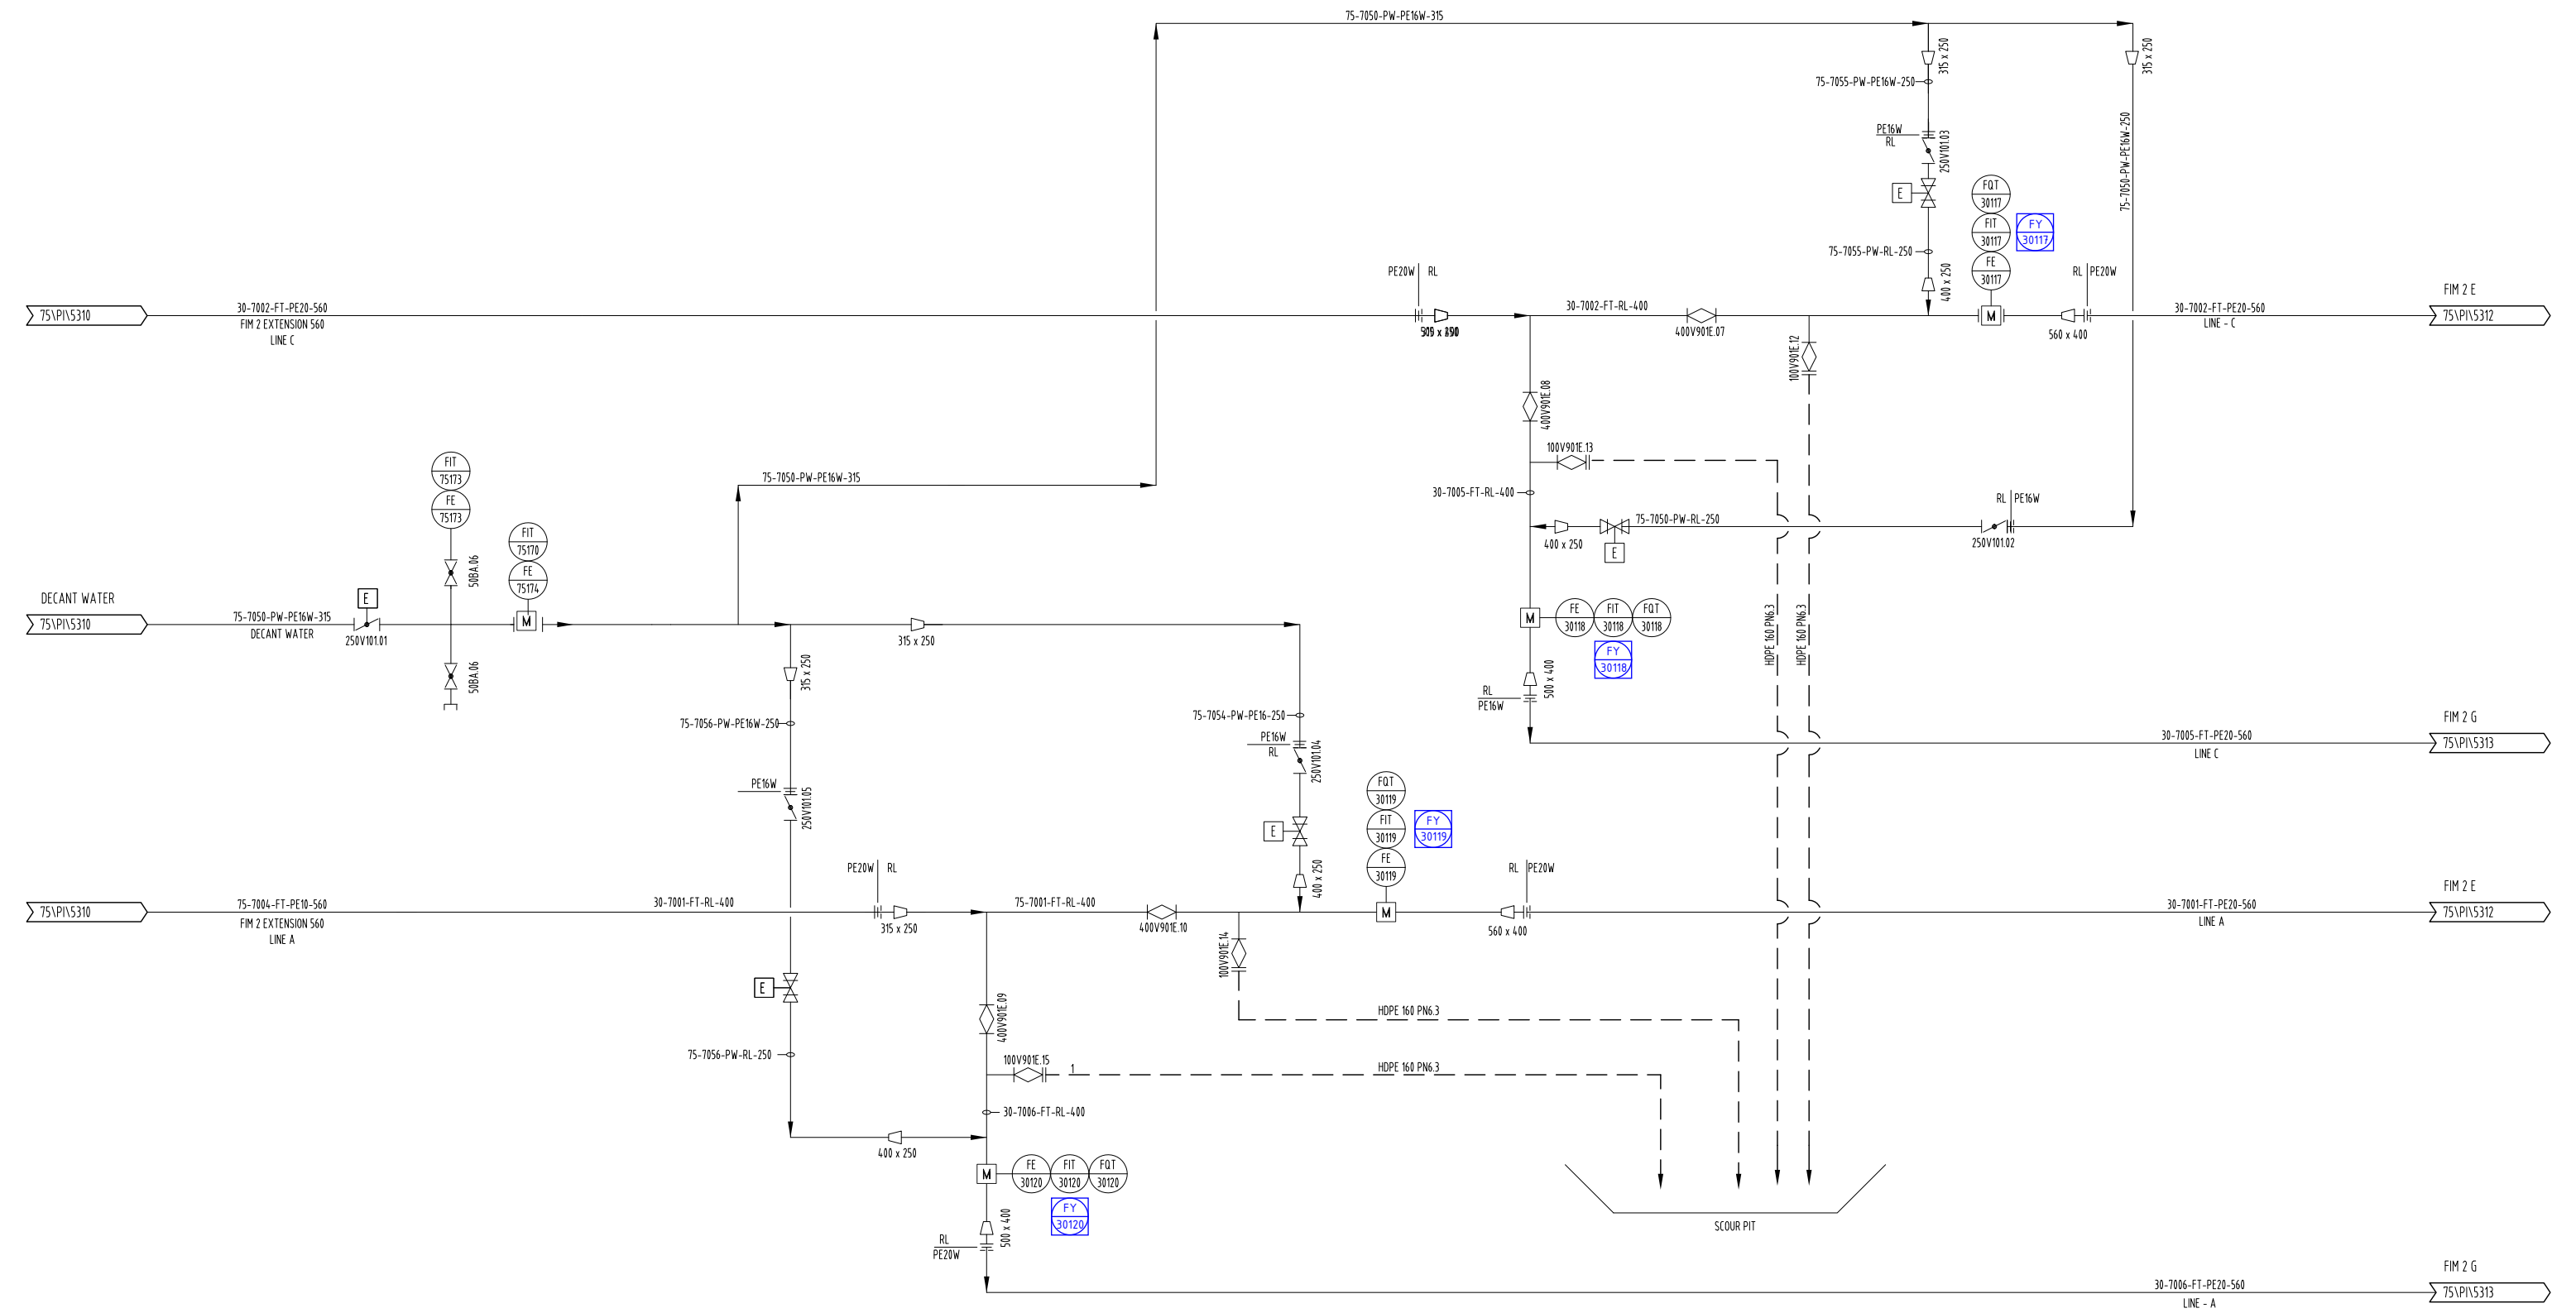

VALVE STATION No.3

LEGEND

KCGM GROWTH PROJECT				
DRAWING NO.				
2000-F75-PID-PR-40026				
0	05DEC24	APPROVED FOR CONSTRUCTION		
REV	DATE	DESCRIPTION		CHECK
				KECH APP

LEGEND:

- EXISTING
- NEW
- FUTURE
- DECOMMISSIONED
- DECOMMISSIONED

EXISTING

NEW



61 8 9479 0800
wilshaw.com.au

WILSHAW DWG No.	REV	JOB No 7117
-----------------	-----	-------------

[illegible]